


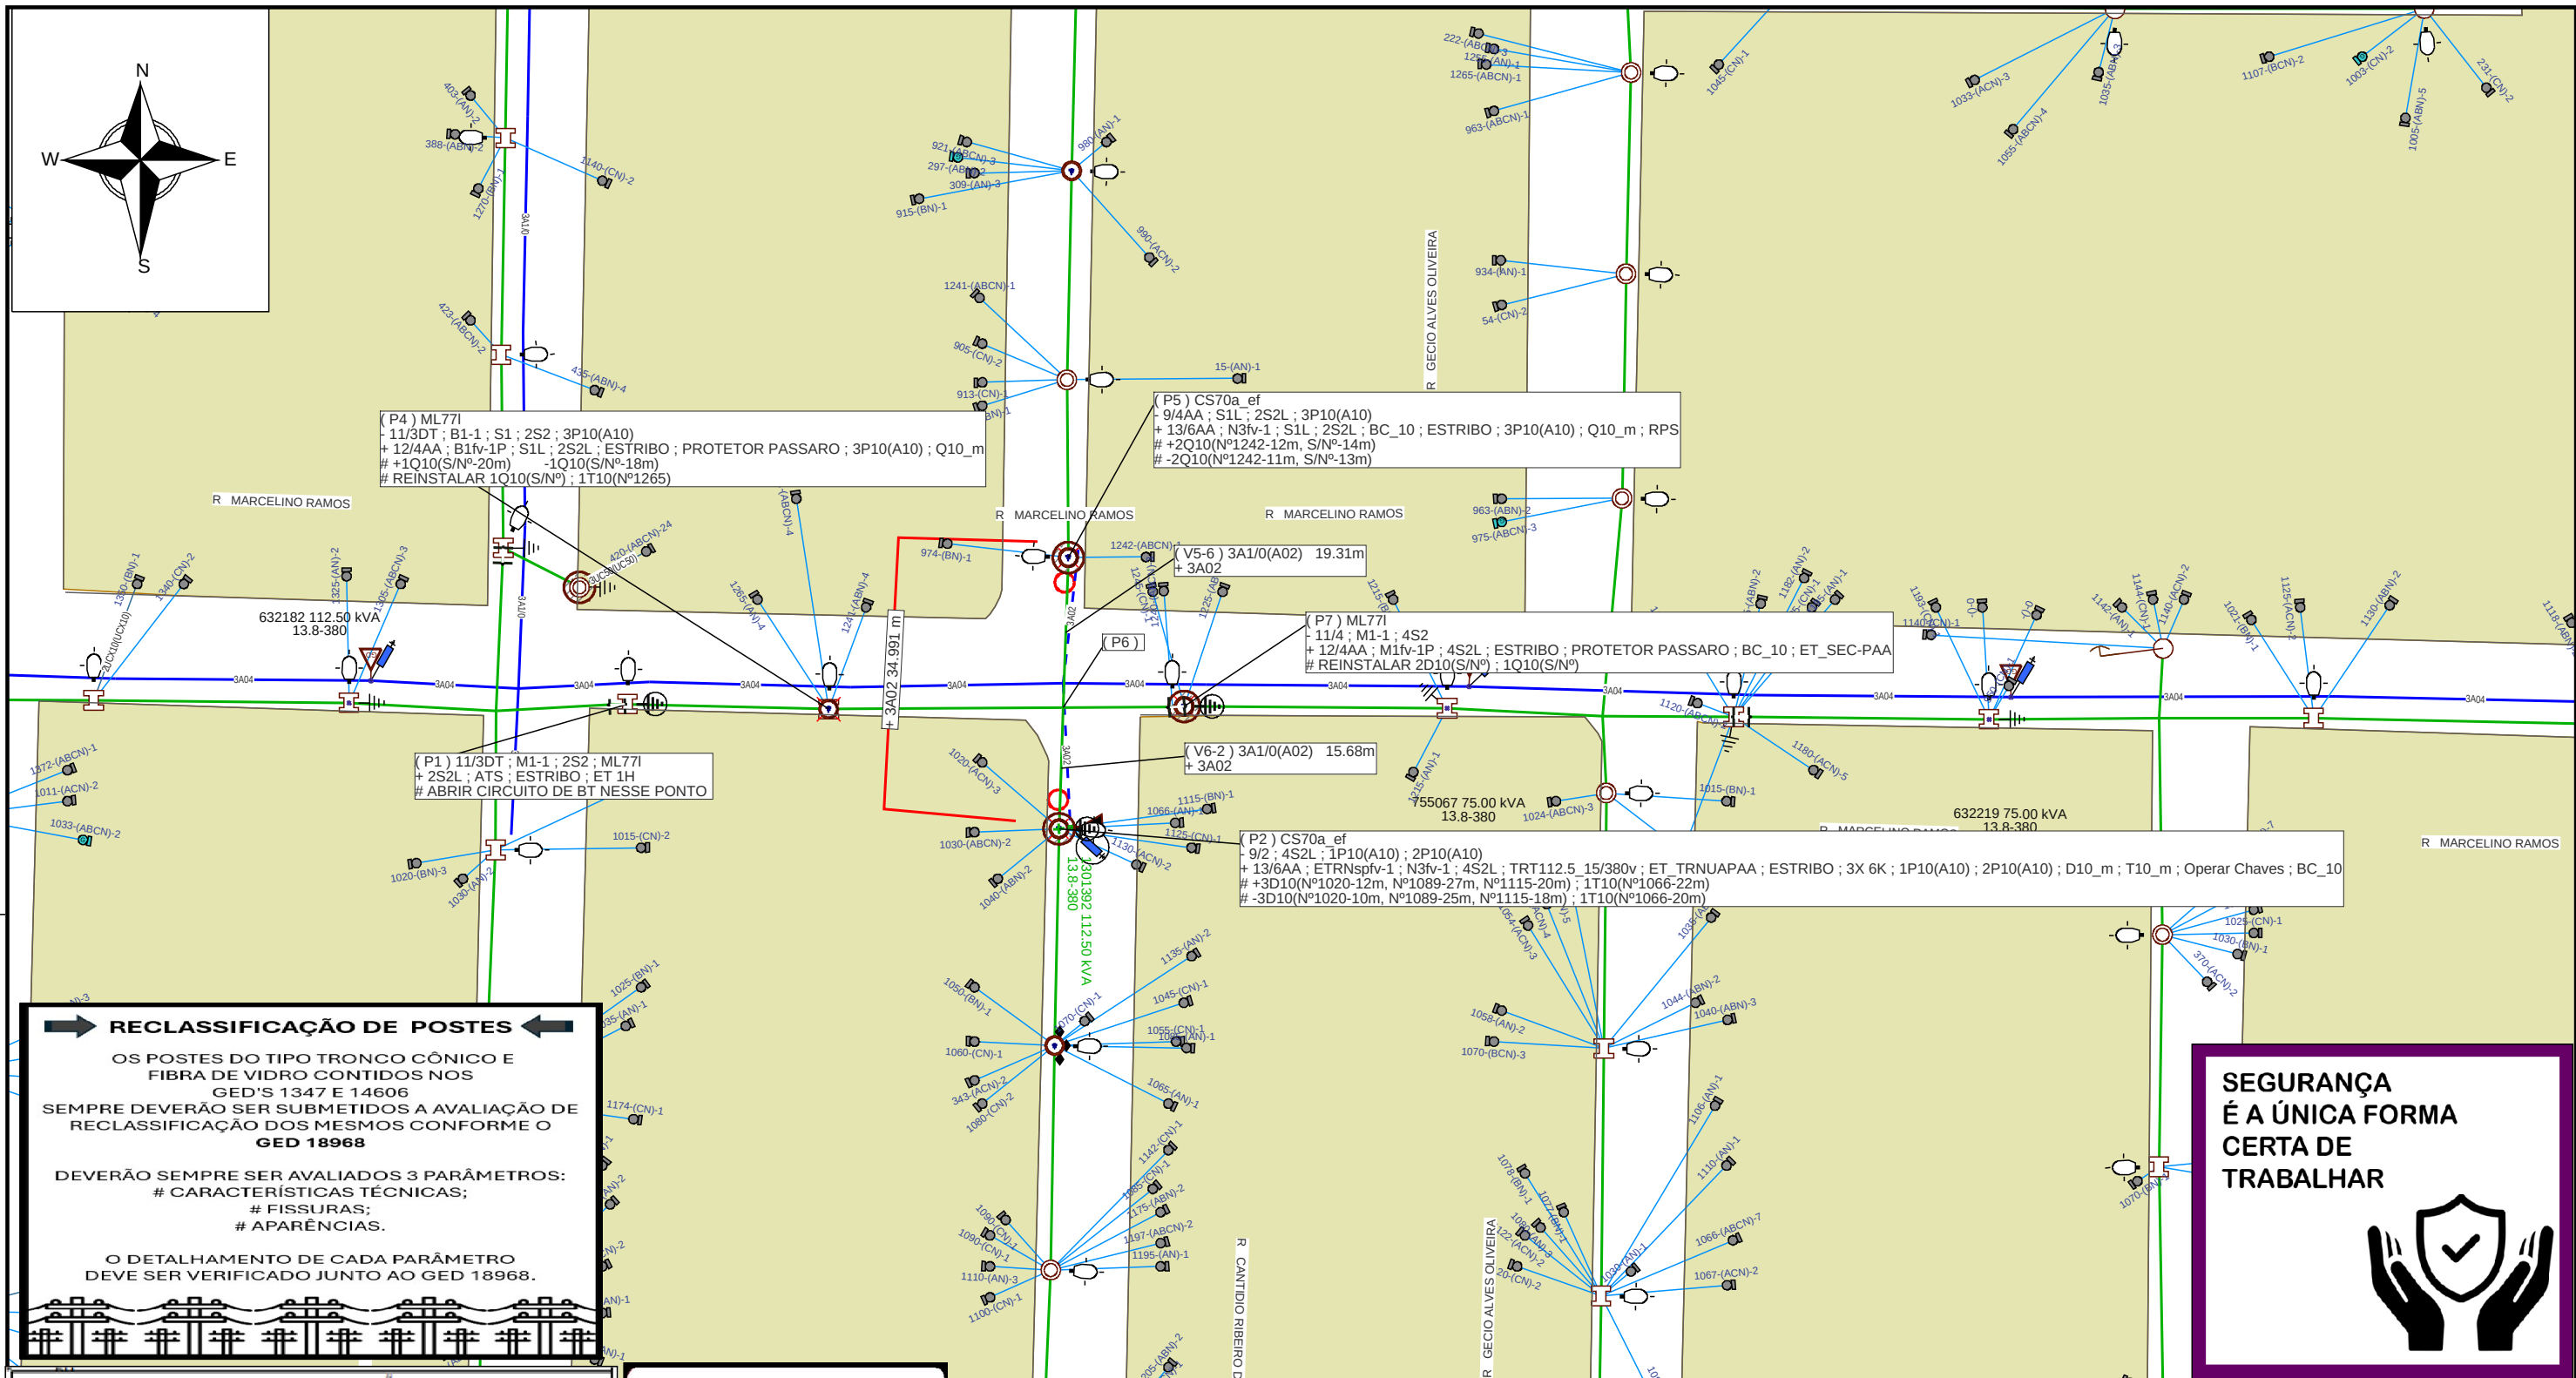

RECLASSIFICAÇÃO DE POSTES

OS POSTES DO TIPO TRONCO CÔNICO E FIBRA DE VIDRO CONTIDOS NOS GED'S 1347 E 14606 SEMPRE DEVERÃO SER SUBMETIDOS A AVALIAÇÃO DE RECLASSIFICAÇÃO DOS MESMOS CONFORME O GED 18968

DEVERÃO SEMPRE SER AVALIADOS 3 PARÂMETROS:

- # CARACTERÍSTICAS TÉCNICAS;
- # FISSURAS;
- # APARÊNCIAS.

O DETALHAMENTO DE CADA PARÂMETRO DEVE SER VERIFICADO JUNTO AO GED 18968.

PLANO DE EXECUÇÃO					
ABRIR CAVAS, PREPARAR OS PONTOS DA OBRA. REALIZAR ATIVIDADES COM LINHA MORTA .					
REALIZAR TODAS AS ATIVIDADES SEGUINDO AS NORMAS DE SEGURANÇA. ESSE PROJETO SÓ PODE SER ALTERADO POR SOLICITAÇÃO DE DI.					
Ação	Equipamento	Número	Clientes	Duração	CHI
Abriu	Chave Fusível	608769	1207	4	4828
Linha Viva?		Não	CHI TOTAL		4828
☐ Poste novo a ser instalado (quando indicado em planta)					

Feedback Para Fábrica de Projetos

Planeje
Use
Teste
Sinalize
Aterre

Gabriel Vergani
Gabriel Vergani
Gerência de Processos de Obras e Manutenção | DROP
Técnico de Análise e Projetos
CFT: 040.224.970-41

		Gerência de Obras e Manutenção			
		Município: Caxias do Sul			
Cliente: RGE SUL DISTRIBUIDORA DE ENERGIA S/A					
Obra: Plano Sobrecarga 2025					
Endereço: R MARCELINO RAMOS, S CAETANO, CAXIAS DO SUL					
Responsável Técnico:		Escala: 1:850	Data: 02/12/2025		
 Eng. Ederson Paulo Vogel CREA: RS135794 ART: 10911826		Classe de isolamento: 15kV	Nota: 000006783053		
		Projetista: Gabriel Vergani	Folha 1		
		Projeto: 000007936657	Levantador: Adelar Miguel Ferreira		