


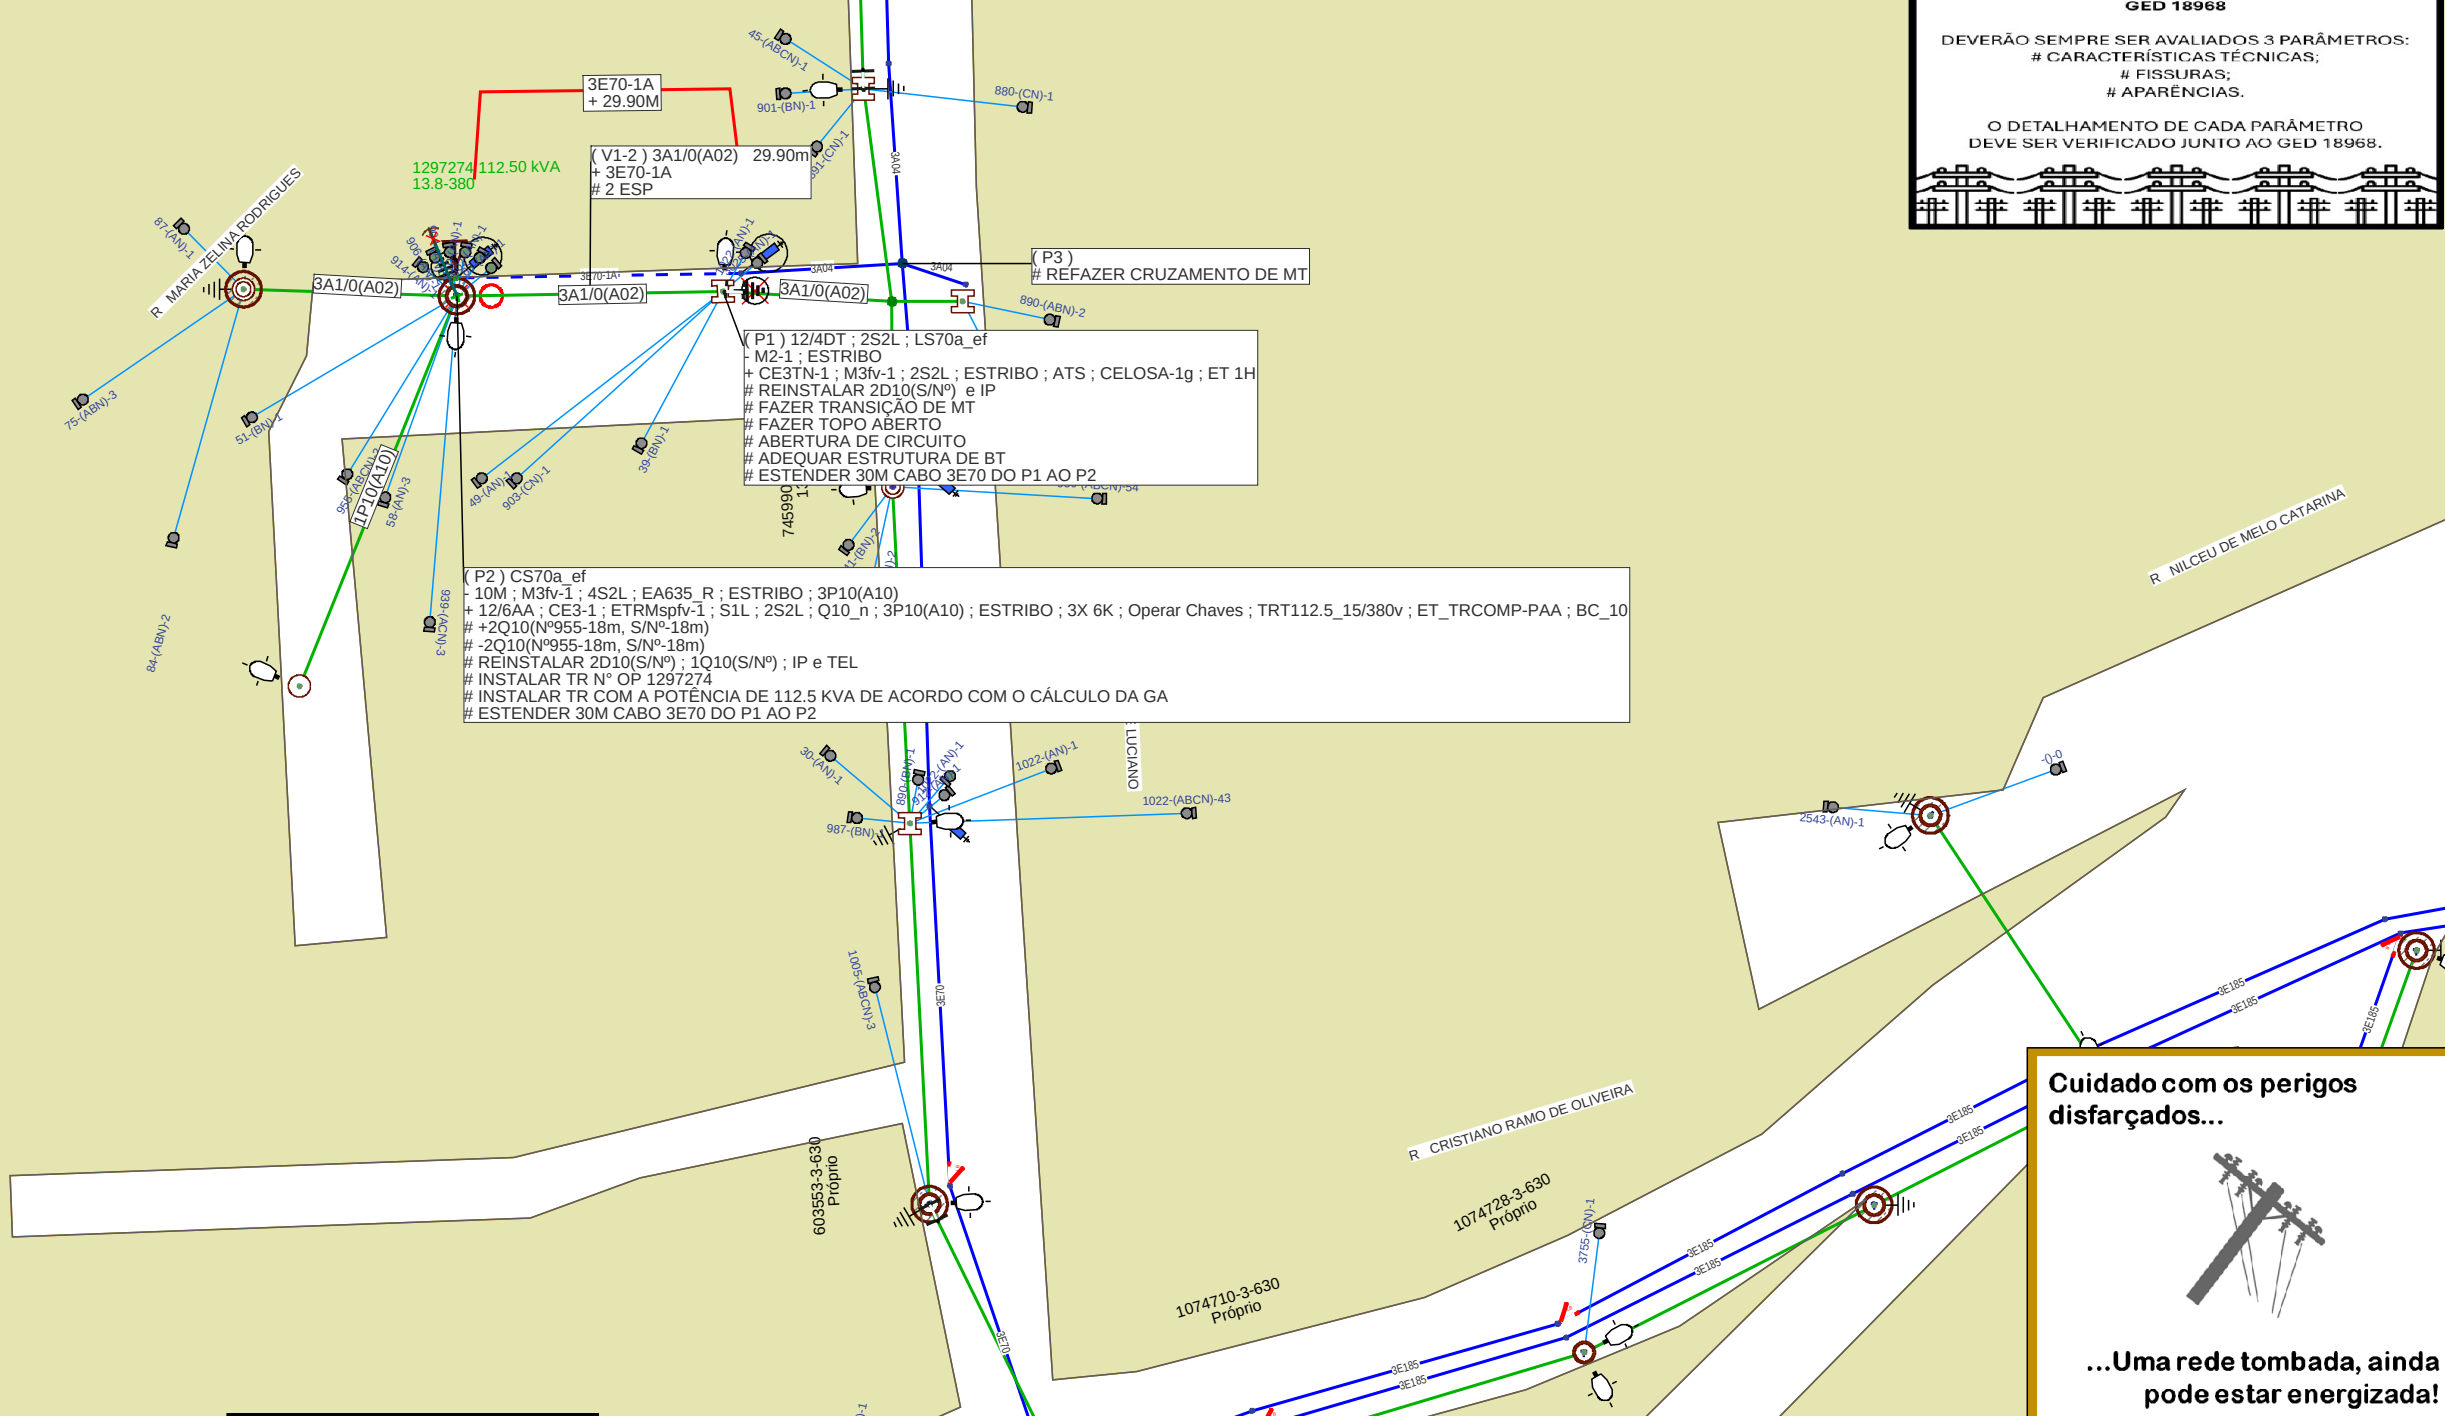

**Cuidado com os perigos
disfarçados...**



**...Uma rede tombada, ainda
pode estar energizada!**

Executar a obra seguindo todos os passos de segurança!

MANOBRAR EQUIPAMENTO REPRESENTADO ABAIXO E REALIZAR A SUBSTITUIÇÃO DOS POSTES INDICADOS. ATENTAR-SE À INSTALAÇÃO DE PLACAS DE Nº OPERATIVO. EXECUTAR A ATIVIDADE SEGUINDO TODAS AS NORMAS DE SEGURANÇA.


SEGUIR ORIENTAÇÕES CONFORME PROJETO, EM CASO DE ALTERAÇÕES SOLICITAR VIA D.I.

Ação	Equipamento	Número	Clientes	Duração	CHI
Abrir	Chave Faca	603553	305	5	1525
Linha Viva?		Não	CHI TOTAL	1525	

☐ Poste novo a ser instalado (quando indicado em planta)



FeedBack Para Fábrica de Projetos

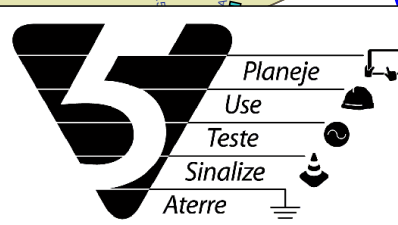

Cauan K. Prestes
Cauan Luis kochenborger Prestes
 Gerência de Processos de Obras e Manutenção | DROP
 Técnico de Análise e Projetos
 CFT: 04355340090



Gerência de Obras e Manutenção

Município: Caxias do Sul

Cliente: RGE SUL DISTRIBUIDORA DE ENERGIA S/A

Obra: Plano Sobrecarga 2025

Endereço: R ALEXANDRE LUCIANO - DESVIO RIZZO - CAXIAS DO SUL

Responsável Técnico:

Eng. Ederson Paulo Vogel
CREA: RS135794 ART: 10911826

Escala: 1:850

Classe de isolação: 15kV

Projeto: CAUAN
PRESTES

Data: 14/11/2025

AL: CXH44

Projeto: 000007927056

Nota:	000006783061
-------	--------------

Folha 1

Levantador: Marcio Bedin
