


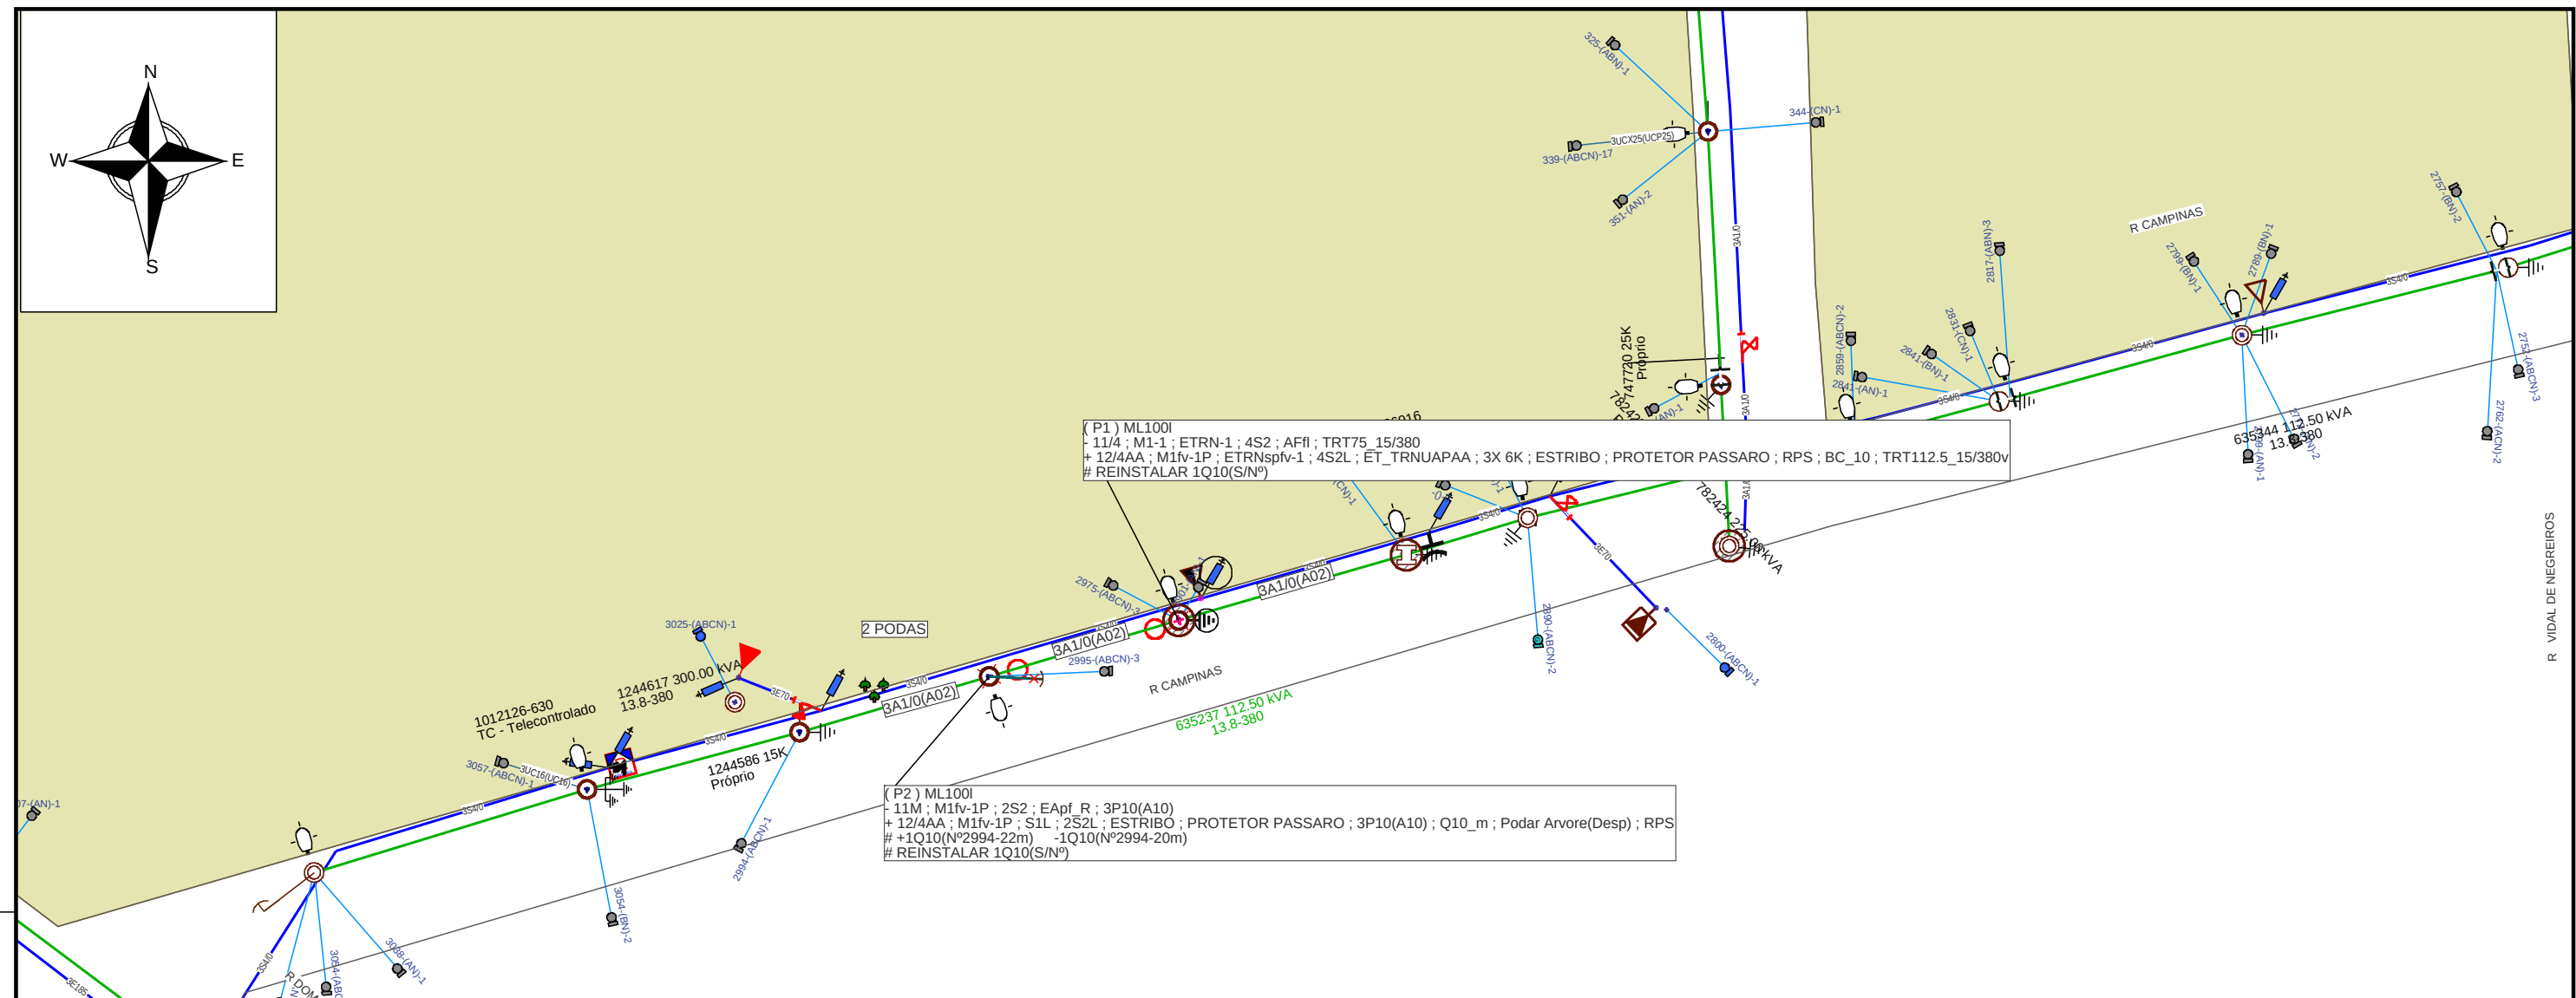

OS POSTES DO TIPO TRONCO CÔNICO E
FIBRA DE VIDRO CONTIDOS NOS
GED'S 1347 E 14606
SEMPRE DEVERÃO SER SUBMETIDOS A AVALIAÇÃO DE
RECLASSIFICAÇÃO DOS MESMOS CONFORME O
GED 18968

DEVERÃO SEMPRE SER AVALIADOS 3 PARÂMETROS:
CARACTERÍSTICAS TÉCNICAS;
FISSURAS;
APARÊNCIAS.

O DETALHAMENTO DE CADA PARÂMETRO DEVE SER VERIFICADO JUNTO AO GED 18968.



ABRIR CAVAS, PREPARAR OS PONTOS DA OBRA.
REALIZAR ATIVIDADES COM LINHA VIVA.

REALIZAR TODAS AS ATIVIDADES SEGUINDO AS NORMAS DE SEGURANÇA.
ESSE PROJETO SÓ PODE SER ALTERADO POR SOLICITAÇÃO DE DI.

 Poste novo a ser instalado (quando indicado em planta)

