


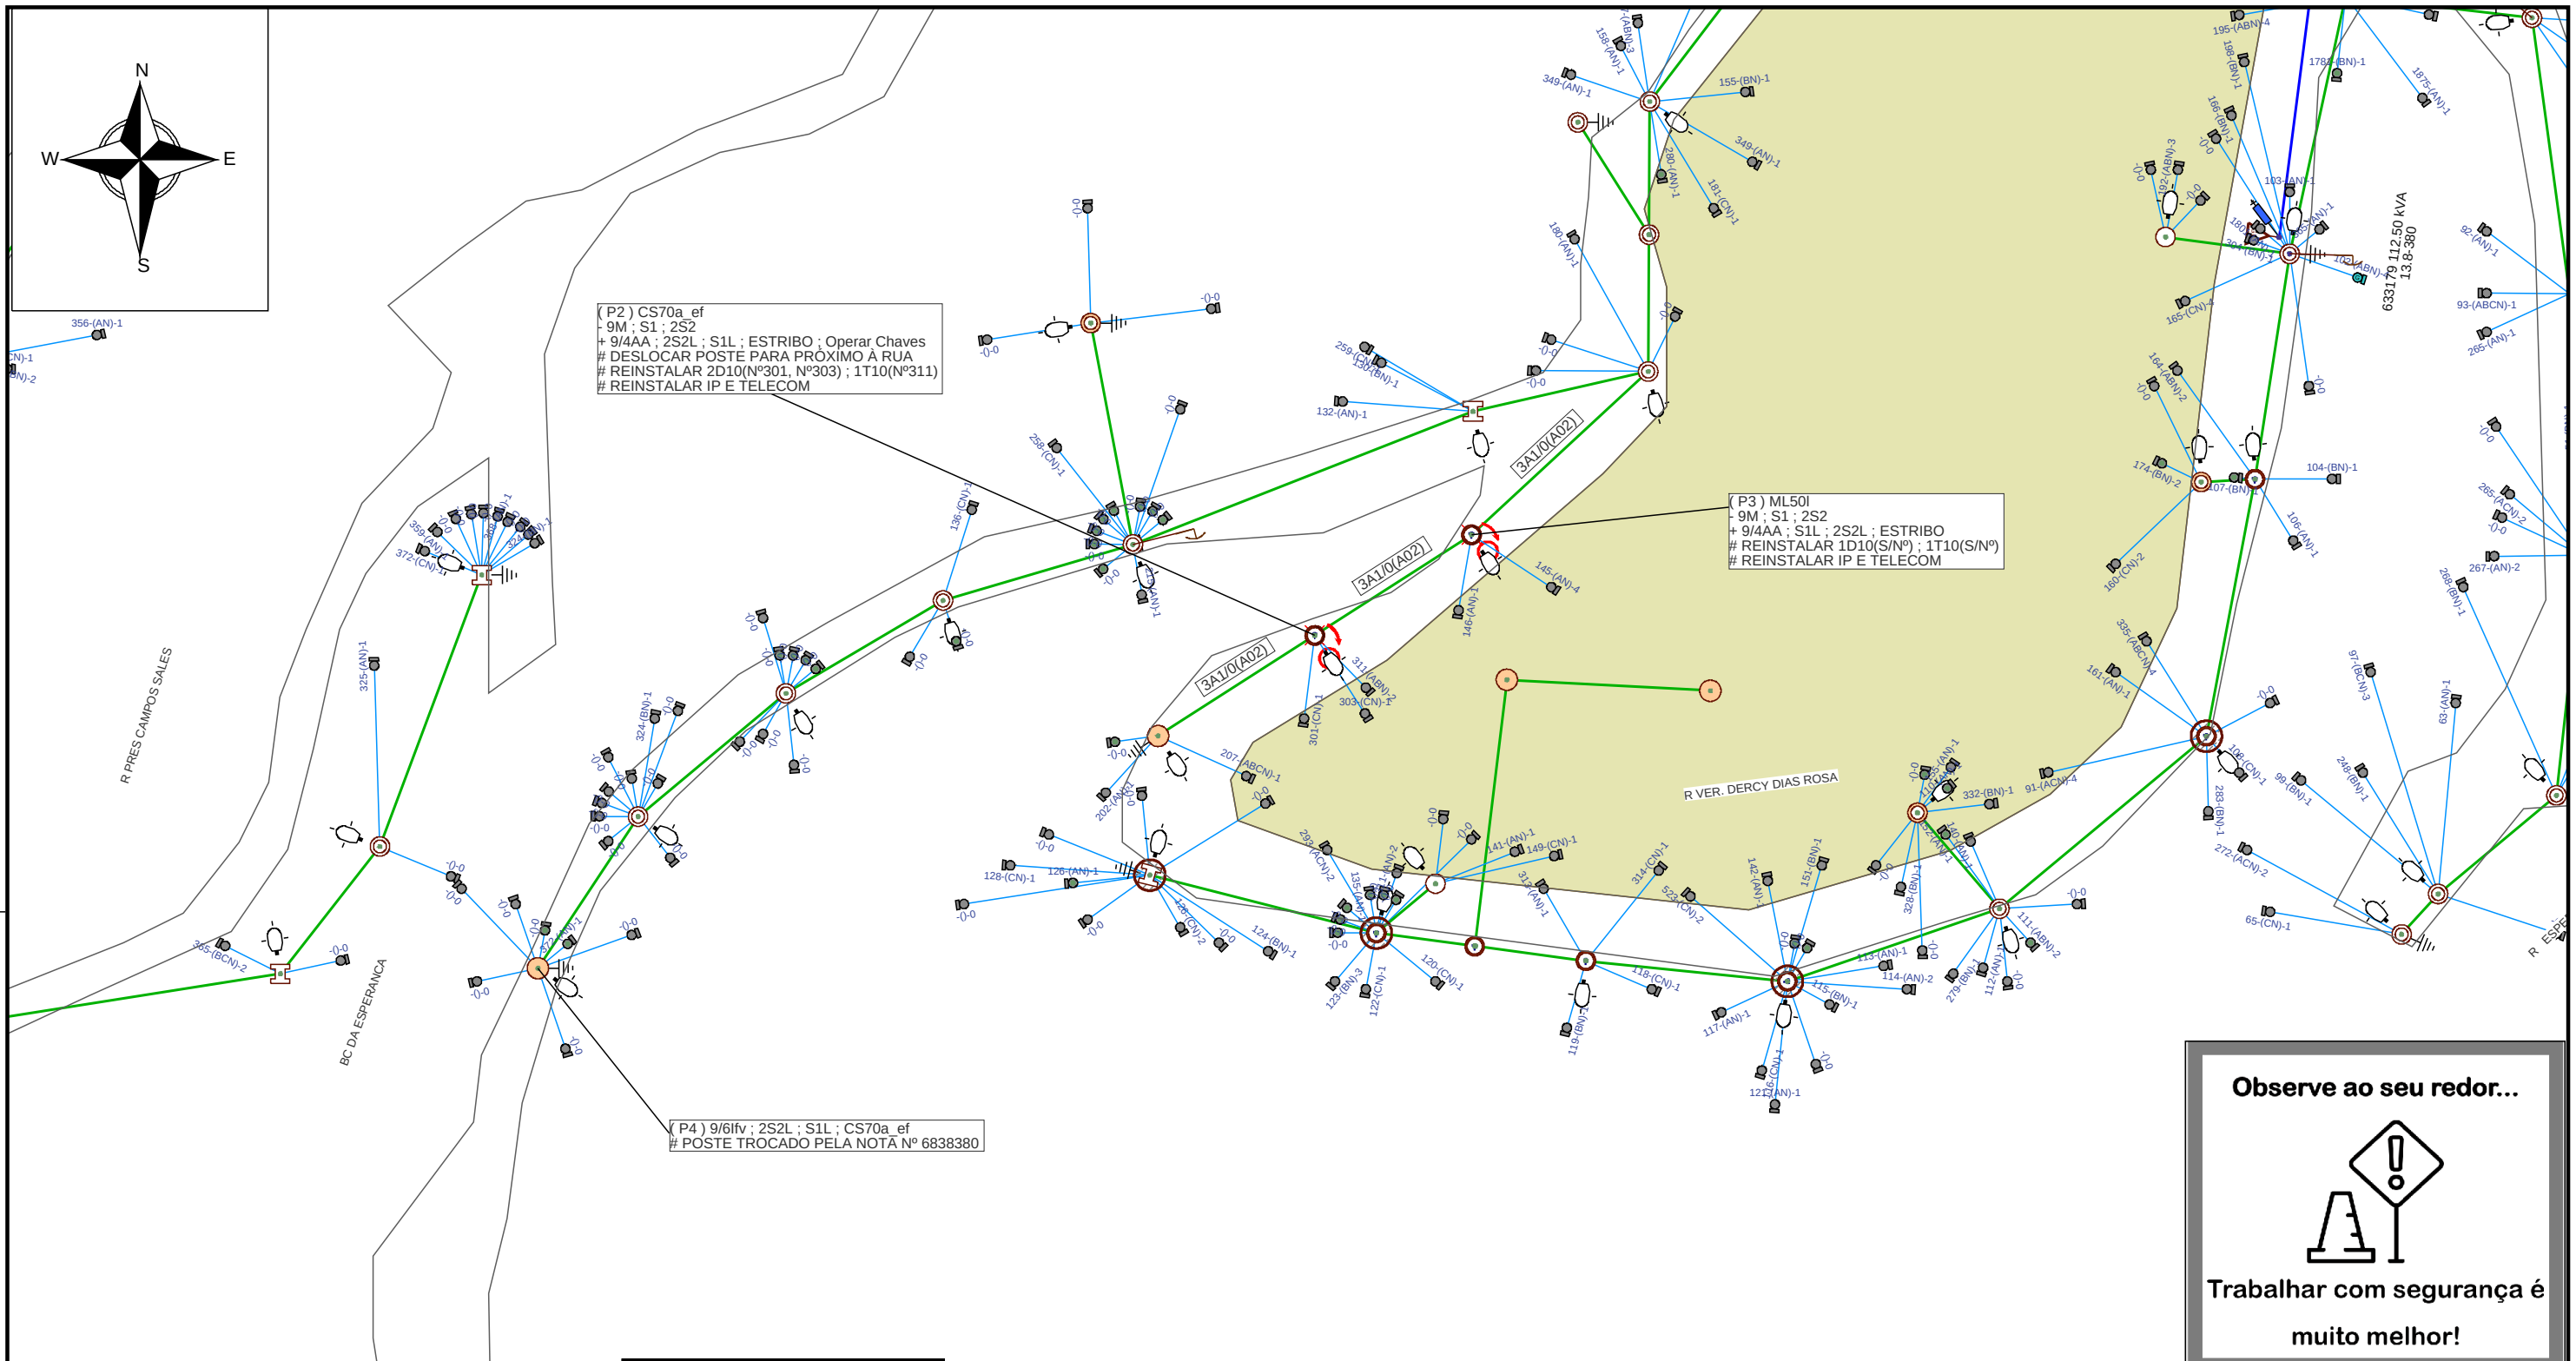

PLANO DE EXECUÇÃO					
EXECUTAR OBRA CONFORME O PROJETO.					

FeedBack Para Fábrica de Projetos

Planeje
Use
Teste
Sinalize
Aterre

Karine Bracht Santos
Gerência de Processos de Obras e Manutenção | DROP
Técnica de Análise e Projetos
CFT: 01798009064

Gerência de Obras e Manutenção
Município: Caxias do Sul

Cliente: RGE SUL DISTRIBUIDORA DE ENERGIA S/A

Obra: Substituição de Poste - TR632668

Endereço: BC DA ESPERANCA - PLANALTO - CAXIAS DO SUL

Responsável Técnico:

Eng. Ederson Paulo Vogel
CREA: RS135794 ART: 10911826

Escala: 1:850
Classe de isolamento: 15kV
Projetista: Karine Bracht

Data: 01/04/2025
AL: CXG24
Projeto: 000007756375

Nota: 000006789081
Folha 1
Levantador: Reinhold Brulinger