


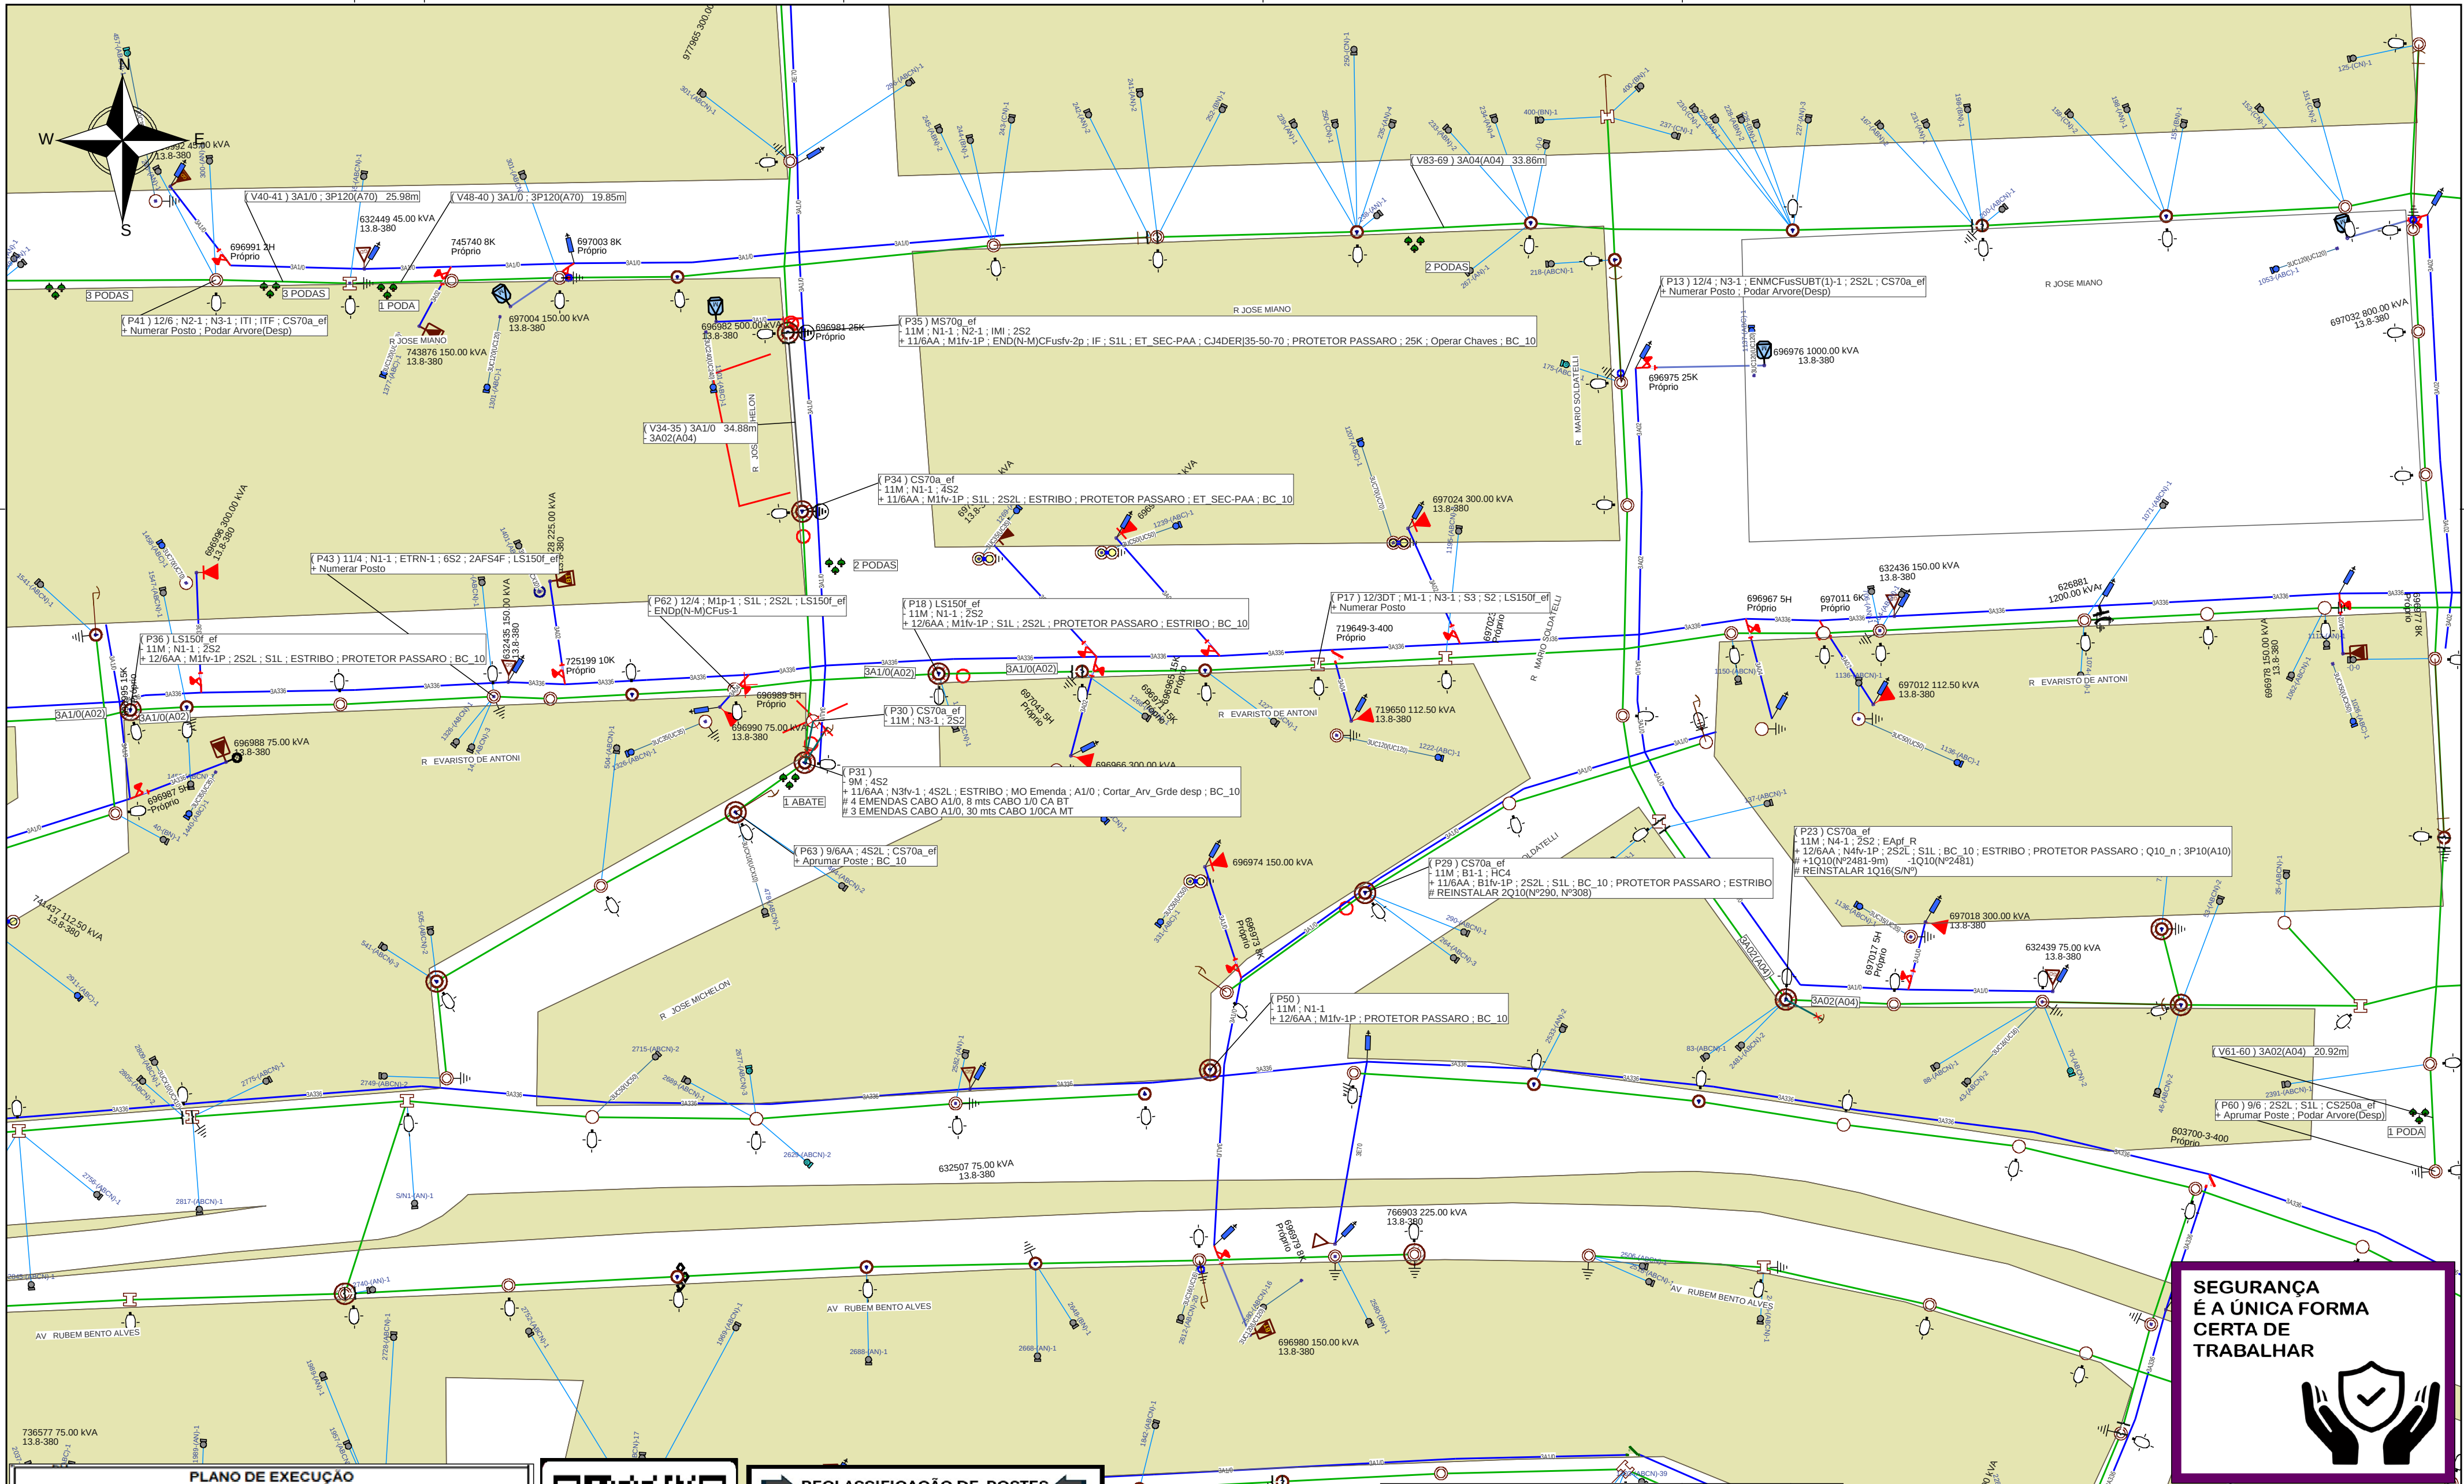

SEGURANÇA
É A ÚNICA FORMA
CERTA DE
TRABALHAR

PLANO DE EXECUÇÃO				
ABRIR CAVAS, PREPARAR OS PONTOS DA OBRA. REALIZAR ATIVIDADES COM LINHA VIVA NA MT.				
REALIZAR TODAS AS ATIVIDADES SEGUINDO AS NORMAS DE SEGURANÇA ESSE PROJETO SÓ PODE SER ALTERADO POR SOLICITAÇÃO DE DI.				
Ação	Equipamento	Número	Clientes	Duração
Abrir	Transformador	632435	21	5
Abrir	Transformador	632439	14	5
Abrir	Transformador	632436	9	5
Linha Viva?				CHI TOTAL
Sim				105
Poste novo a ser instalado (quando indicado em planta)				

FeedBack Para Fábrica de Projetos

RECLASSIFICAÇÃO DE POSTES

OS POSTES DO TIPO TRONCO CÔNICO E FIBRA DE VIDRO CONTIDOS NOS GED'S 1347 E 14606 SEMPRE DEVERÃO SER SUBMETIDOS A AVALIAÇÃO DE RECLASSIFICAÇÃO DOS MESMOS CONFORME O GED 18968

DEVERÃO SEMPRE SER AVALIADOS 3 PARÂMETROS:
CARACTERÍSTICAS TÉCNICAS;
FISSURAS;
APARÊNCIAS.

O DETALHAMENTO DE CADA PARÂMETRO DEVE SER VERIFICADO JUNTO AO GED 18968.

Planeje
Use
Teste
Sinalize
Aterre

Gabriel Vergani
Gerência de Processos de Obras e Manutenção | DROP
Técnico de Análise e Projetos
CFT: 040.224.970-41

Gerência de Obras e Manutenção

Município: Caxias do Sul

Cliente: RGE SUL DISTRIBUIDORA DE ENERGIA S/A

Obra: Caxias do Sul 2025 - Insp Visual de Rede

Endereço: R EVARISTO DE ANTONI, S JOSE, CAXIAS DO SUL

Responsável Técnico:

Eng. Ederson Paulo Vogel
CREA: RS135794

Escala: 1:850
Classe de isolamento: 15kV
Projetista: Gabriel Vergani

Data: 01/04/2025
AL: KCS25
Projeto: 000007756774

Nota: 000006789535
Folha 1
Levantador: Adelar Miguel Ferreira