


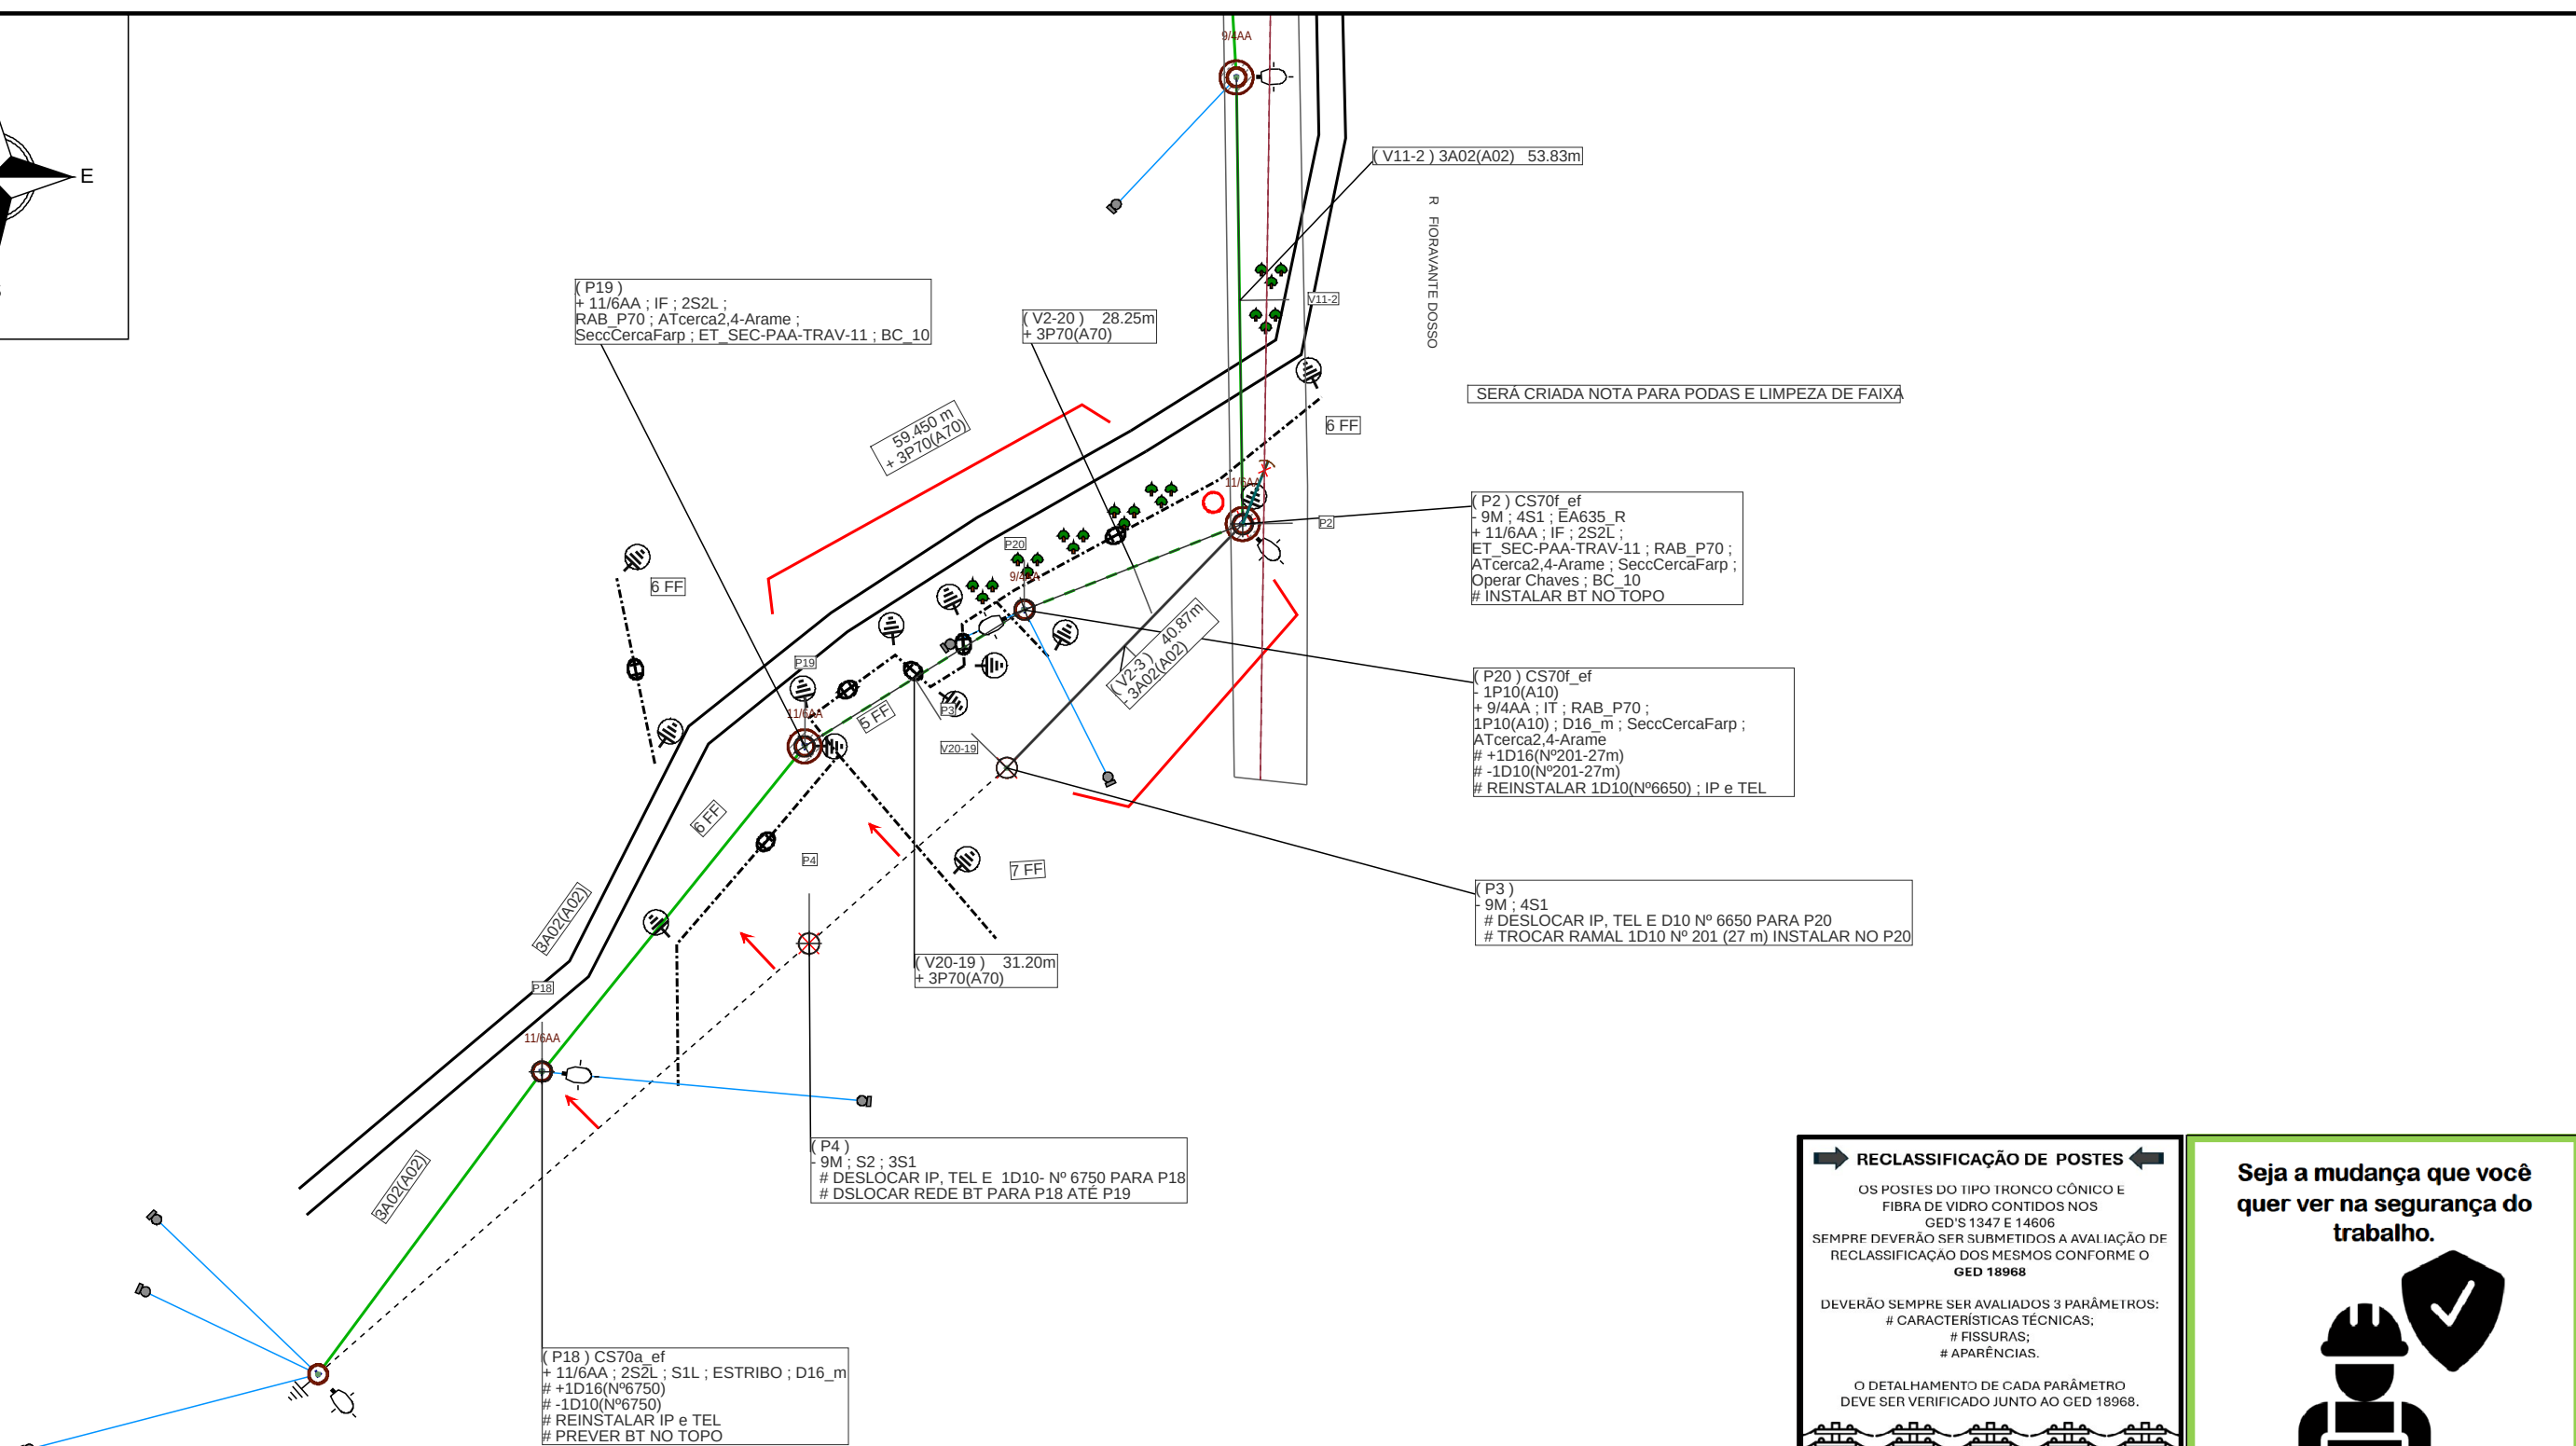


EXECUTAR OBRA SEGUINDO OS PASSOS DE SEGURANÇA
MANOBRAR EQUIPAMENTO ABAIXO PARA SUBSTITUIR POSTES
EXECUTAR CONFORME PROJETO

Ação	Equipamento	Número	Clientes	Duração	CHI
Abrir	Transformador	761065	21	5	105
Linha Viva?		Não	CHI TOTAL		105

☐ Poste novo a ser instalado (quando indicado em planta)



FeedBack Para Fábrica de Projetos

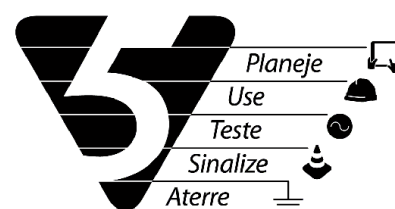

Jailson Cardoso Kessner
Jailson Cardoso Kessner
Gerência de Processos de Obras e Manutenção | DROP
Técnico de Análise e Projetos
CFT: 0138933086



Gerência de Obras e Manutenção

Município: Caxias do Sul

Cliente: RGE SUL DISTRIBUIDORA DE ENERGIA S.A

Obra: Caxias do Sul 2025 - Insp Visual de Rede

Endereço: TR IGREJA Nº 6700

Responsável Técnico:

 Eng. Ederson Paulo Vogel
 CREA: RS135794 ART: 10911826

➡ RECLASSIFICAÇÃO DE POSTES ⬅

OS POSTES DO TIPO TRONCO CÔNICO E
FIBRA DE VIDRO CONTIDOS NOS
GED'S 1347 E 14606
SEMPRE DEVERÃO SER SUBMETIDOS A AVALIAÇÃO DE
RECLASSIFICAÇÃO DOS MESMOS CONFORME O
GED 18968

DEVERÃO SEMPRE SER AVALIADOS 3 PARÂMETROS:
CARACTERÍSTICAS TÉCNICAS;
FISSURAS;
APARÊNCIAS.

O DETALHAMENTO DE CADA PARÂMETRO DEVE SER VERIFICADO JUNTO AO GED 18968.



Seja a mudança que você quer ver na segurança do trabalho.



Responsável Técnico:

Escala: 1:850

Data: 28/04/2025

Nota:	000006824255
-------	--------------

Classe de isolamento:	15kV
-----------------------	------

AL: CXD12

	0000000
	Folha 1

Projeto: JAILSON KESSNER

Projeto: 000007778774

	Levantador: ALESSANDRO S. DE OLIVEIRA
--	--