


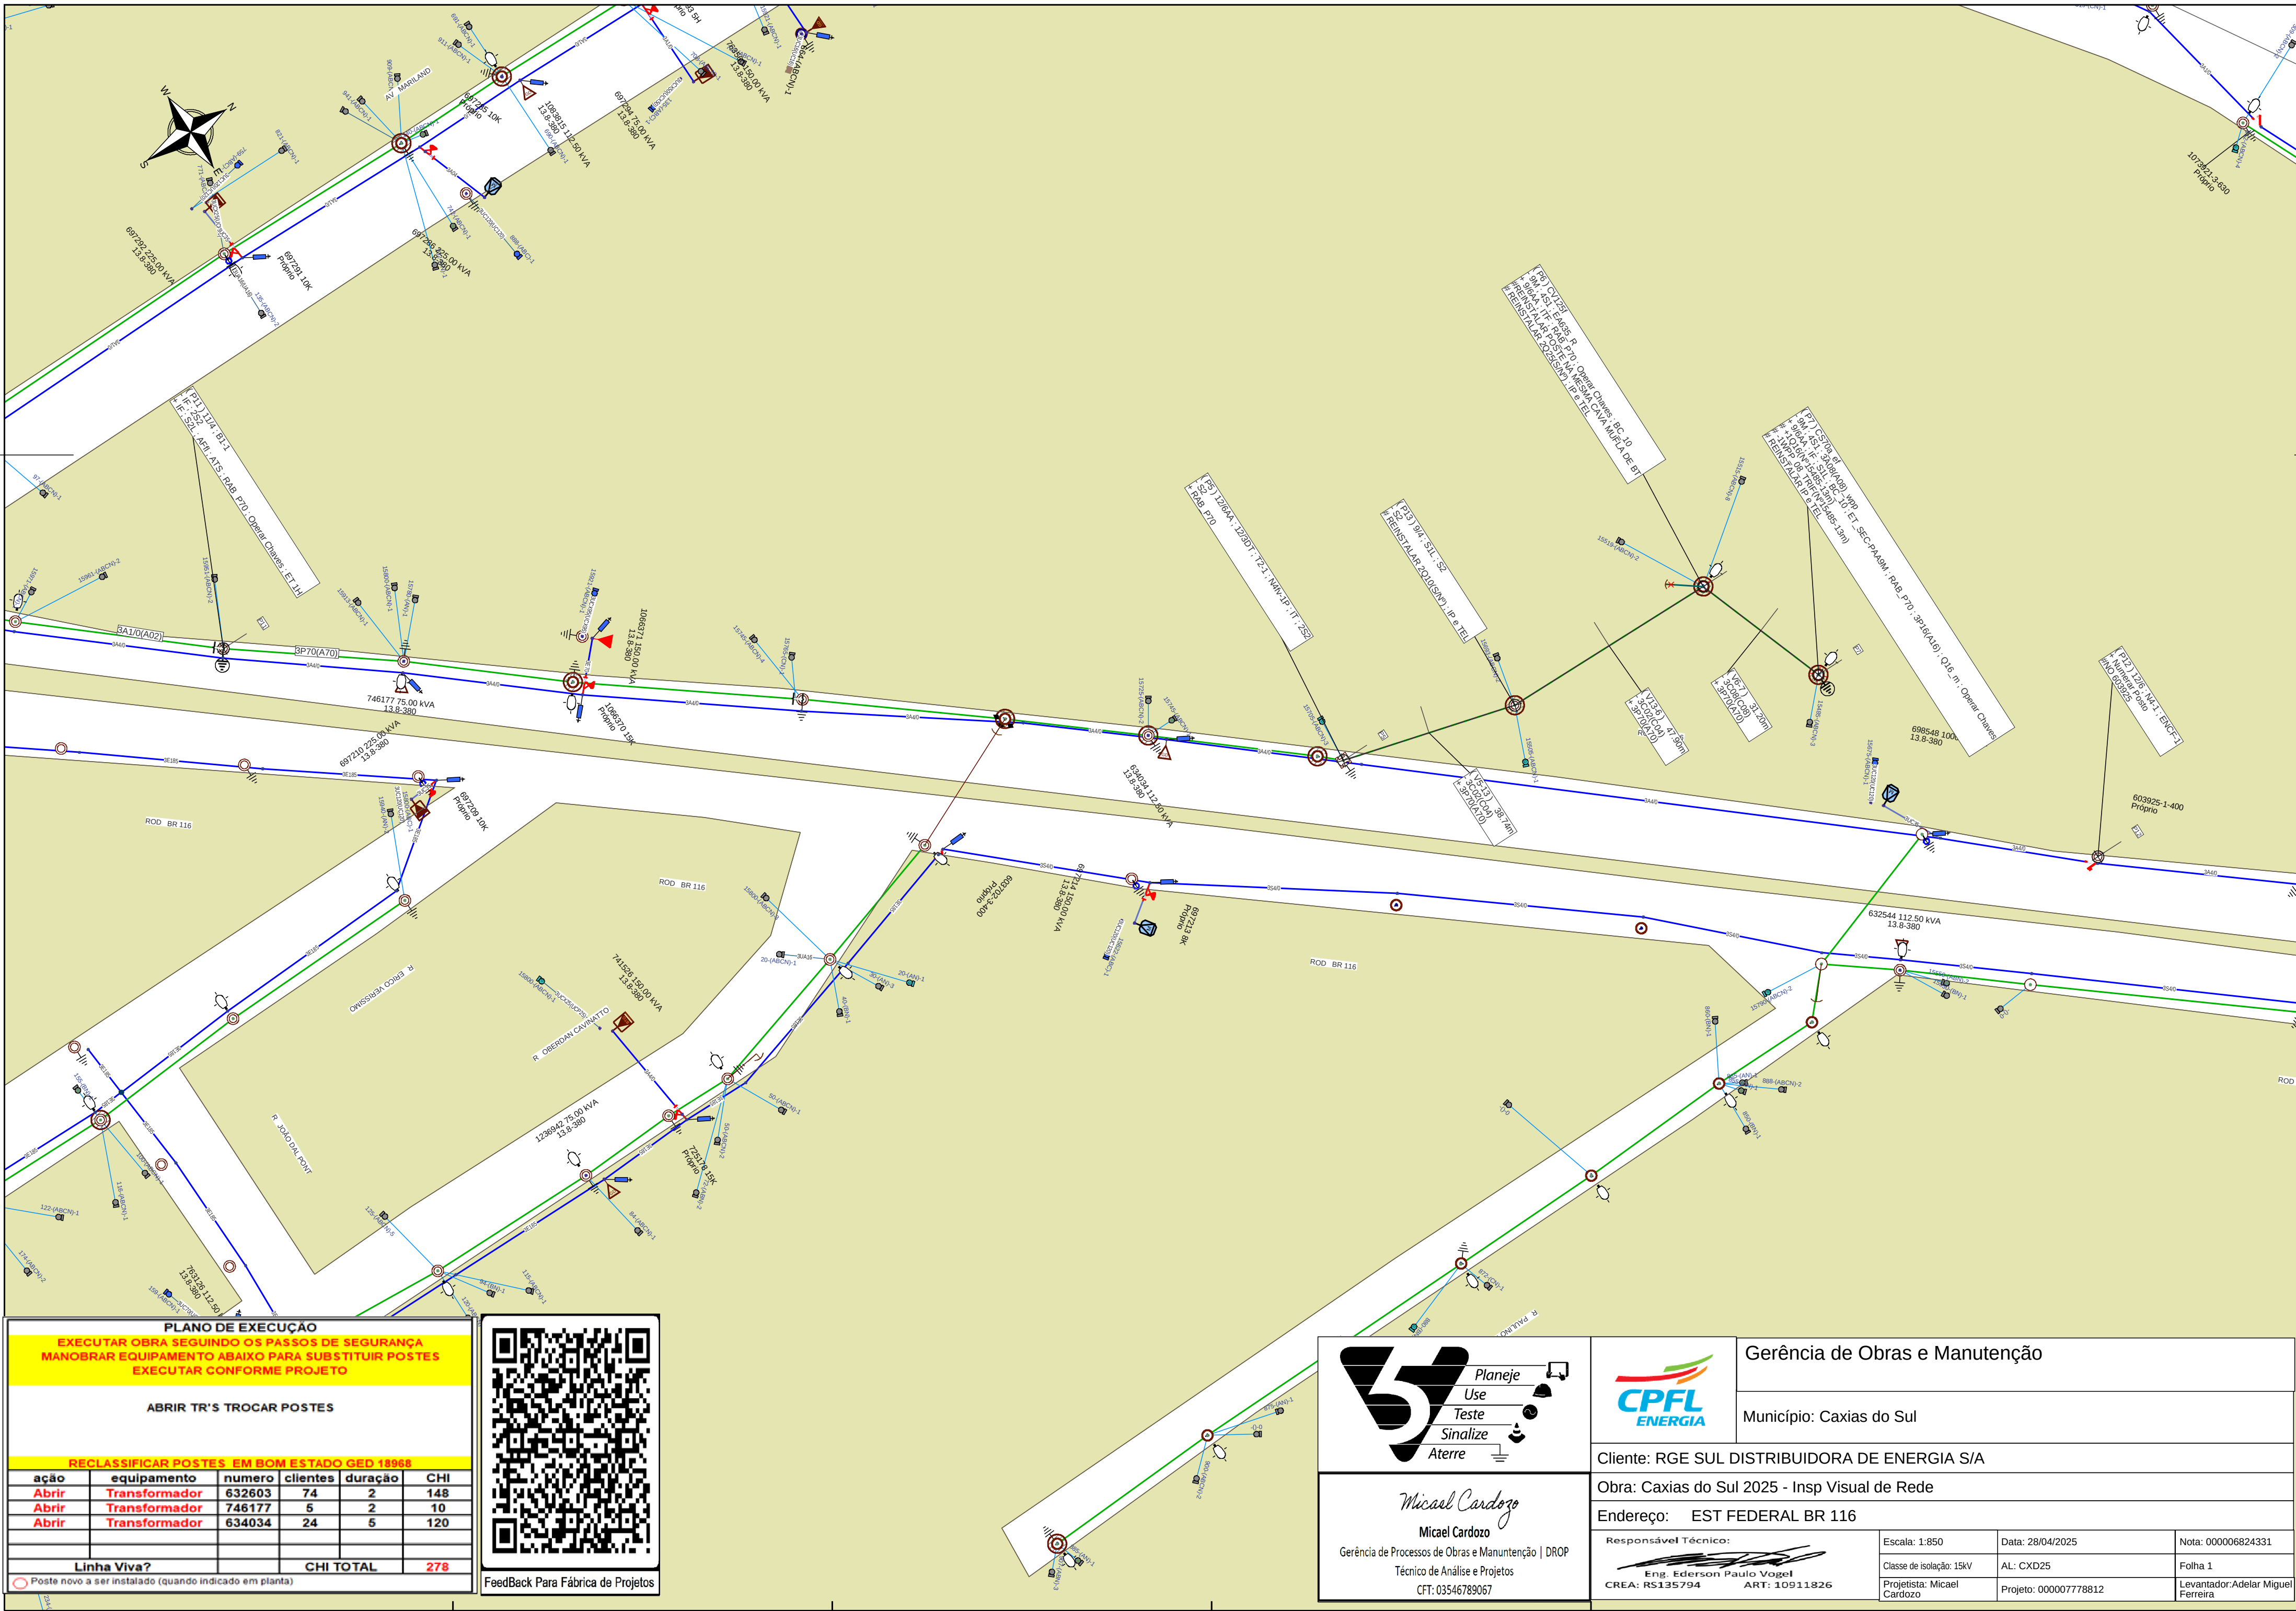

PLANO DE EXECUÇÃO

EXECUTAR OBRA SEGUINDO OS PASSOS DE SEGURANÇA
MANOBRAR EQUIPAMENTO ABAIXO PARA SUBSTITUIR POSTES
EXECUTAR CONFORME PROJETO

ABRIR TR'S TROCAR POSTES

RECLASSIFICAR POSTES EM BOM ESTADO GED 18968					
ação	equipamento	numero	clientes	duração	CHI
Abriu	Transformador	632603	74	2	148
Abriu	Transformador	746177	5	2	10
Abriu	Transformador	634034	24	5	120
Linha Viva?					CHI TOTAL
					278

Poste novo a ser instalado (quando indicado em planta)

FeedBack Para Fábrica de Projetos

Planeje
Use
Teste
Sinalize
Aterre

Micael Cardozo

Micael Cardozo

Gerência de Processos de Obras e Manutenção | DROP

Técnico de Análise e Projetos

CFT: 03546789067

Gerência de Obras e Manutenção

Município: Caxias do Sul

Cliente: RGE SUL DISTRIBUIDORA DE ENERGIA S/A

Obra: Caxias do Sul 2025 - Insp Visual de Rede

Endereço: EST FEDERAL BR 116

Responsável Técnico:	Escala: 1:850	Data: 28/04/2025	Nota: 000006824331
Eng. Ederson Paulo Vogel	Classe de isolamento: 15kV	AL: CXD25	Folha 1
CREA: RS135794	Projetista: Micael Cardozo	Projeto: 000007778812	Levantador: Adelar Miguel Ferreira