


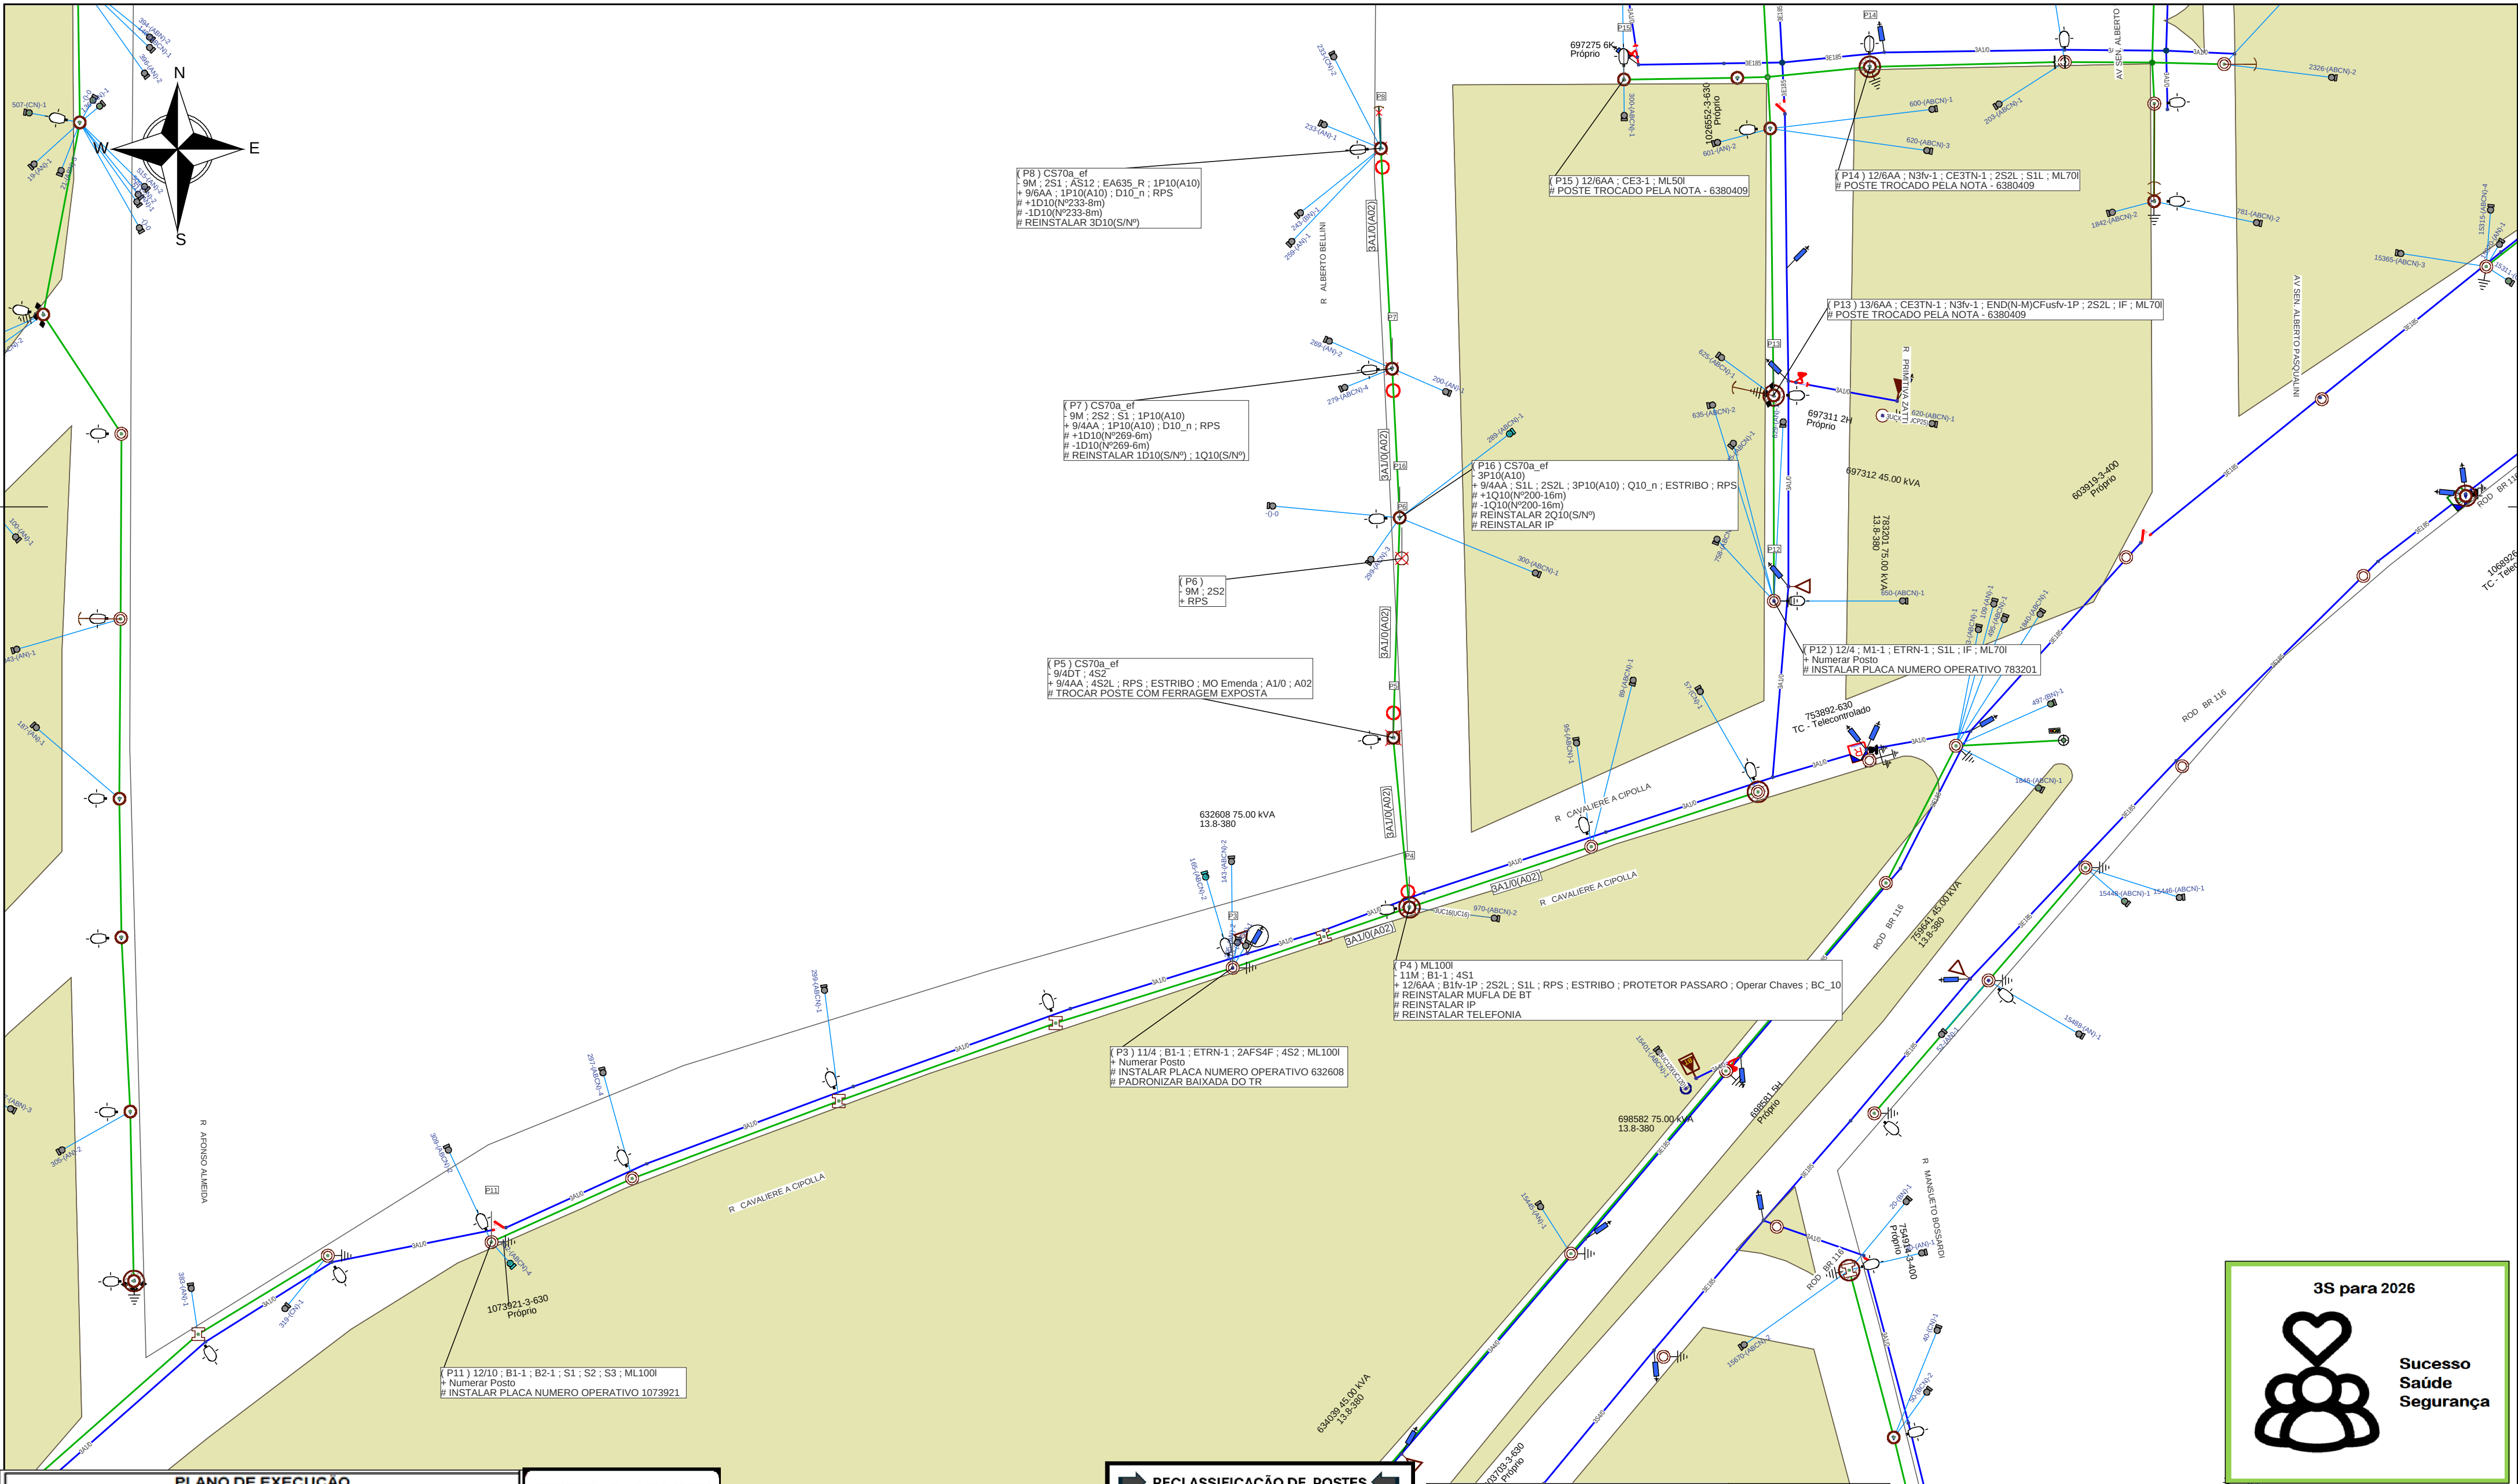

3S para 2026

Sucesso
Saúde
Segurança

PLANO DE EXECUÇÃO					
COM LINHA VIVA TROCAR POSTE P4 COM LINHA MORTA TROCAR POSTES P5, P16, P7, P8 NUMERAR POSTO P11, P3, P12					
Ação	Equipamento	Número	Clientes	Duração	CHI
Abriu	Chave Faca	6824340	39	5	195
					0
					0
					0
					0
					0
Linha Viva?		Não	CHI TOTAL		195
☐ Poste novo a ser instalado (quando indicado em planta)					

FeedBack Para Fábrica de Projetos

RECLASSIFICAÇÃO DE POSTES

OS POSTES DO TIPO TRONCO CÔNICO E FIBRA DE VIDRO CONTIDOS NOS GED'S 1347 E 14606 SEMPRE DEVERÃO SER SUBMETIDOS A AVALIAÇÃO DE RECLASSIFICAÇÃO DOS MESMOS CONFORME O GED 18968

DEVERÃO SEMPRE SER AVALIADOS 3 PARÂMETROS:
CARACTERÍSTICAS TÉCNICAS;
FISSURAS;
APARÊNCIAS.

O DETALHAMENTO DE CADA PARÂMETRO DEVE SER VERIFICADO JUNTO AO GED 18968.

Use
Teste
Sinalize
Aterre

Dionathan C. Hernandez
Gerência de Processos de Obras e Manutenção | DROP
Técnico de Análise e Projetos
CFT: 03466944007

Gerência de Obras e Manutenção

Município: Caxias do Sul

Cliente: RGE SUL DISTRIBUIDORA DE ENERGIA S/A

Obra: Caxias do Sul 2025 - Insp Visual de Rede

Endereço: R CAVALIERE AMBROGIO CIPOLLA 970 - MARILAND - CAXIAS DO SUL

Responsável Técnico:

Eng. Ederson Paulo Vogel
CREA: RS135794 ART: 10911826

Escala: 1:850
Classe de Isolação: 15kV
Projetista: DIONATHAN

Data: 28/04/2025
AL: CXD25
Projeto: 000007778911

Nota: 000006824340
Folha 1
RICARDO QUEVEDO DE ALBUQUERQUE