



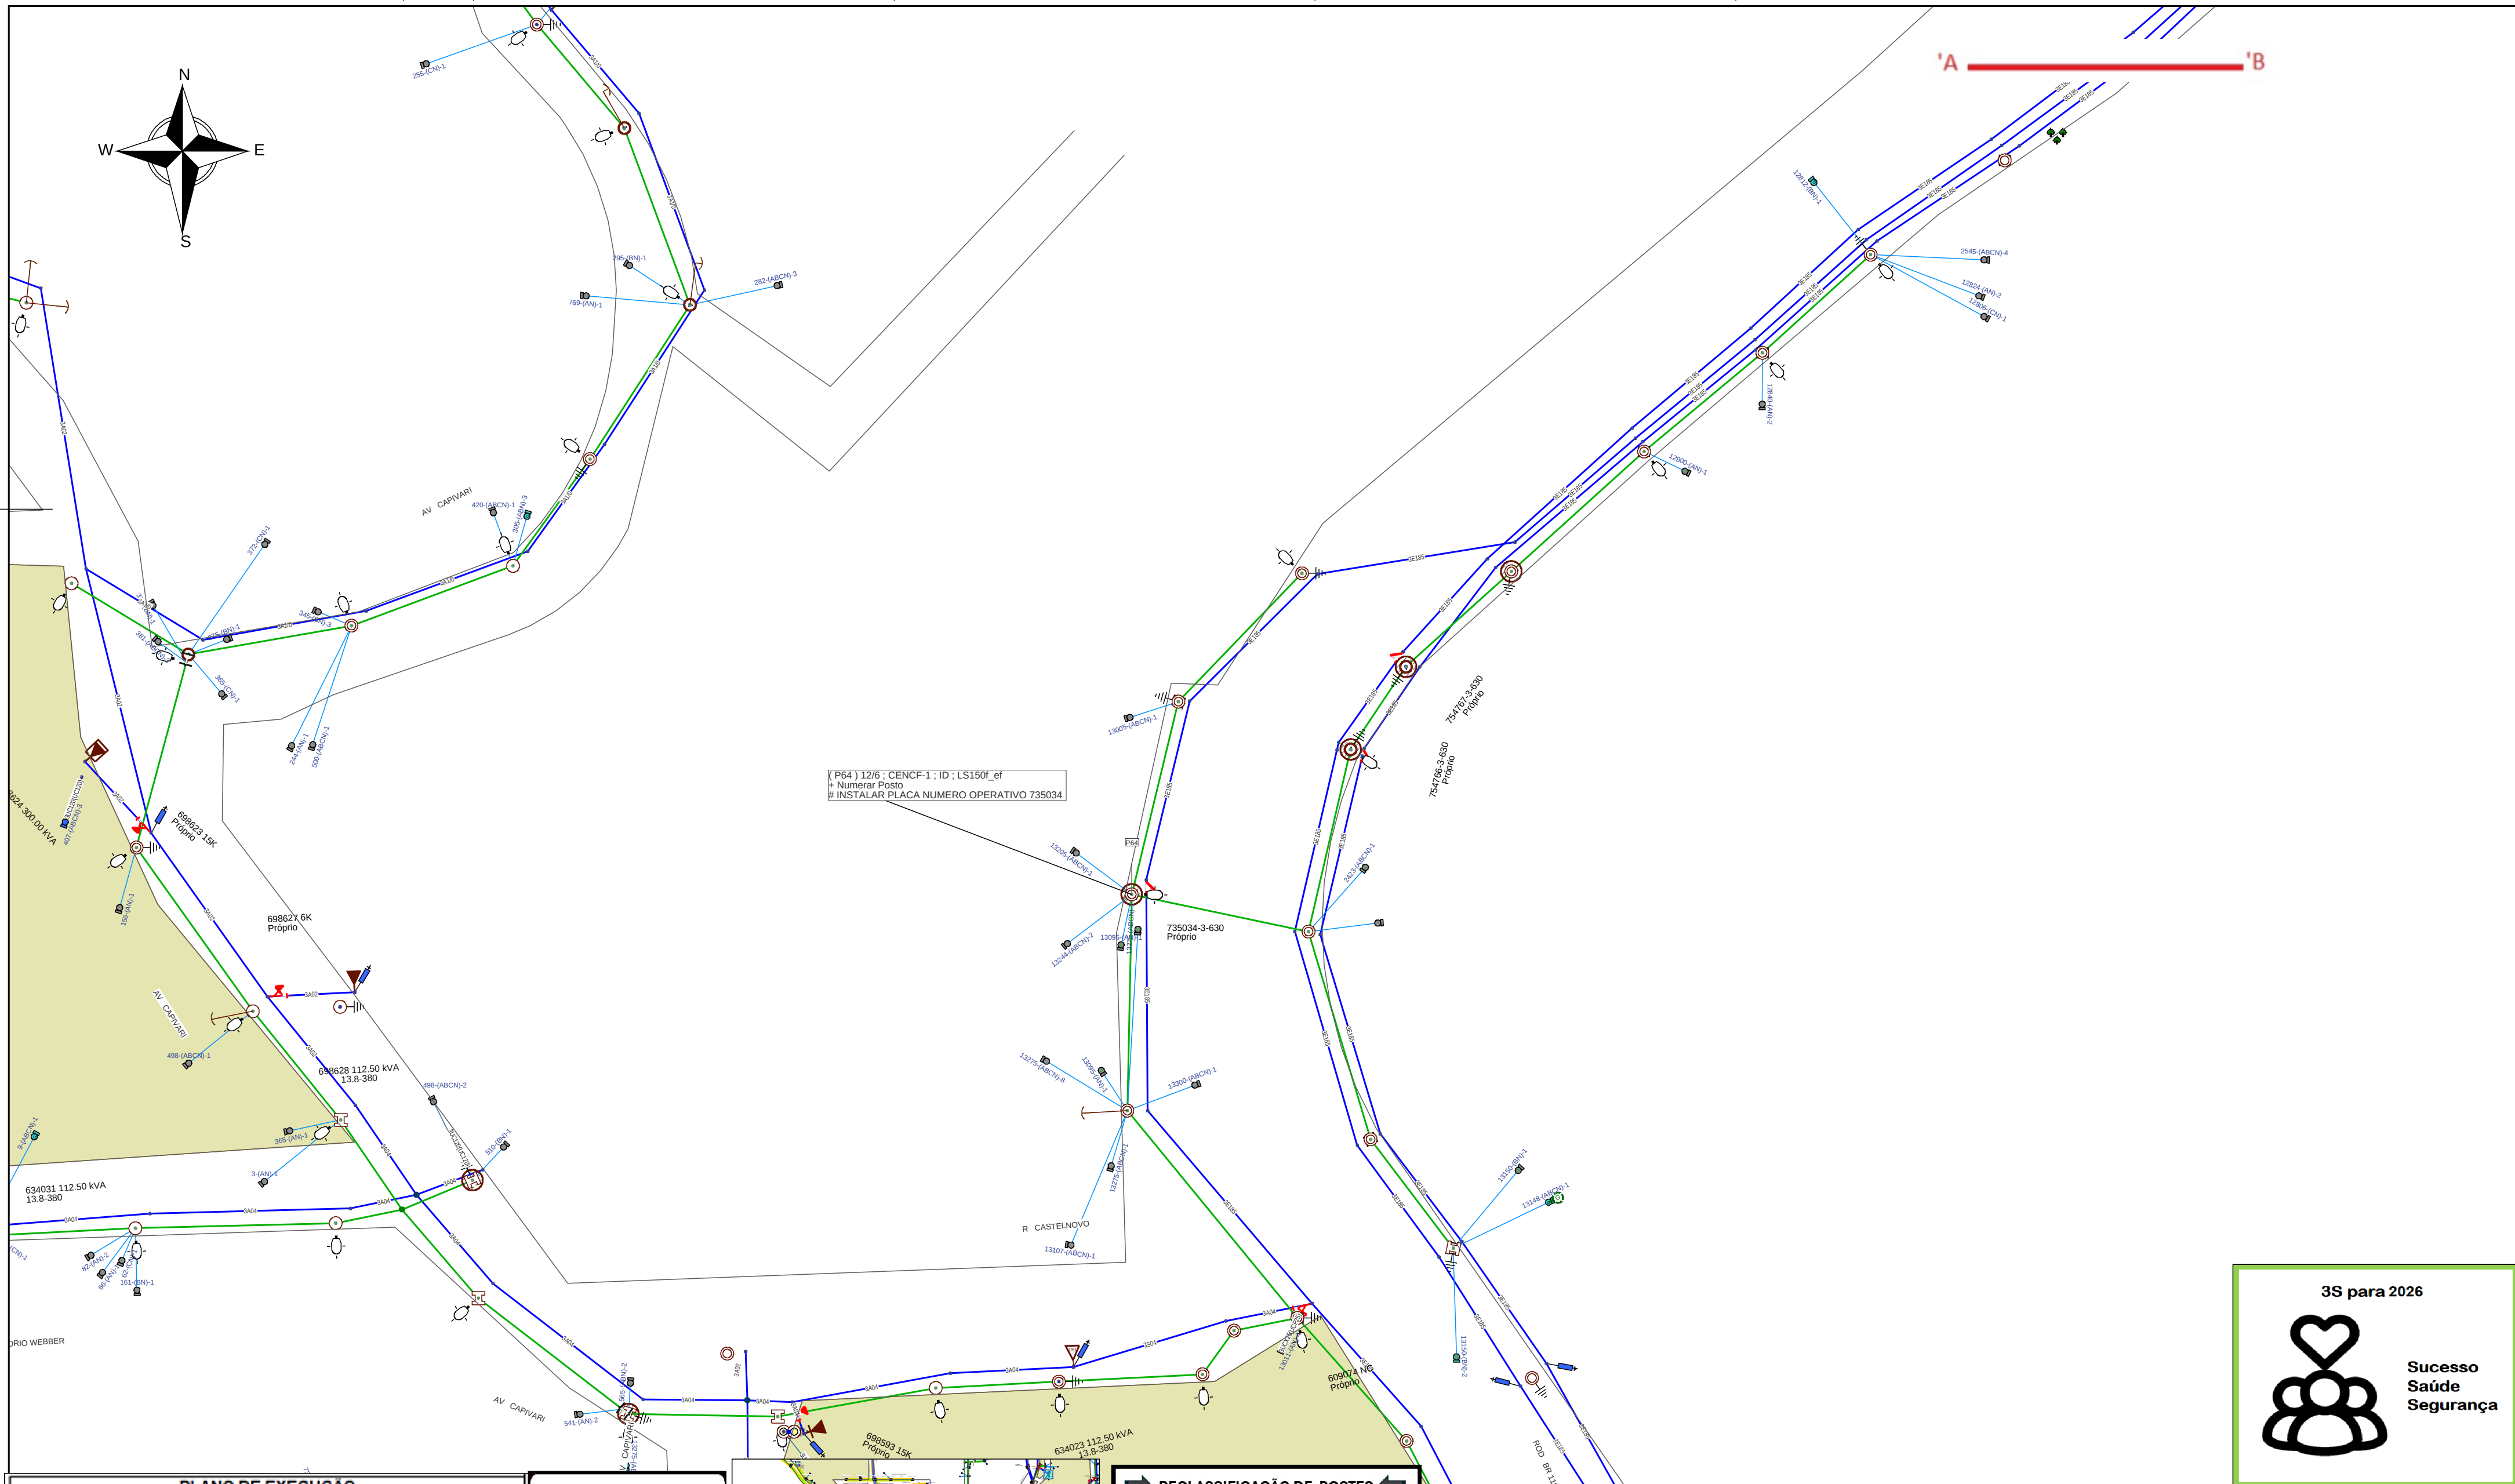

PLANO DE EXECUÇÃO					
EXECUTAR EM CONJUNTO NOTA FILHA - 7381600					
COM LINHA VIVA TROCAR POSTE - P32					
COM LINHA MORTA TROCAR POSTES - P8, P9, P10					
NUMERAR POSTO P29, P28, P34, P64					
APRUMAR POSTE P5					
REMOVER POSTE TELEFONIA P63, P62					
Ação	Equipamento	Número	Clientes	Duração	CHI
Abriu	Transformador	634022	114	5	570
					0
					0
					0
					0
					0
Linha Viva?		Sim	CHI TOTAL		570

FeedBack Para Fábrica de Projetos

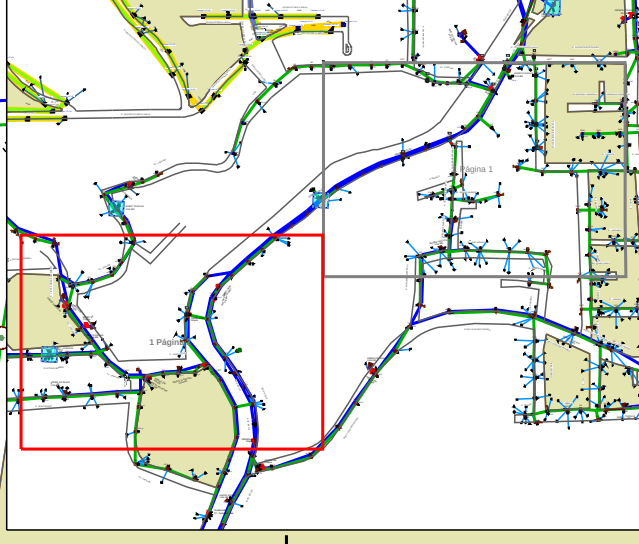

RECLASSIFICAÇÃO DE POSTES

OS POSTES DO TIPO TRONCO CÔNICO E FIBRA DE VIDRO CONTIDOS NOS GED'S 1347 E 14606 SEMPRE DEVERÃO SER SUBMETIDOS A AVALIAÇÃO DE RECLASSIFICAÇÃO DOS MESMOS CONFORME O GED 18968

DEVERÃO SEMPRE SER AVALIADOS 3 PARÂMETROS:

- # CARACTERÍSTICAS TÉCNICAS;
- # FISSURAS;
- # APARÊNCIAS.

O DETALHAMENTO DE CADA PARÂMETRO DEVE SER VERIFICADO JUNTO AO GED 18968.

Dionathan C. Hernandez
Gerência de Processos de Obras e Manutenção | DROP
Técnico de Análise e Projetos
CFT: 03466944007

Gerência de Obras e Manutenção

Município: Caxias do Sul

Cliente: RGE SUL DISTRIBUIDORA DE ENERGIA S/A

Obra: Caxias do Sul 2025 - Insp Visual de Rede

Endereço: R LUIZ CECONI 147 - S CRISTOVAO - CAXIAS DO SUL

Responsável Técnico:	Escala: 1:850	Data: 28/04/2025	Nota: 000006824347
Eng. Ederson Paulo Vogel CREA: RS135794 ART: 10911826	Classe de isolamento: 15KV	AL: CXD23	Folha 2
	Projetista: DIONATHAN	Projeto: 00000778854	REINHOLDO BRULINGER