


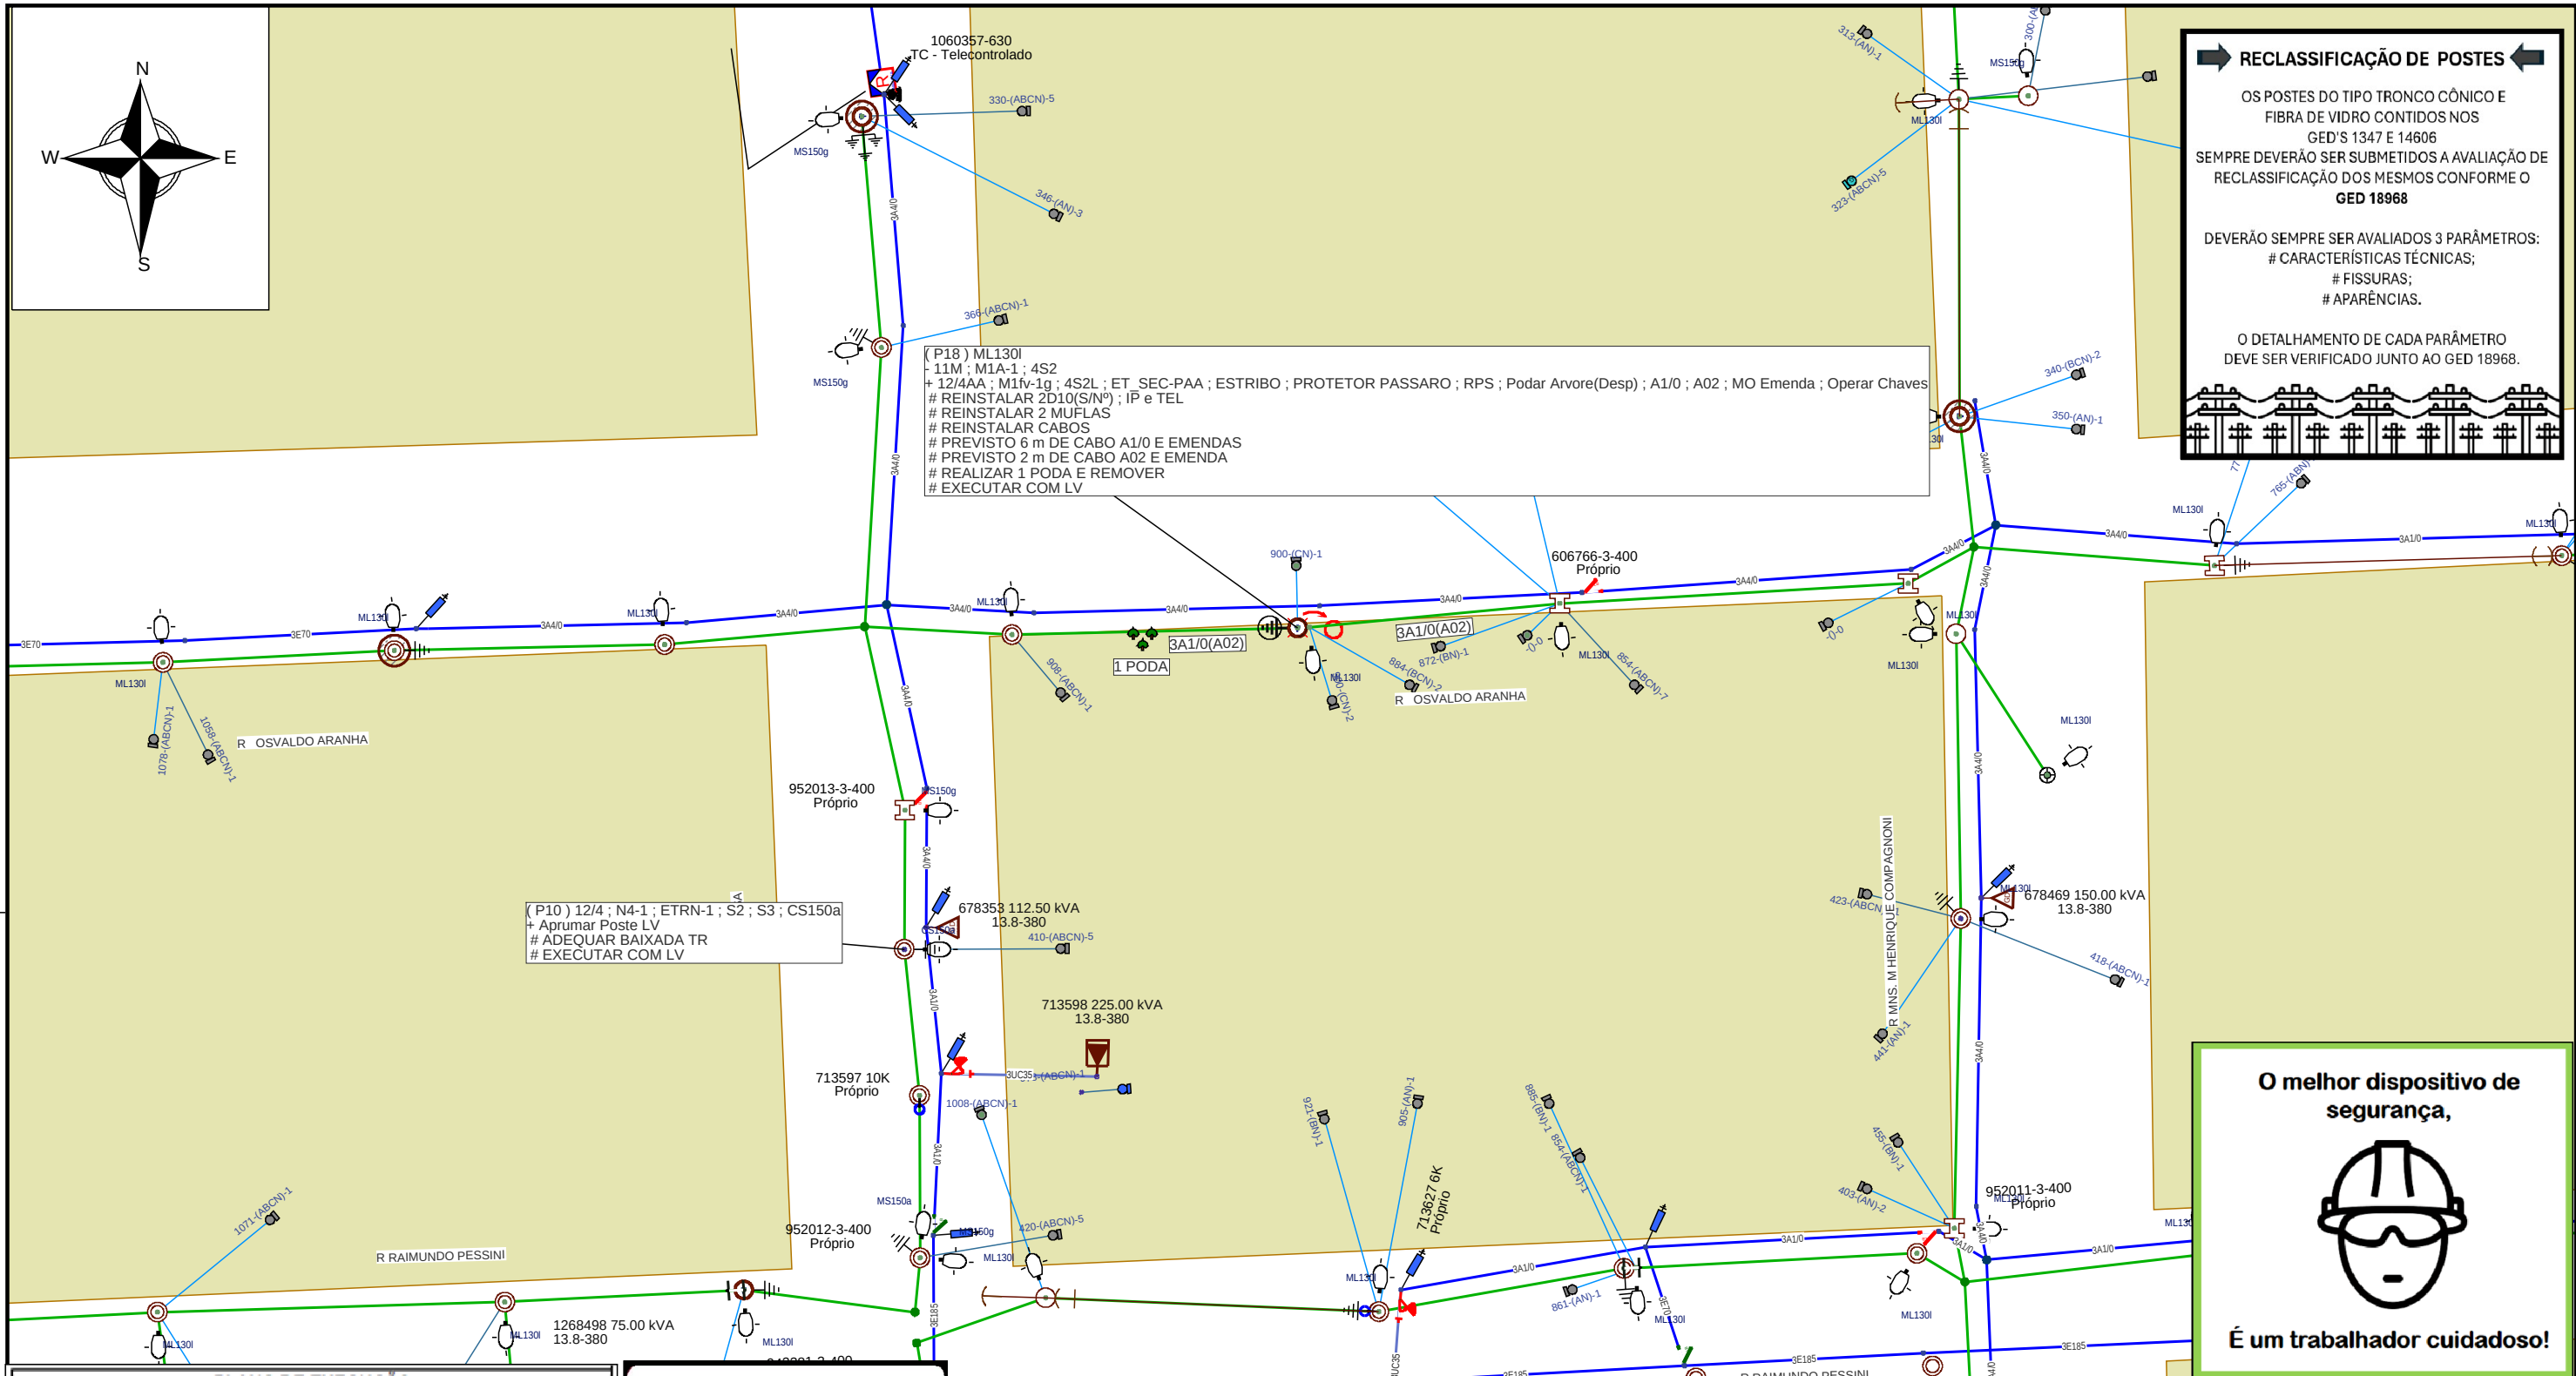

PLANO DE EXECUÇÃO					
Substituir os postes indicados.					
Executar as atividades em conjunto a nota 6868902.					
Executar as atividades com segurança, respeitando as orientações e normas vigentes.					
Obs: executar os pontos P10 e P18 com equipe de linha viva.					
Ação	Equipamento	Número	Clientes	Duração	CHI
Desligar	Transformador	678353	27	5	135
Desligar	Transformador	678469	67	5	335
					0
					0
					0
Linha Viva?	Sim	CHI TOTAL			470
Poste novo a ser instalado (quando indicado em planta)					

FeedBack Para Fábrica de Projetos

Planeje
Use
Teste
Sinalize
Aterre

Milena Bueno Ferreira

Gerência de Processos de Obras e Manutenção | DROP

Técnico de Análise e Projetos

CFT: 04355870057

Gerência de Obras e Manutenção

Município: São Marcos

Cliente: RGE SUL DISTRIBUIDORA DE ENERGIA S.A.

Obra: Caxias do Sul 2025 - Insp Visual de Rede

Endereço: R OSVALDO ARANHA 901, CENTRO SAO MARCOS - RS

Responsável Técnico: Eng. Ederson Paulo Vogel
CREA: RS135794 ART: 10911826

Escala: 1:850
Classe de isolamento: 15kV
Projetista: Milena Ferreira

Data: 01/06/2025
AL: SMC11
Projeto: 000007806606

Nota: 000006867310
Folha 1
Levantador: RICARDO DE ALBUQUERQUE