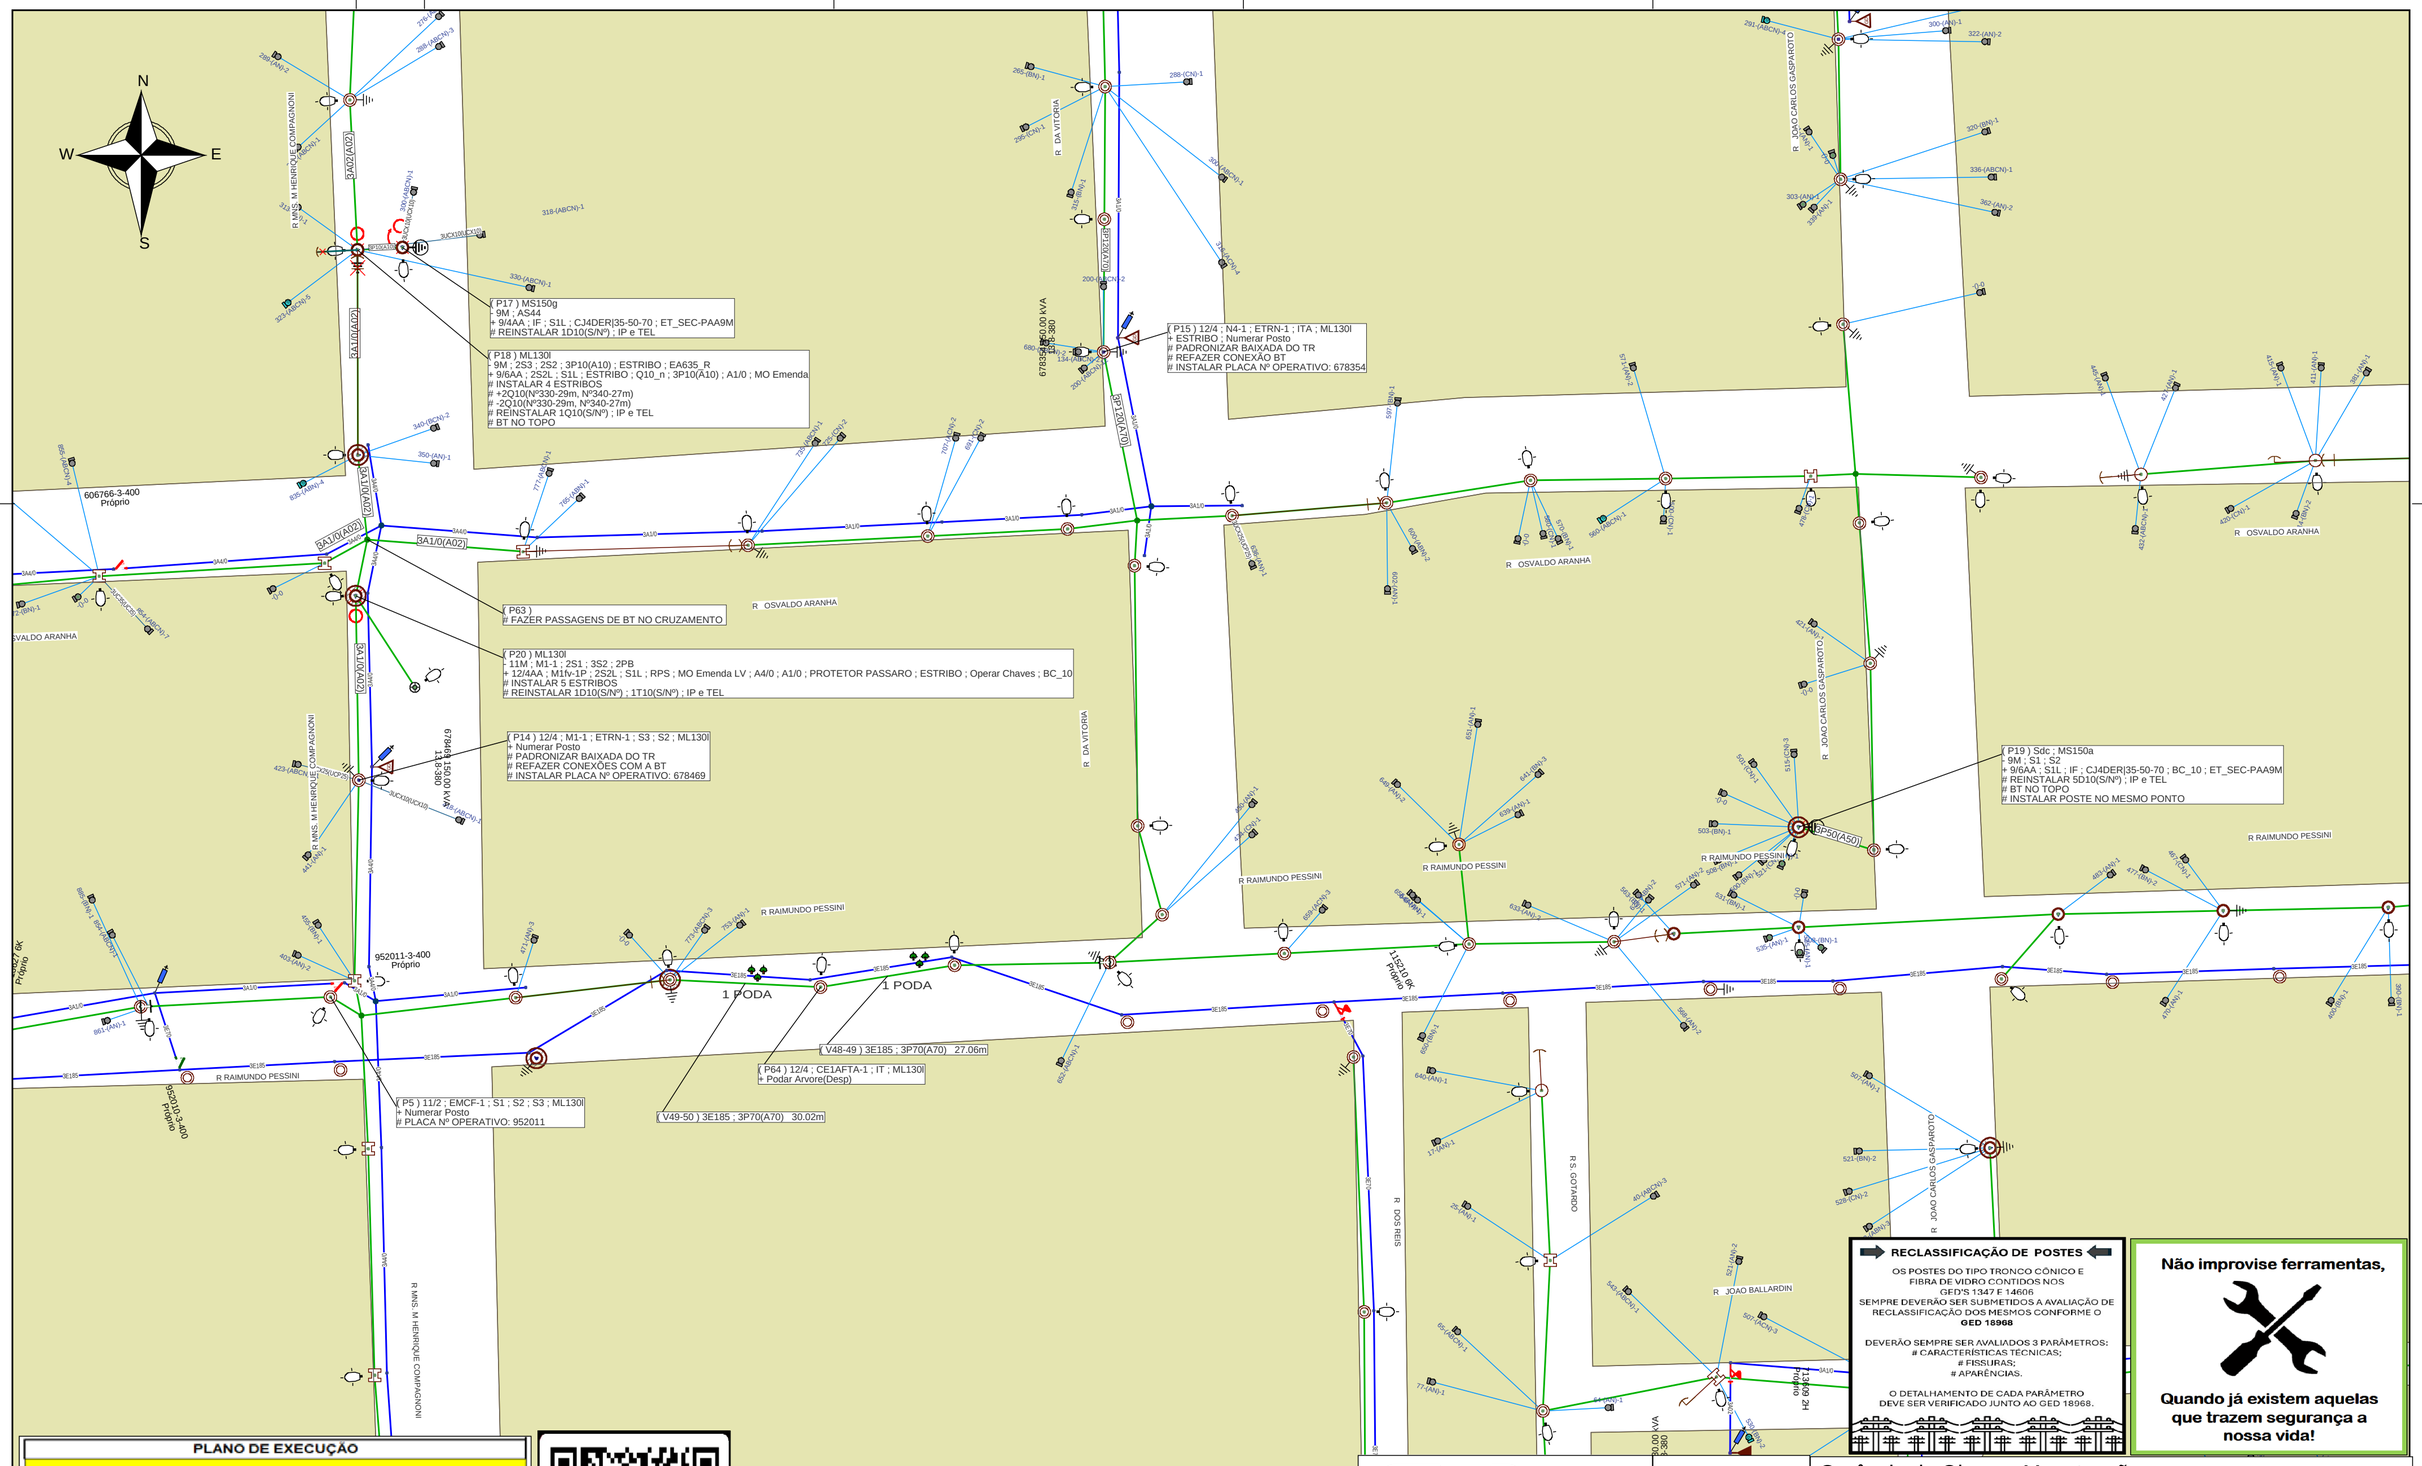

PLANO DE EXECUÇÃO

TROCAR POSTES EXECUTANDO A MT COM LINHA VIVA SEGUINDO PROCEDIMENTOS OPERACIONAIS PADRÃO E NORMAS VIGENTES

Ação	Equipamento	Número	Clientes	Duração	CHI
Abrir	Transformador	678469	67	4	268
Abrir	Transformador	678354	85	4	340
Linha Viva?			CHI TOTAL		608

Poste novo a ser instalado (quando indicado em planta)

FeedBack Para Fábrica de Projetos

Planeje
Use
Teste
Sinalize
Aterre

Breno Ardenghy
Breno Ardenghy Da Silva
Gerência de Processos de Obras e Manuntenção | DROP
Técnico de Análise e Projetos
CFT: 03188101074

CPFL ENERGIA

Gerência de Obras e Manutenção

Município: São Marcos

Cliente: RGE SUL DISTRIBUIDORA DE ENERGIA S.A

Obra: Caxias do Sul 2025 - Insp Visual de Rede

Endereço: R M HENRIQUE COMPAGNONI 289 CENTRO SAO MARCOS

Responsável Técnico:
Eng. Ederson Paulo Vogel
CREA: RS135794 ART: 10911826

Escala: 1:850	Data: 01/06/2025	Nota: 000006868902
Classe de isolação: 15kV	AL: SMC11	Folha 1
Projetista: BRENO ARDENHY	Projeto: 000007807321	Levantador: RICARDO QUEV ALBUQUERQUE