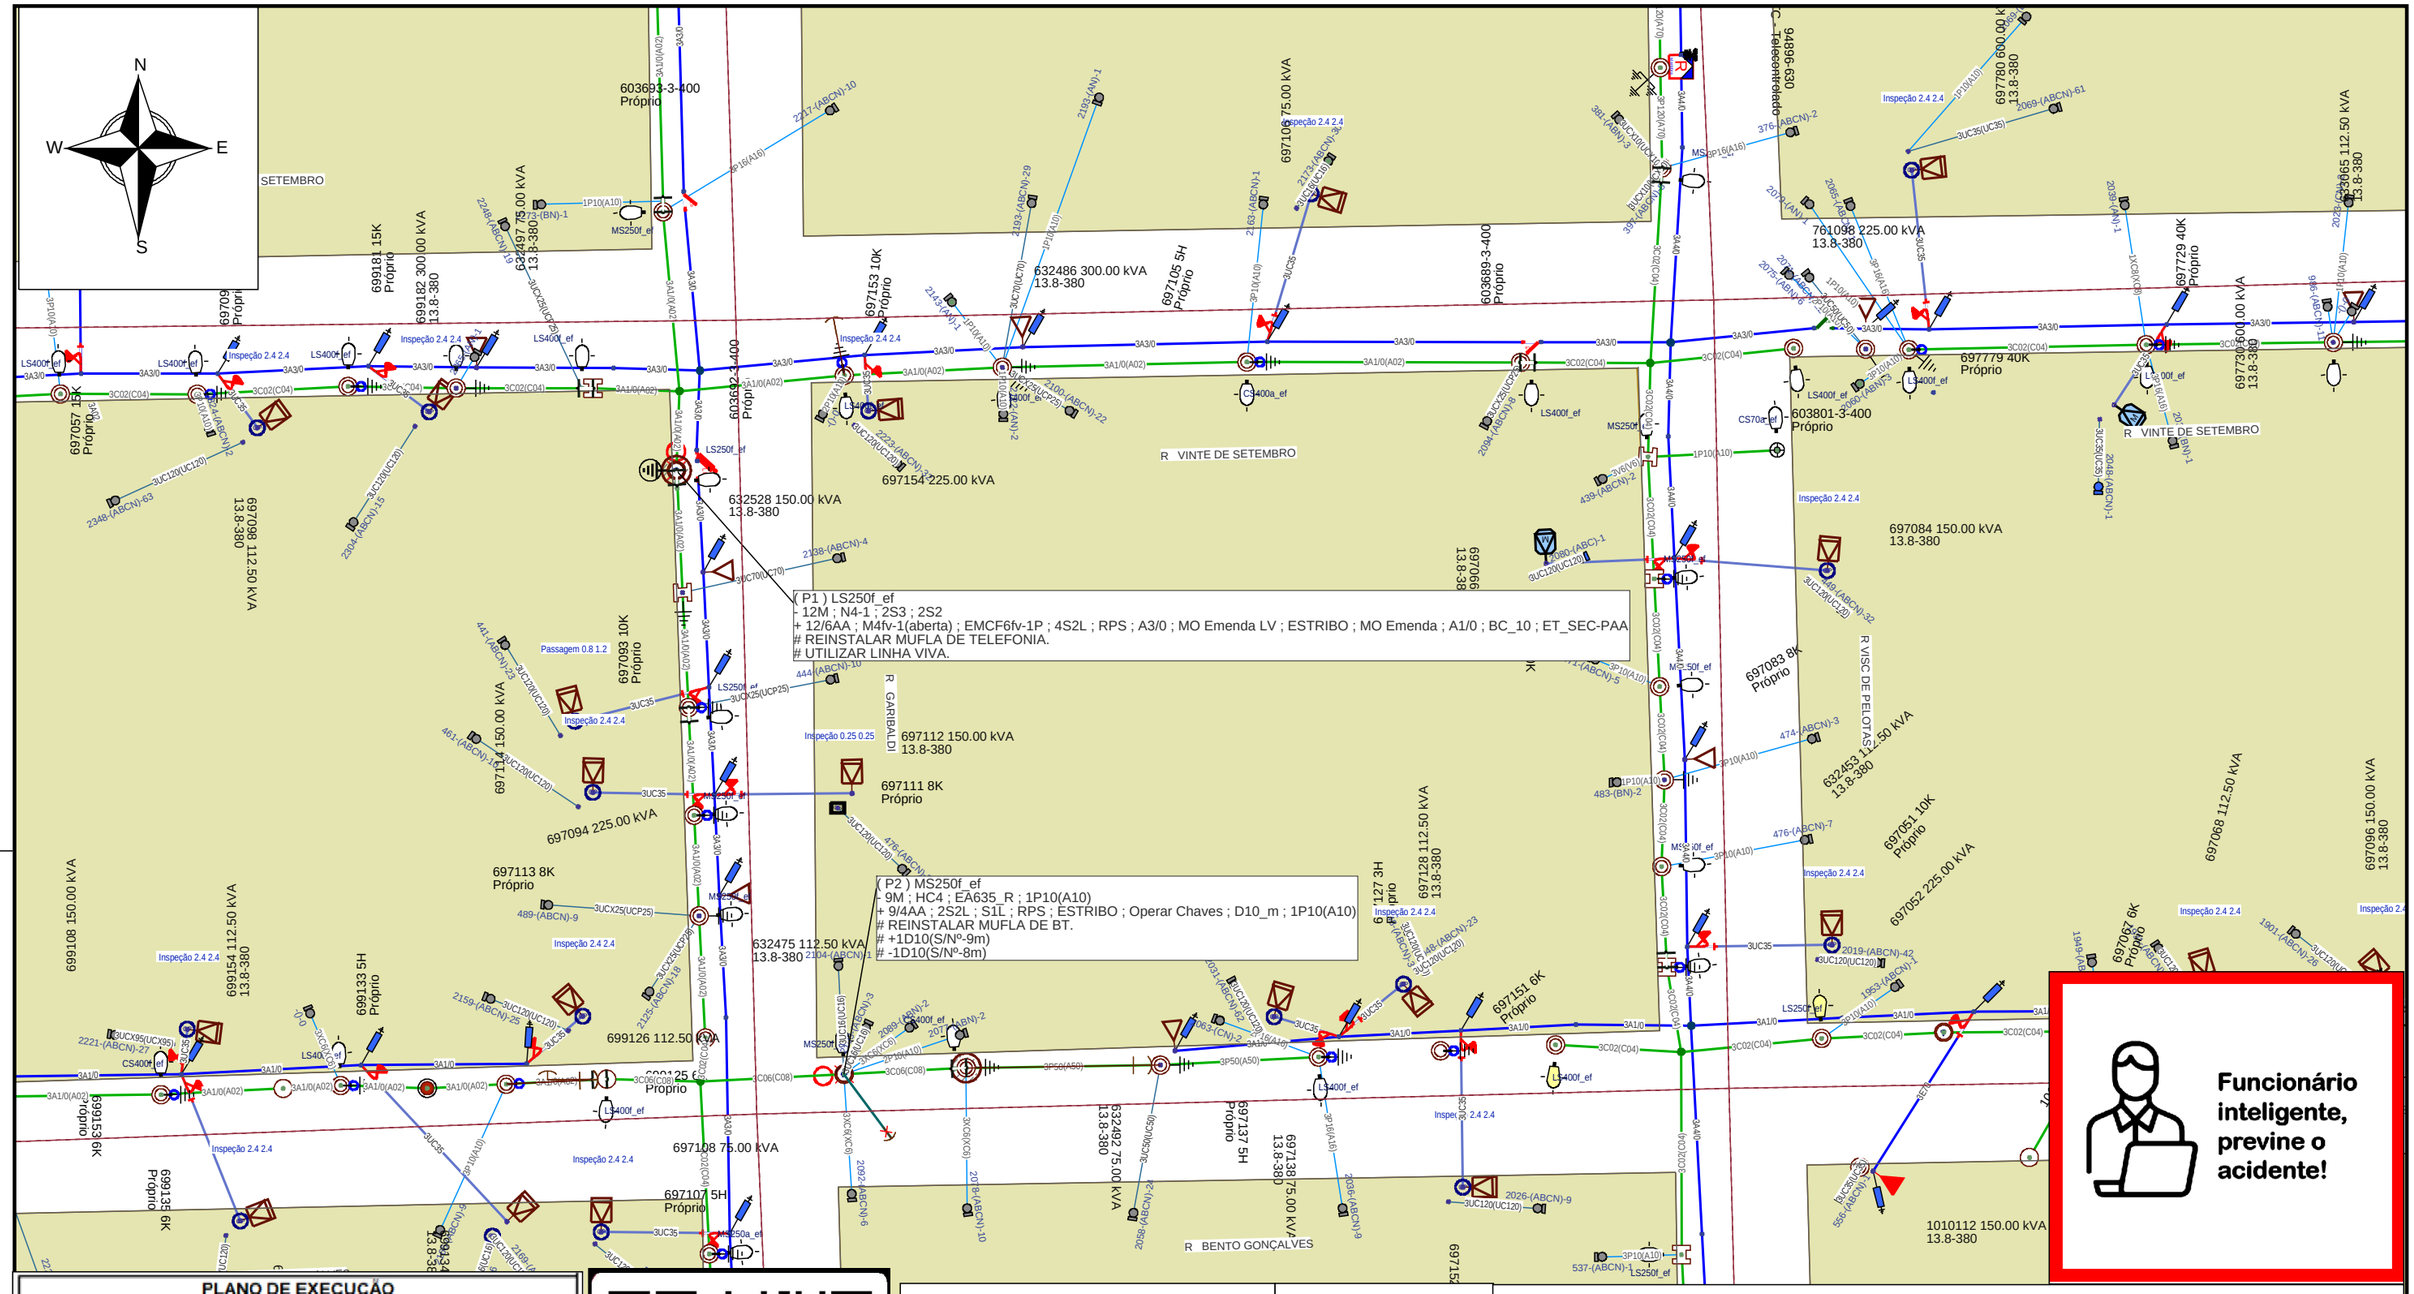

PLANO DE EXECUÇÃO

Preparar a obra seguindo todos os passos de segurança.
SUBSTITUIR POSTES CONFORME INDICAÇÃO DE PROJETO.
REINSTALAR MUFLAS.
REPARAR CALÇADAS.
UTILIZAR LINHA VIVA.

ESSE PROJETO SÓ PODE SER ALTERADO POR SOLICITAÇÃO DE DI.
MANOBRAR EQUIPAMENTO ABAIXO PRA REALIZAR PROCEDIMENTO.

Ação	Equipamento	Número	Clientes	Duração	CHI
Desligar	Transformador	632486	71	5	355
Desligar	Transformador	632528	13	5	65
Desligar	Transformador	632475	40	5	200
Linha Viva?		Sim	CHI TOTAL		620

◯ Poste novo a ser instalado (quando indicado em planta)

FeedBack Para Fábrica de Projetos

Planeje
Use
Teste
Sinalize
Aterre

Pierre Menegoni Felscher
Pierre Menegoni Felscher
Gerência de Processos de Obras e Manuntenção | DROP
Técnico de Análise e Projetos
CFT: 025.116.280-07

CPFL ENERGIA

Gerência de Obras e Manutenção

Município: Caxias do Sul

Cliente: RGE DISTRIBUIDORA DE ENERGIA S.A

Obra: Substituição de Poste - TR 632528

Endereço: R GARIBALDI, 444 - CENTRO - CAXIAS DO SUL

Responsável Técnico:
Eng. Ederson Paulo Vogel
CREA: RS135794 ART: 10911826

Escala: 1:850	Data: 13/06/2025	Nota: 000006888589
Classe de isolação: 15kV	AL: KCS21	Folha 1
Projetista: Pierre Felscher	Projeto: 000007815971	Levantador: MARCIO BEDIN