


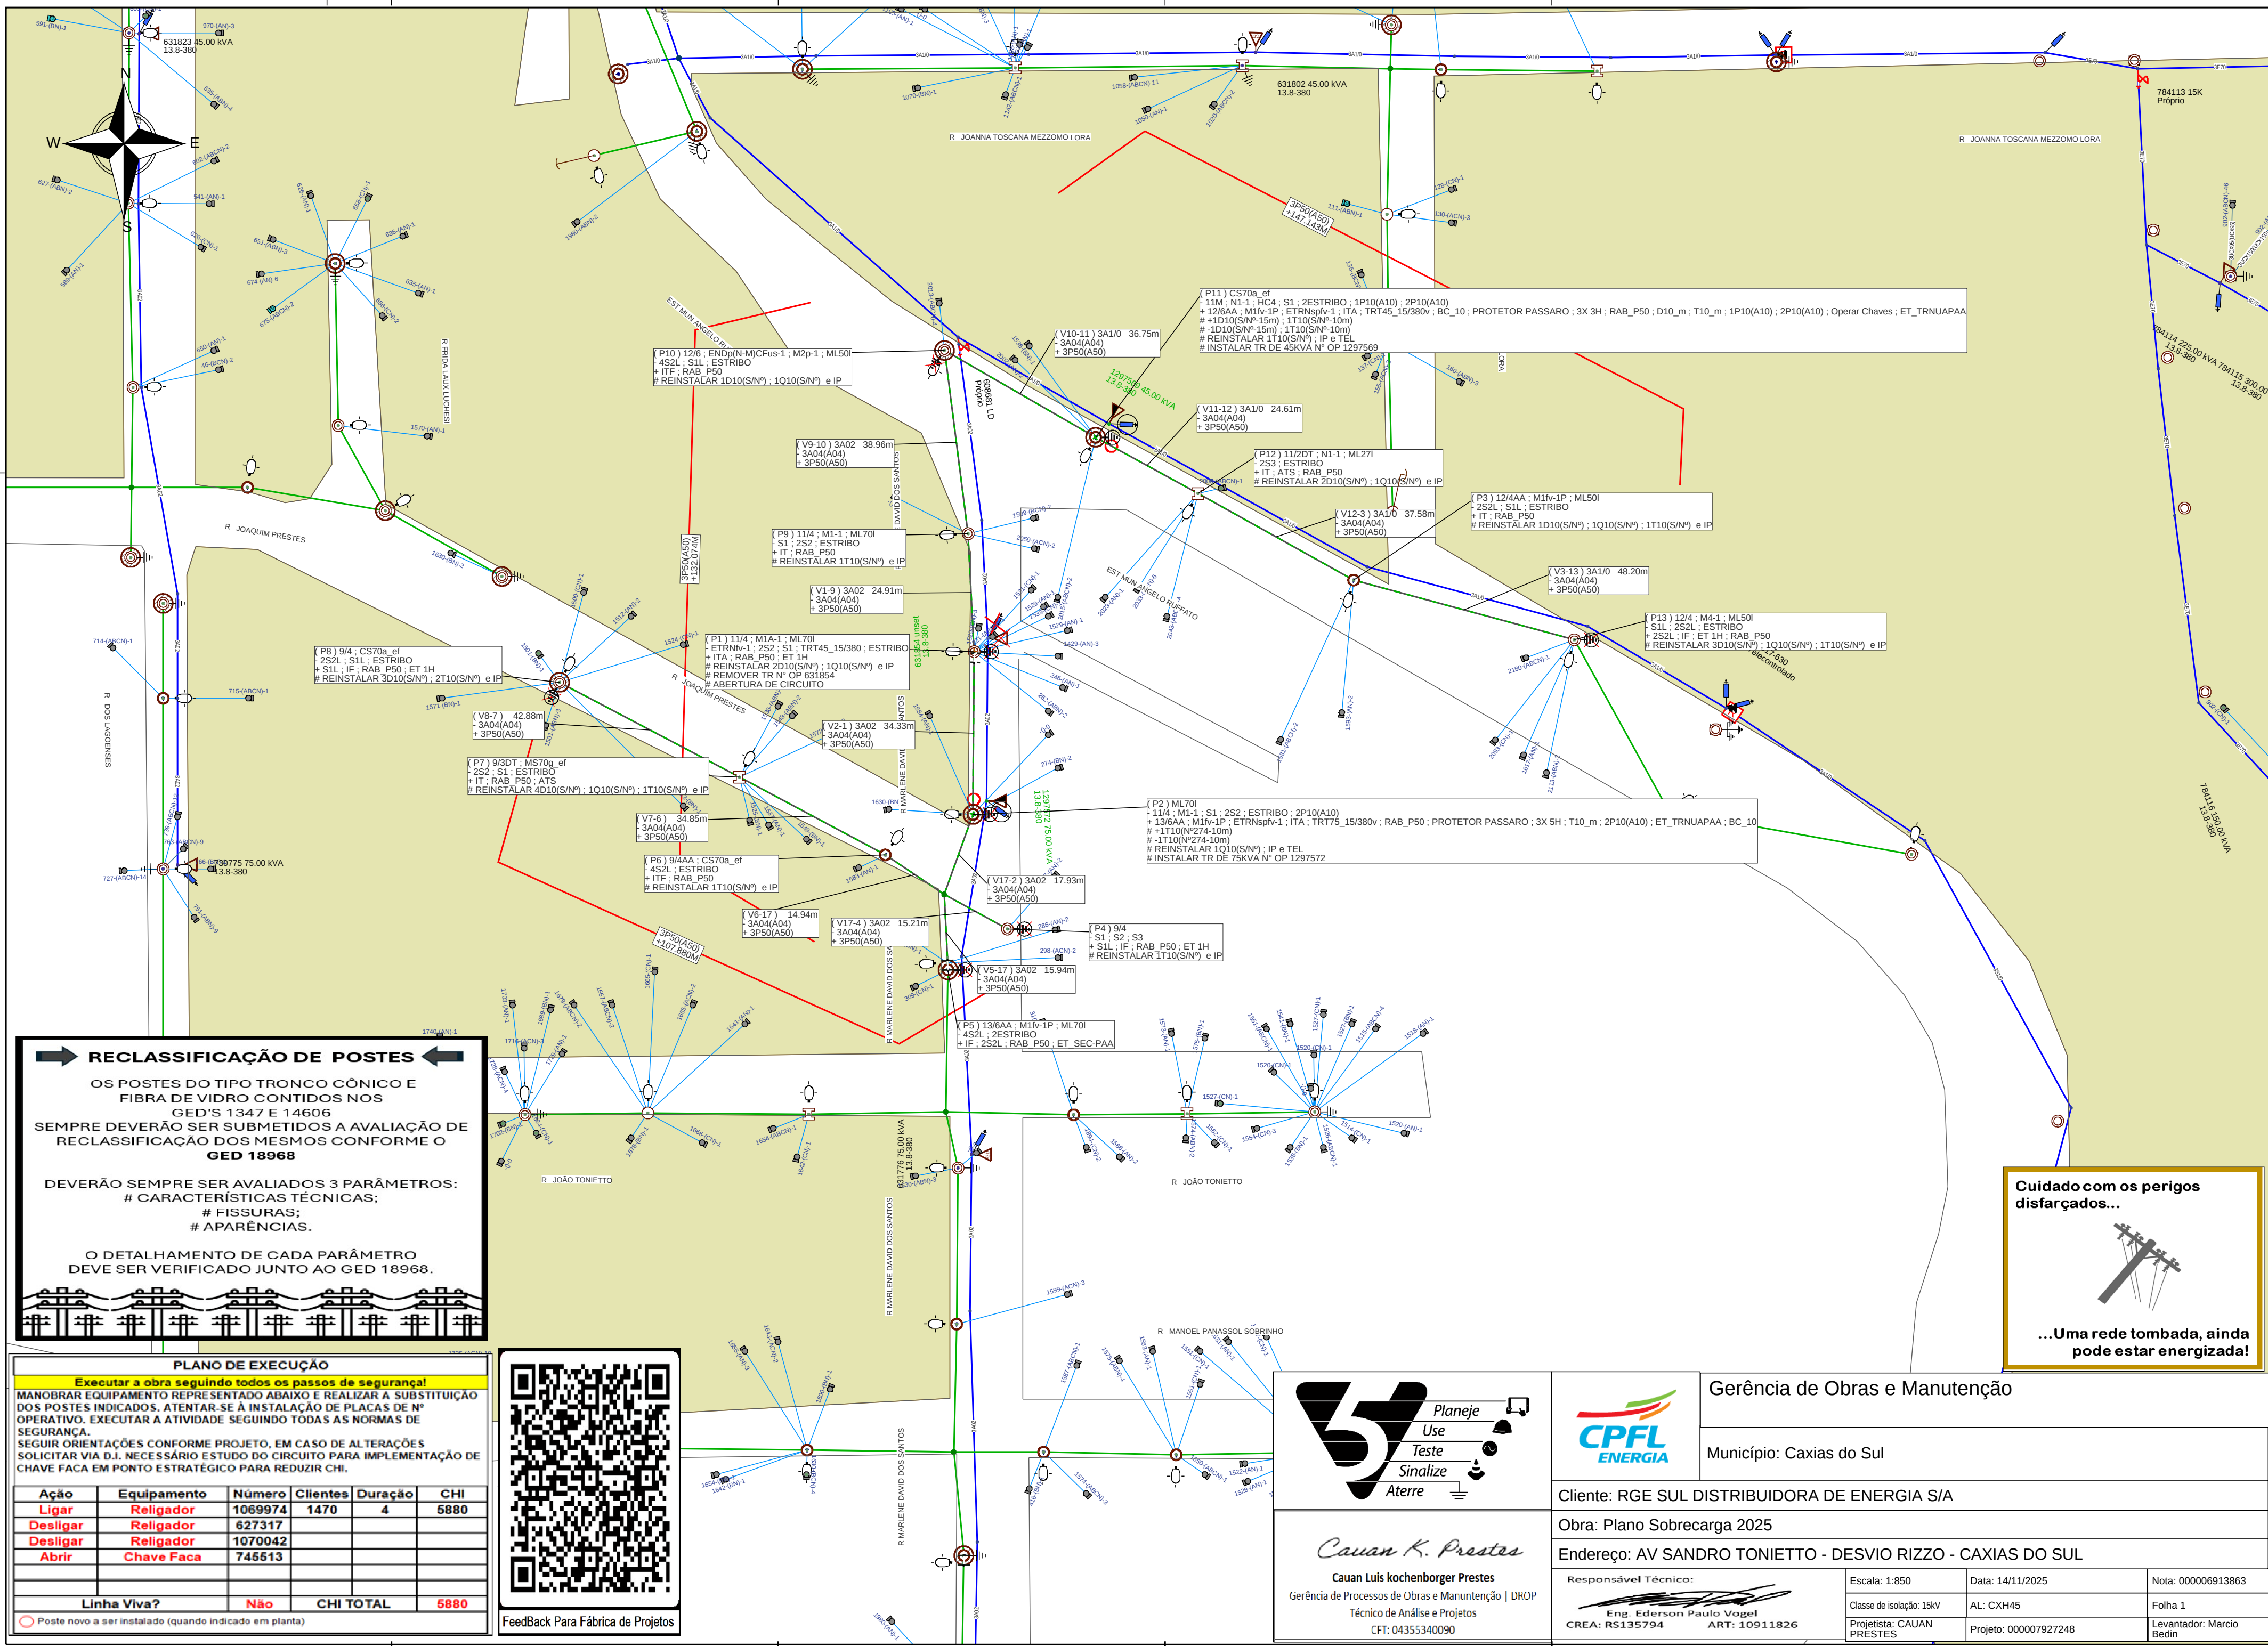

RECLASSIFICAÇÃO DE POSTES

OS POSTES DO TIPO TRONCO CÔNICO E FIBRA DE VIDRO CONTIDOS NOS GED'S 1347 E 14606 SEMPRE DEVERÃO SER SUBMETIDOS A AVALIAÇÃO DE RECLASSIFICAÇÃO DOS MESMOS CONFORME O GED 18968

DEVERÃO SEMPRE SER AVALIADOS 3 PARÂMETROS:
CARACTERÍSTICAS TÉCNICAS;
FISSURAS;
APARÊNCIAS.

O DETALHAMENTO DE CADA PARÂMETRO DEVE SER VERIFICADO JUNTO AO GED 18968.

PLANO DE EXECUÇÃO

Executar a obra seguindo todos os passos de segurança! MANOBRAR EQUIPAMENTO REPRESENTADO ABAIXO E REALIZAR A SUBSTITUIÇÃO DOS POSTES INDICADOS. ATENTAR-SE À INSTALAÇÃO DE PLACAS DE Nº OPERATIVO. EXECUTAR A ATIVIDADE SEGUINDO TODAS AS NORMAS DE SEGURANÇA. SEGUIR ORIENTAÇÕES CONFORME PROJETO, EM CASO DE ALTERAÇÕES SOLICITAR VIA D.I. NECESSÁRIO ESTUDO DO CIRCUITO PARA IMPLEMENTAÇÃO DE CHAVE FACA EM PONTO ESTRATÉGICO PARA REDUZIR CHI.

Ação	Equipamento	Número	Cilentes	Duração	CHI
Ligar	Religador	1069974	1470	4	5880
Desligar	Religador	627317			
Desligar	Religador	1070042			
Abrir	Chave Faca	745513			
Linha Viva?	Não	CHI TOTAL			5880

Poste novo a ser instalado (quando indicado em planta)

FeedBack Para Fábrica de Projetos

Planeje
Use
Teste
Sinalize
Aterre

Cauan K. Prestes

Cauan Luis kochenborger Prestes
Gerência de Processos de Obras e Manutenção | DROP
Técnico de Análise e Projetos
CFT: 04355340090

Gerência de Obras e Manutenção

Município: Caxias do Sul

Cliente: RGE SUL DISTRIBUIDORA DE ENERGIA S/A

Obra: Plano Sobrecarga 2025

Endereço: AV SANDRO TONIETTO - DESVIO RIZZO - CAXIAS DO SUL

Responsável Técnico:

Eng. Ederson Paulo Vogel
CREA: RS135794 ART: 10911826

Escala: 1:850
Classe de isolamento: 15kV
Projetista: CAUAN PRESTES

Data: 14/11/2025
AL: CXH45
Projeto: 000007927248

Nota: 000006913863
Folha 1
Levantador: Marcio Bedin