


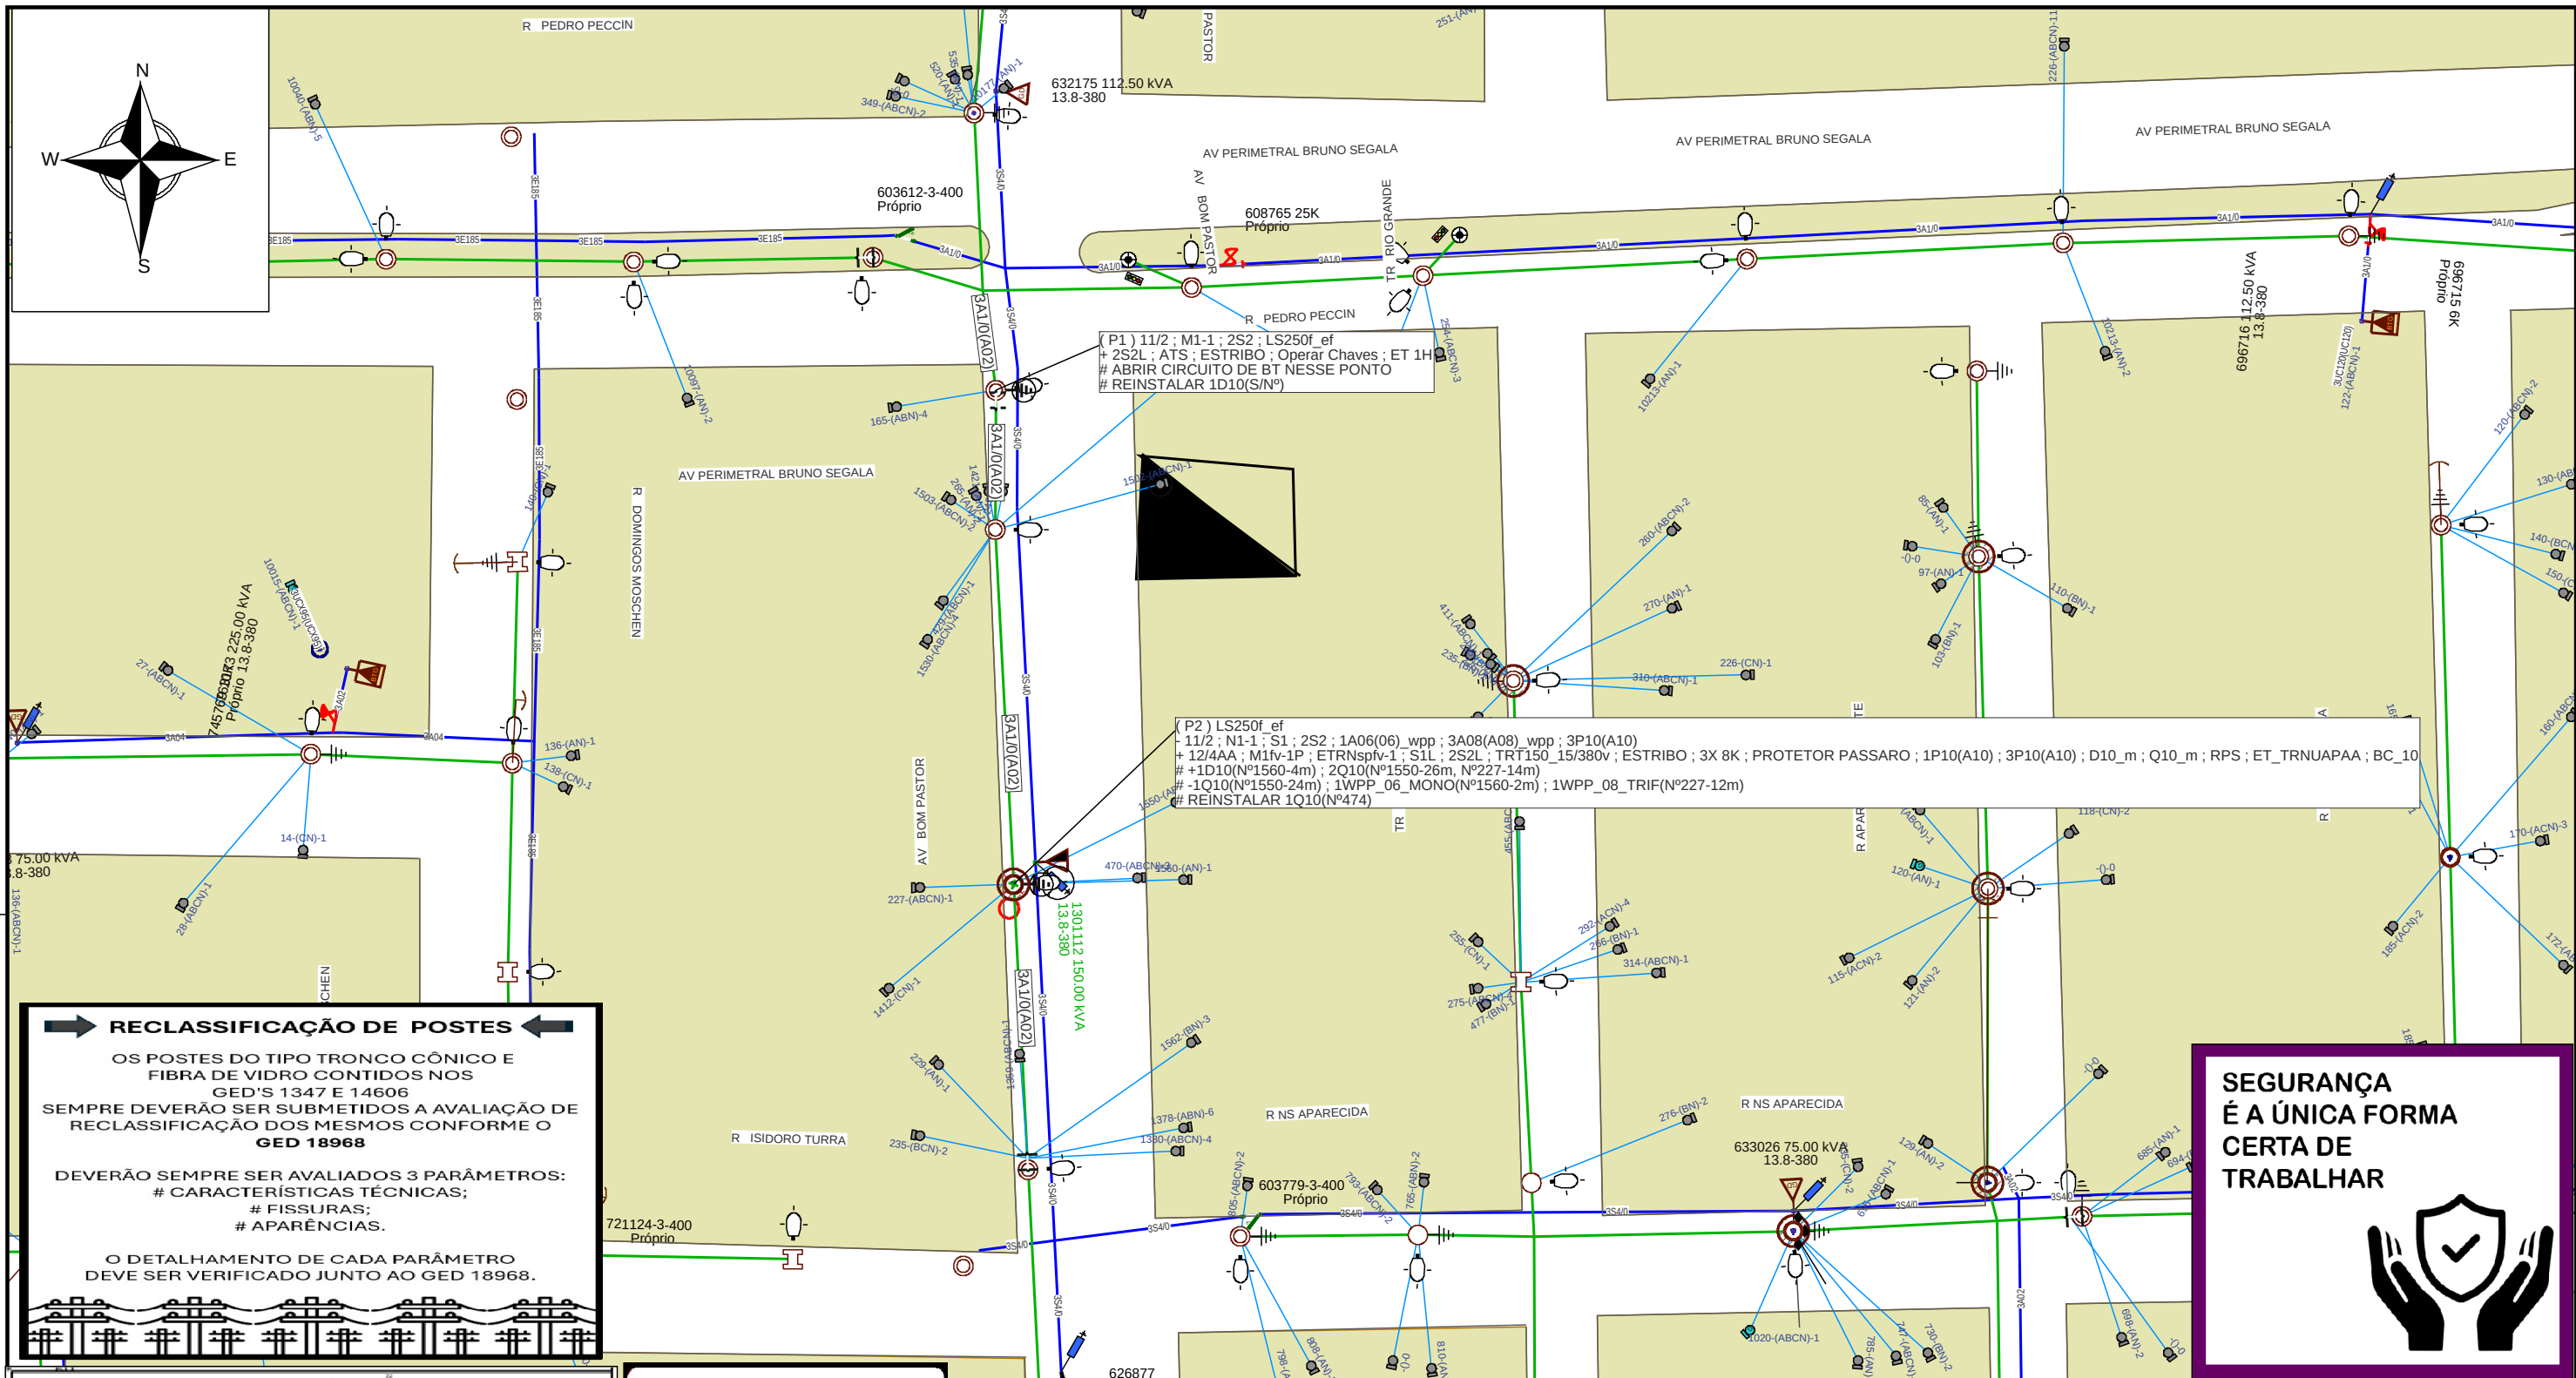

RECLASSIFICAÇÃO DE POSTES

OS POSTES DO TIPO TRONCO CÔNICO E FIBRA DE VIDRO CONTIDOS NOS GED'S 1347 E 14606 SEMPRE DEVERÃO SER SUBMETIDOS A AVALIAÇÃO DE RECLASSIFICAÇÃO DOS MESMOS CONFORME O GED 18968

DEVERÃO SEMPRE SER AVALIADOS 3 PARÂMETROS:

- # CARACTERÍSTICAS TÉCNICAS;
- # FISSURAS;
- # APARÊNCIAS.

O DETALHAMENTO DE CADA PARÂMETRO DEVE SER VERIFICADO JUNTO AO GED 18968.

SEGURANÇA É A ÚNICA FORMA CERTA DE TRABALHAR

PLANO DE EXECUÇÃO					
ABRIR CAVAS, PREPARAR OS PONTOS DA OBRA. REALIZAR ATIVIDADES COM LINHA VIVA .					
REALIZAR TODAS AS ATIVIDADES SEGUINDO AS NORMAS DE SEGURANÇA ESSE PROJETO SÓ PODE SER ALTERADO POR SOLICITAÇÃO DE DI.					
Ação	Equipamento	Número	Clientes	Duração	CHI
Abrir	Transformador	632175	54	4	216
Linha Viva?		Sim	CHI TOTAL		216
☐ Poste novo a ser instalado (quando indicado em planta)					

FeedBack Para Fábrica de Projetos

Planeje
Use
Teste
Sinalize
Aterre

Gabriel Vergani
Gerência de Processos de Obras e Manutenção | DROP
Técnico de Análise e Projetos
CFT: 040.224.970-41

Gerência de Obras e Manutenção

Município: Caxias do Sul

Cliente: RGE SUL DISTRIBUIDORA DE ENERGIA S/A

Obra: Plano Sobrecarga 2025

Endereço: AV BOM PASTOR, KAYSER, CAXIAS DO SUL RS

Responsável Técnico:

Eng. Ederson Paulo Vogel
CREA: RS135794 ART: 10911826

Escala: 1:850

Classe de isolamento: 15kV

Projetista: Gabriel Vergani

Data: 17/12/2025

AL: CXA14

Projeto: 000007946150

Nota: 000006913876

Folha 1

Levantador: Reinholdo Brulinger