


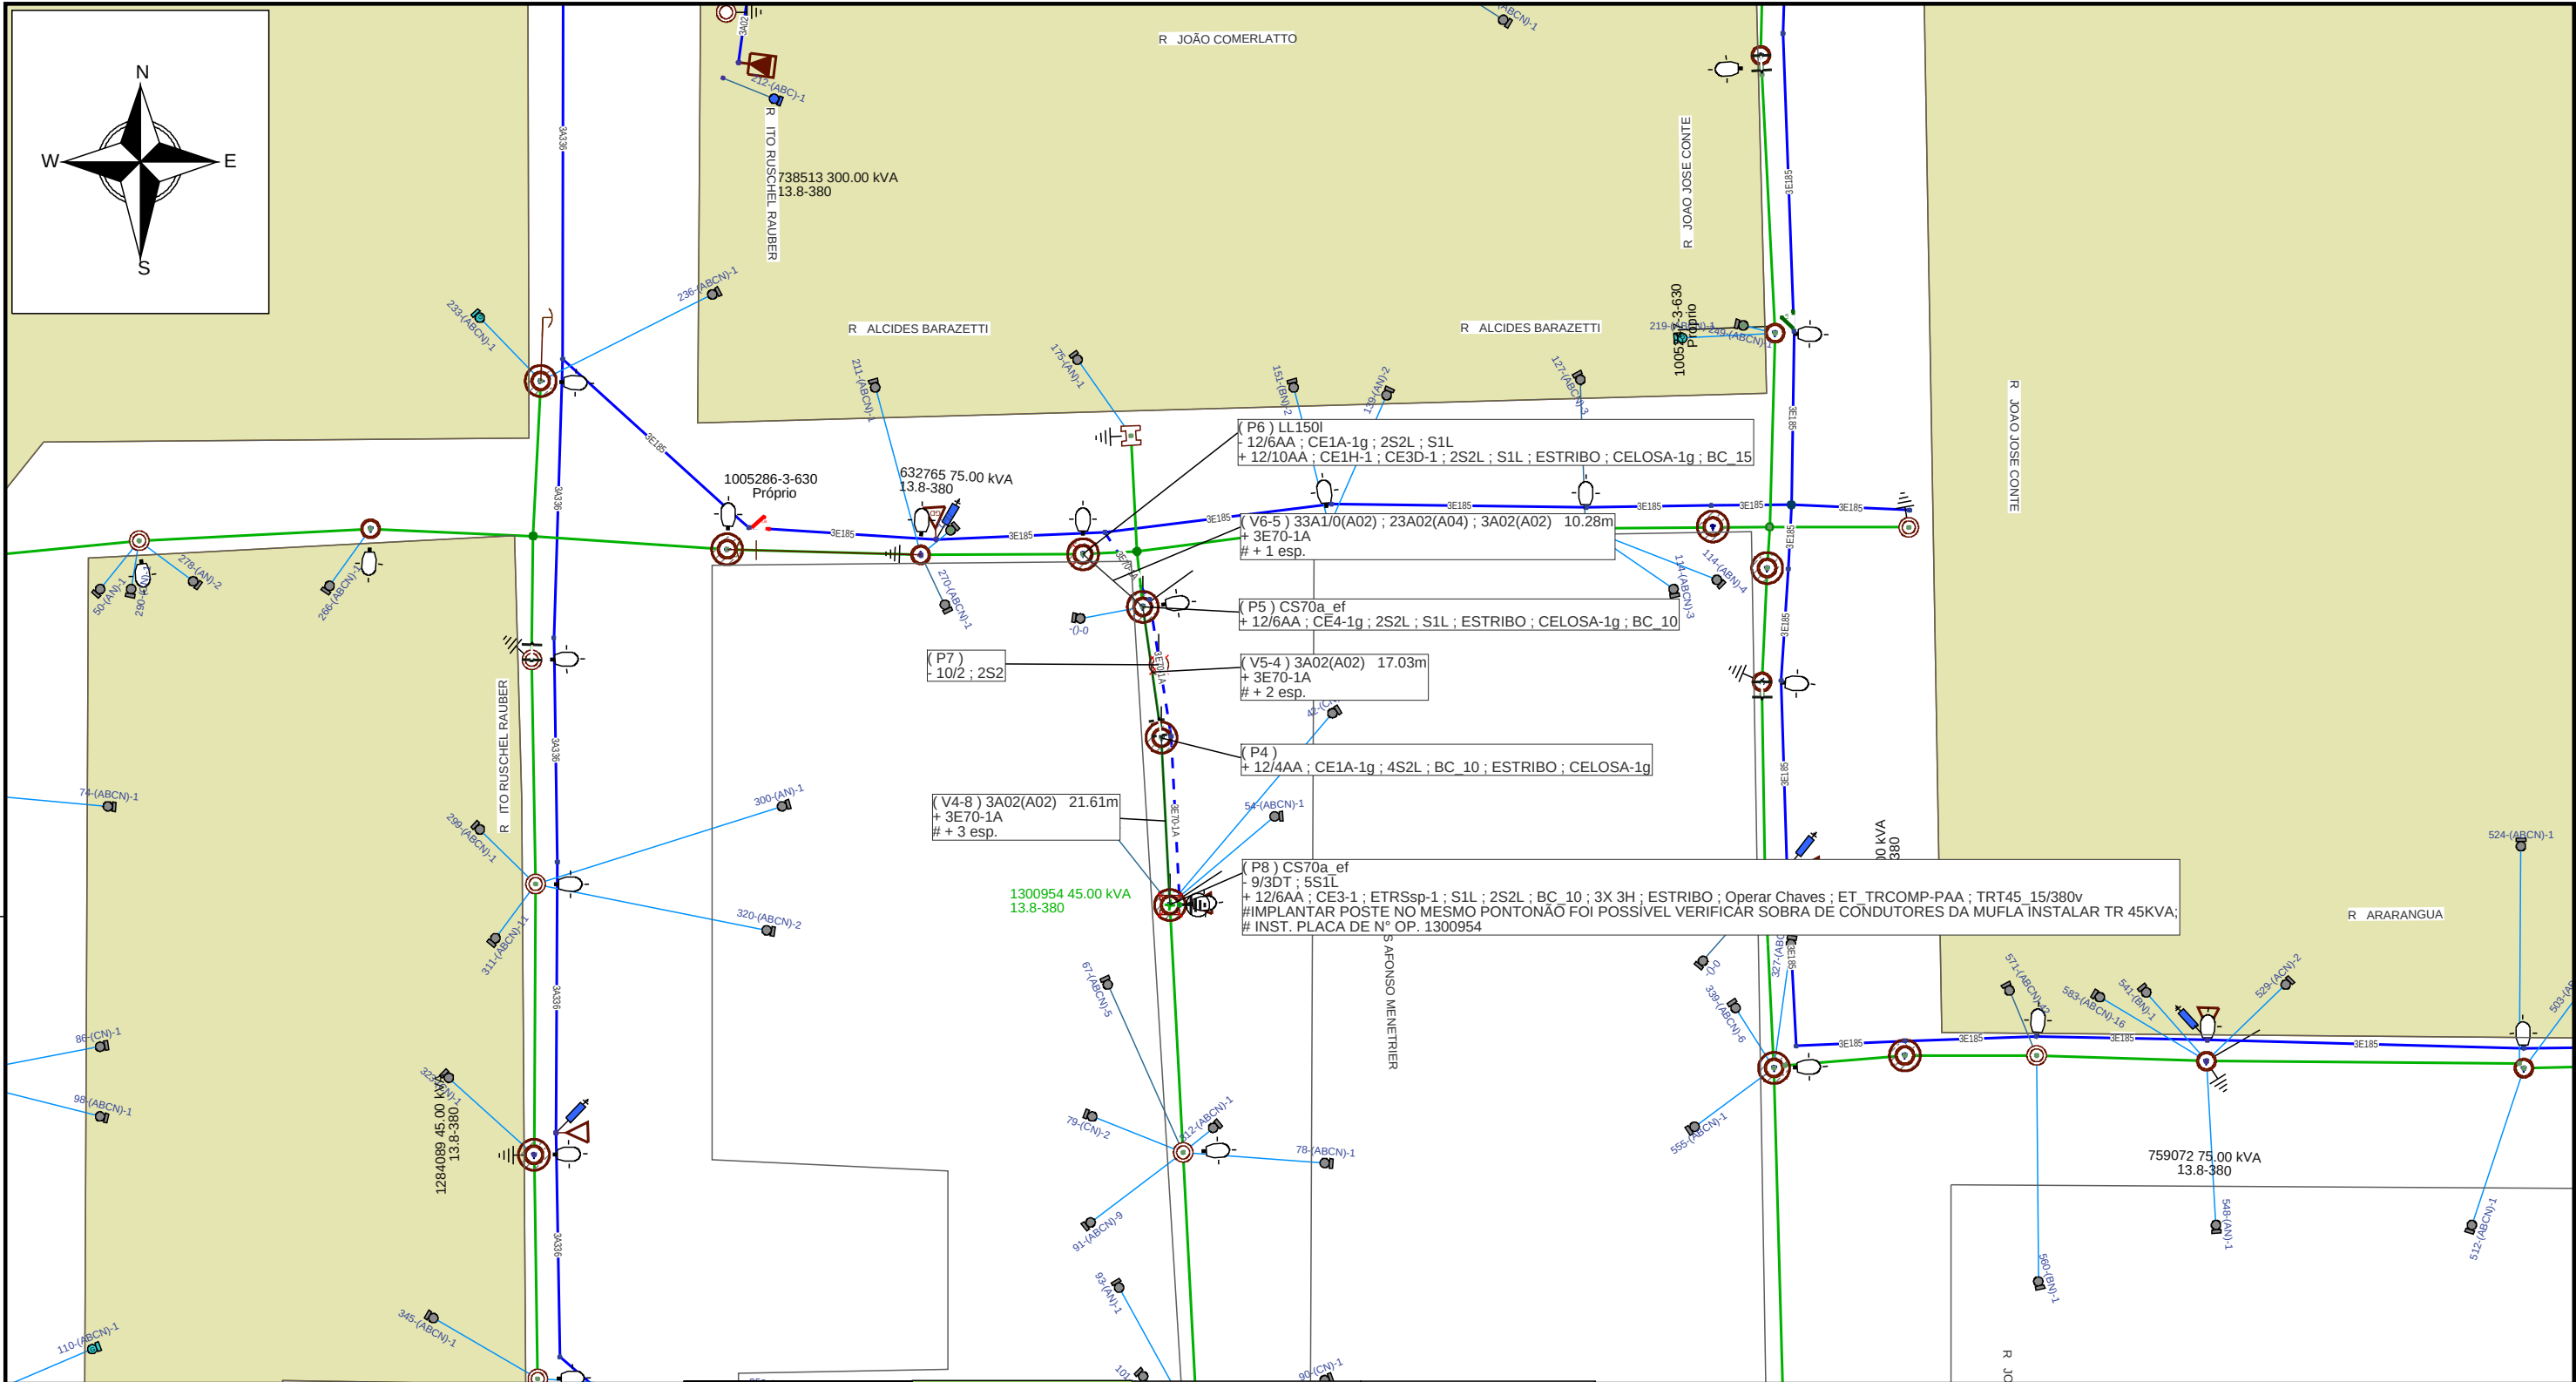

Intervir na rede conforme grade de estudos abaixo para substituir as estruturas apontadas na planta kaffa;
 Executar atividade com auxílio da linha viva.
 Se possível, na mesma programação podem ser executadas as seguintes notas 300001092919, 300001075223,

O DEC EM ESTUDO PODE SER OTIMIZADO EM ATÉ 425 A CHI					Quantidade de equipes sugeridas para o desligamento	
					0	0
 Busca Dado Busca Eq Busca Pa Chat Arquivos  Procurar  Assistente de IA (GPT)	Equipamento Desligado	Número Operativo	Clientes Desligados	Duração da intervenção	CHI Total	Observações (se necessário)
	TRANSFORMADOR	632765	75	5	375	

RECLASSIFICAÇÃO DE POSTES

OS POSTES DO TIPO TRONCO CÔNICO E FIBRA DE VIDRO CONTIDOS NOS GED'S 1347 E 1406 SEMPRE DEVERÃO SER SUBMETIDOS A AVALIAÇÃO DE RECLASSIFICAÇÃO DOS MESMOS CONFORME O GED 18968

DEVERÃO SEMPRE SER AVALIADOS 3 PARÂMETROS:
CARACTERÍSTICAS TÉCNICAS;
FISSURAS;
APARÊNCIAS.

O DETALHAMENTO DE CADA PARÂMETRO DEVE SER VERIFICADO JUNTO AO GED 18968.

Seja a mudança que você quer ver na segurança do trabalho.

Planeje
Use
Teste
Sinalize
Aterre

FeedBack Para Fábrica de Projetos

Henrique Silva Erguy Junior

Gerência de Processos de Obras e Manutenção | DROP

Técnico de Análise Projetos I

CFT: 5287547404-9

CPFL ENERGIA

Gerência de Obras e Manutenção

Município: Caxias do Sul

Cliente: RIO GRANDE ENERGIA S.A.

Obra: Plano Sobrecarga 2025

Endereço: 632765

Responsável Técnico: Eng. Ederson Paulo Vogel
CREA: RS135794 ART: 10911826

Escala: 1:850
Classe de isolamento: 15kV
Projetista: henrique erguy

Data: 02/12/2025
AL: CXG24
Projeto: 000007937013

Nota: 000006914043
Folha 1
Levantador: ricardo