


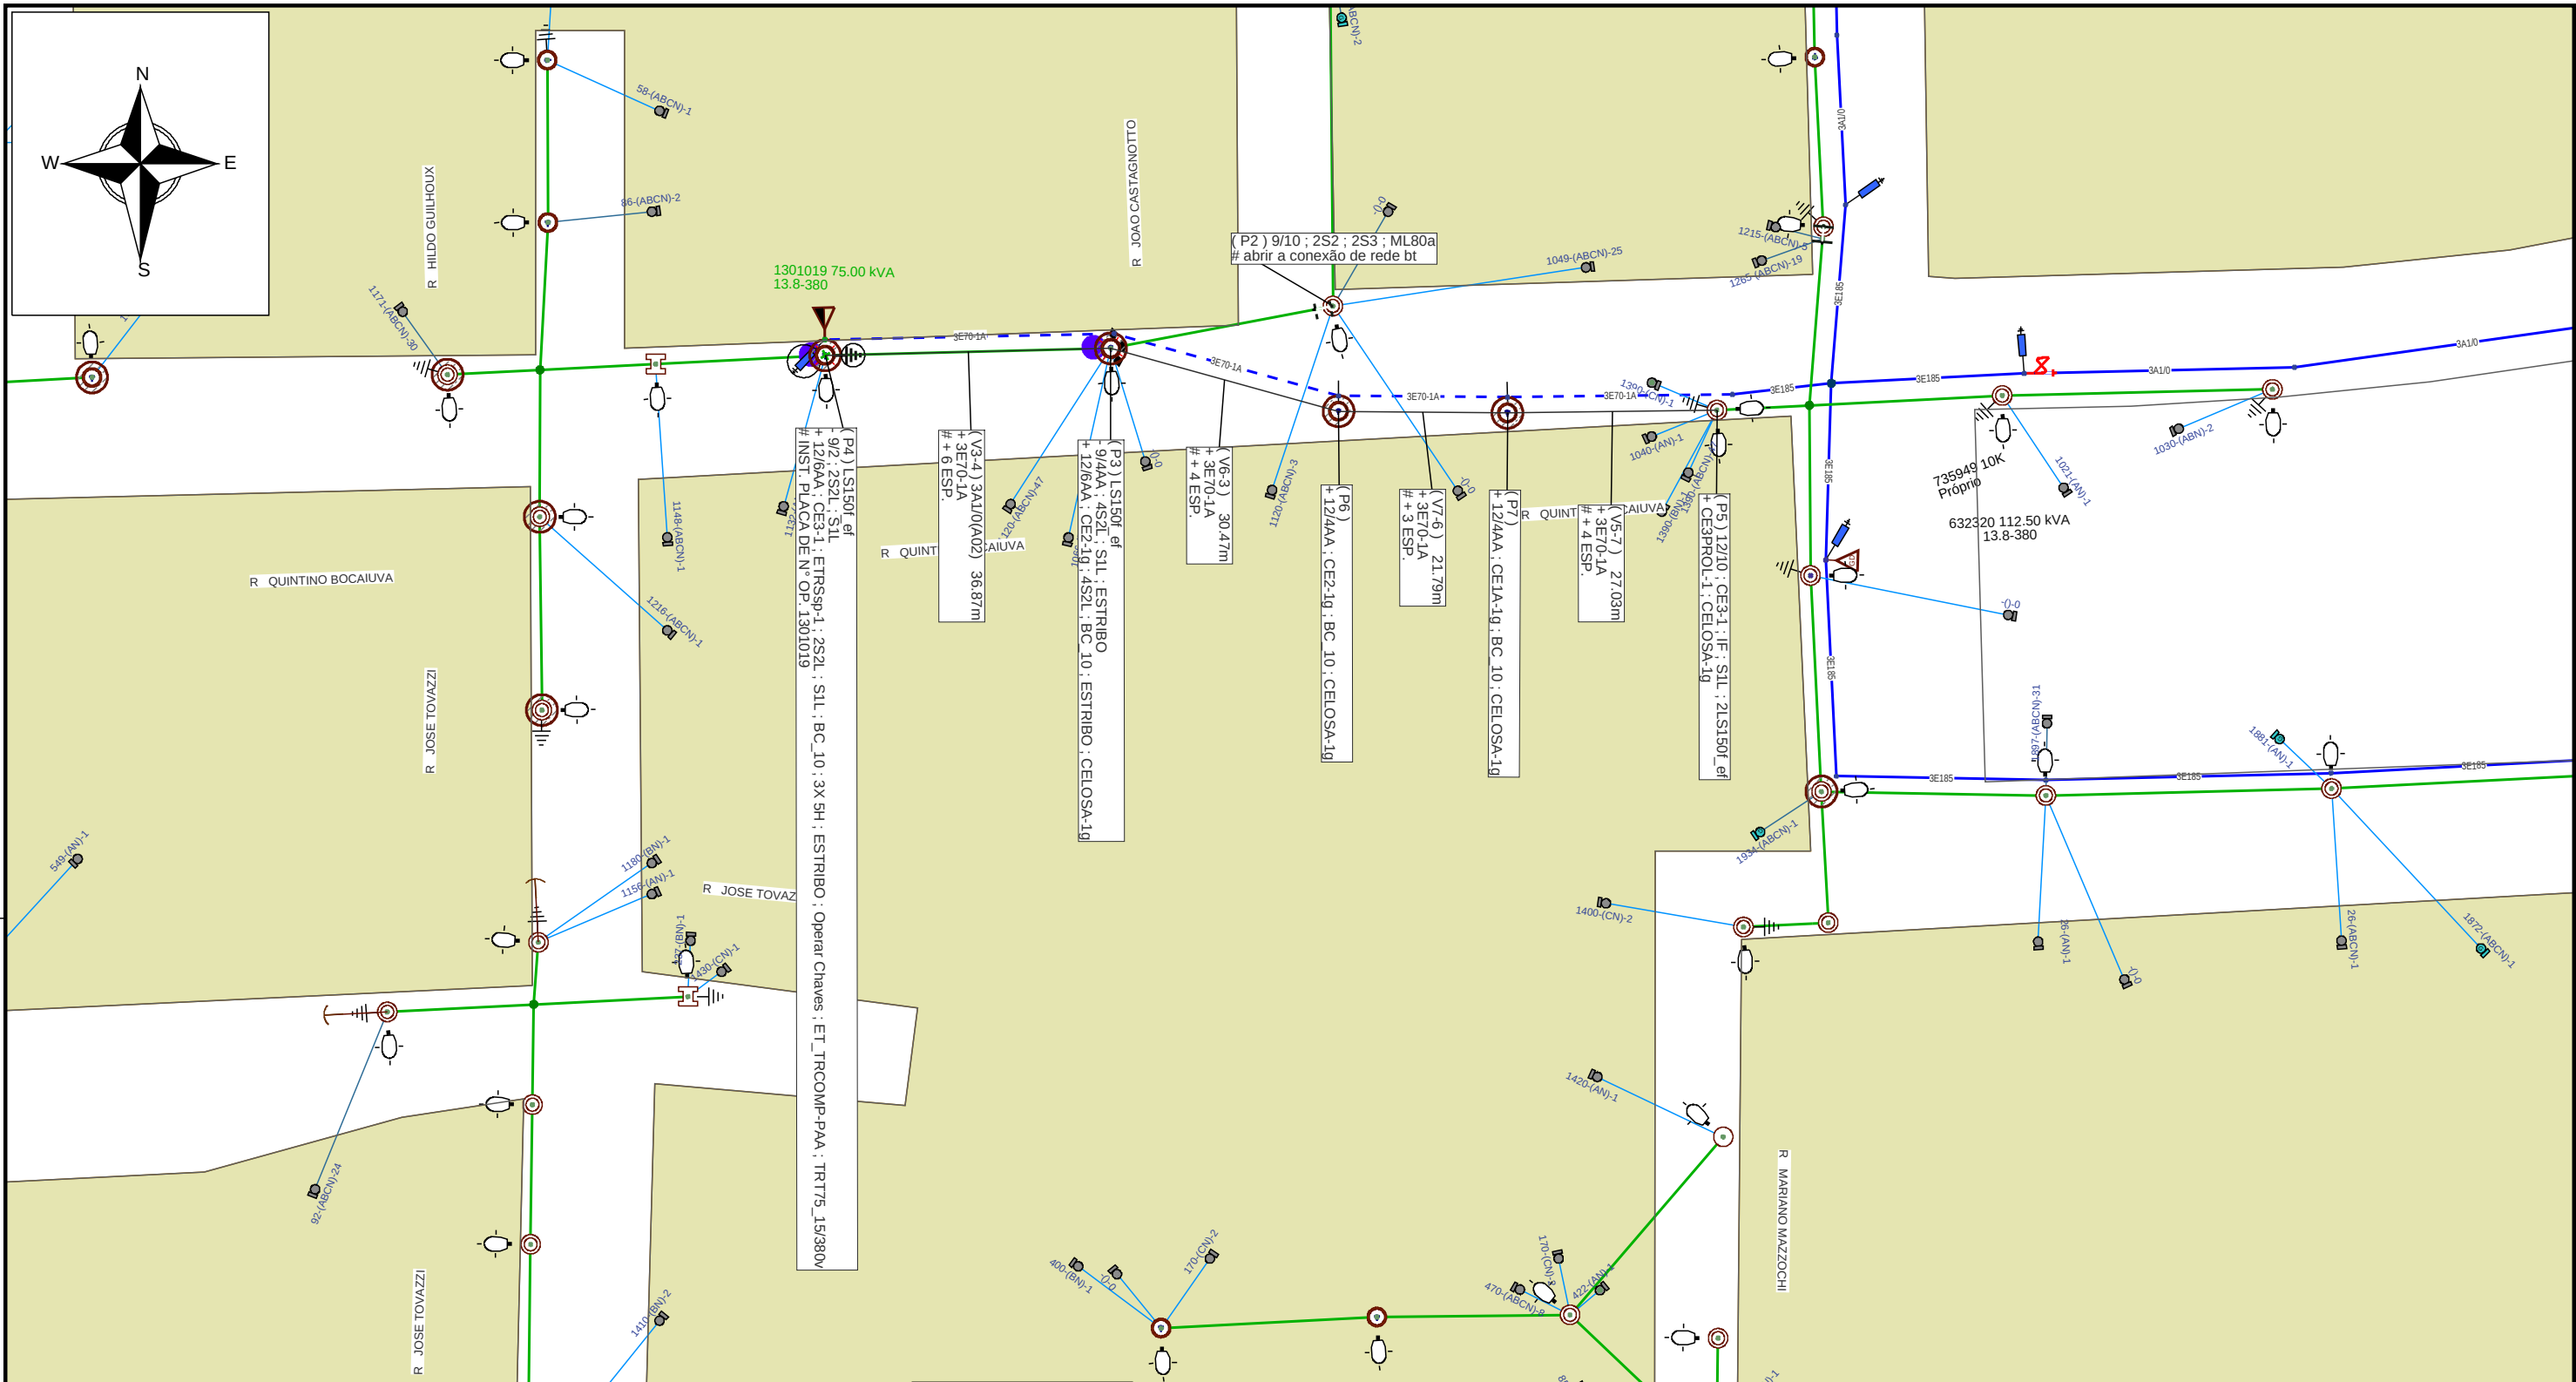

Na preparação implantar postes + estender rede MT do P5 P4 + prever tr no p4 segundo estudo + conectar rede + instalar Tr + tirar rede e postes velhos (desligar TR 719907)

NÃO FORAM LOCALIZADAS OTIMIZAÇÕES PARA DEC PROGRAMADO					Quantidade de equipes sugeridas para o desligamento	
Equipamento Desligado	Número Operativo	Clientes Desligados	Duração da intervenção	CHI Total	Observações (se necessário)	
TRANSFORMADOR	719907	177	4	708		
ESTUDO DE CHI					Totat	708

RE: 0000335 Base interna de dados 08/03/2025

Técnico: ADELAR MIGUEL FERREIRA GRAFE Data da análise: 15/01/2024

RECLASSIFICAÇÃO DE POSTES

OS POSTES DO TIPO TRONCO CÔNICO E FIBRA DE VIDRO CONTIDOS NOS GED'S 1347 E 14506 SEMPRE DEVERÃO SER SUBMETIDOS A AVALIAÇÃO DE RECLASSIFICAÇÃO DOS MESMOS CONFORME O GED 18968

DEVERÃO SEMPRE SER AVALIADOS 3 PARÂMETROS:
CARACTERÍSTICAS TÉCNICAS;
FISSURAS;
APARÊNCIAS.

O DETALHAMENTO DE CADA PARÂMETRO DEVE SER VERIFICADO JUNTO AO GED 18968.

Seja a mudança que você quer ver na segurança do trabalho.

Planeje
Use
Teste
Sinalize
Aterre

FeedBack Para Fábrica de Projetos

Henrique Silva Erguy Junior

Gerência de Processos de Obras e Manutenção | DROP

Técnico de Análise Projetos I

CPF: 5287547404-9

Gerência de Obras e Manutenção

Município: Caxias do Sul

Cliente: RIO GRANDE ENERGIA S.A.

Obra: Plano Sobrecarga 2025

Endereço: 719907

Responsável Técnico:

Eng. Ederson Paulo Vogel
CREA: RS135794 ART: 10911826

Escala: 1:850

Classe de isolamento: 15kV

Projetista: HENRIQUE ERGUY

Data: 03/12/2025

AL: CXC14

Projeto: 000007937169

Nota: 000006914081

Folha 1

Levantador ADELAR GRAFE