


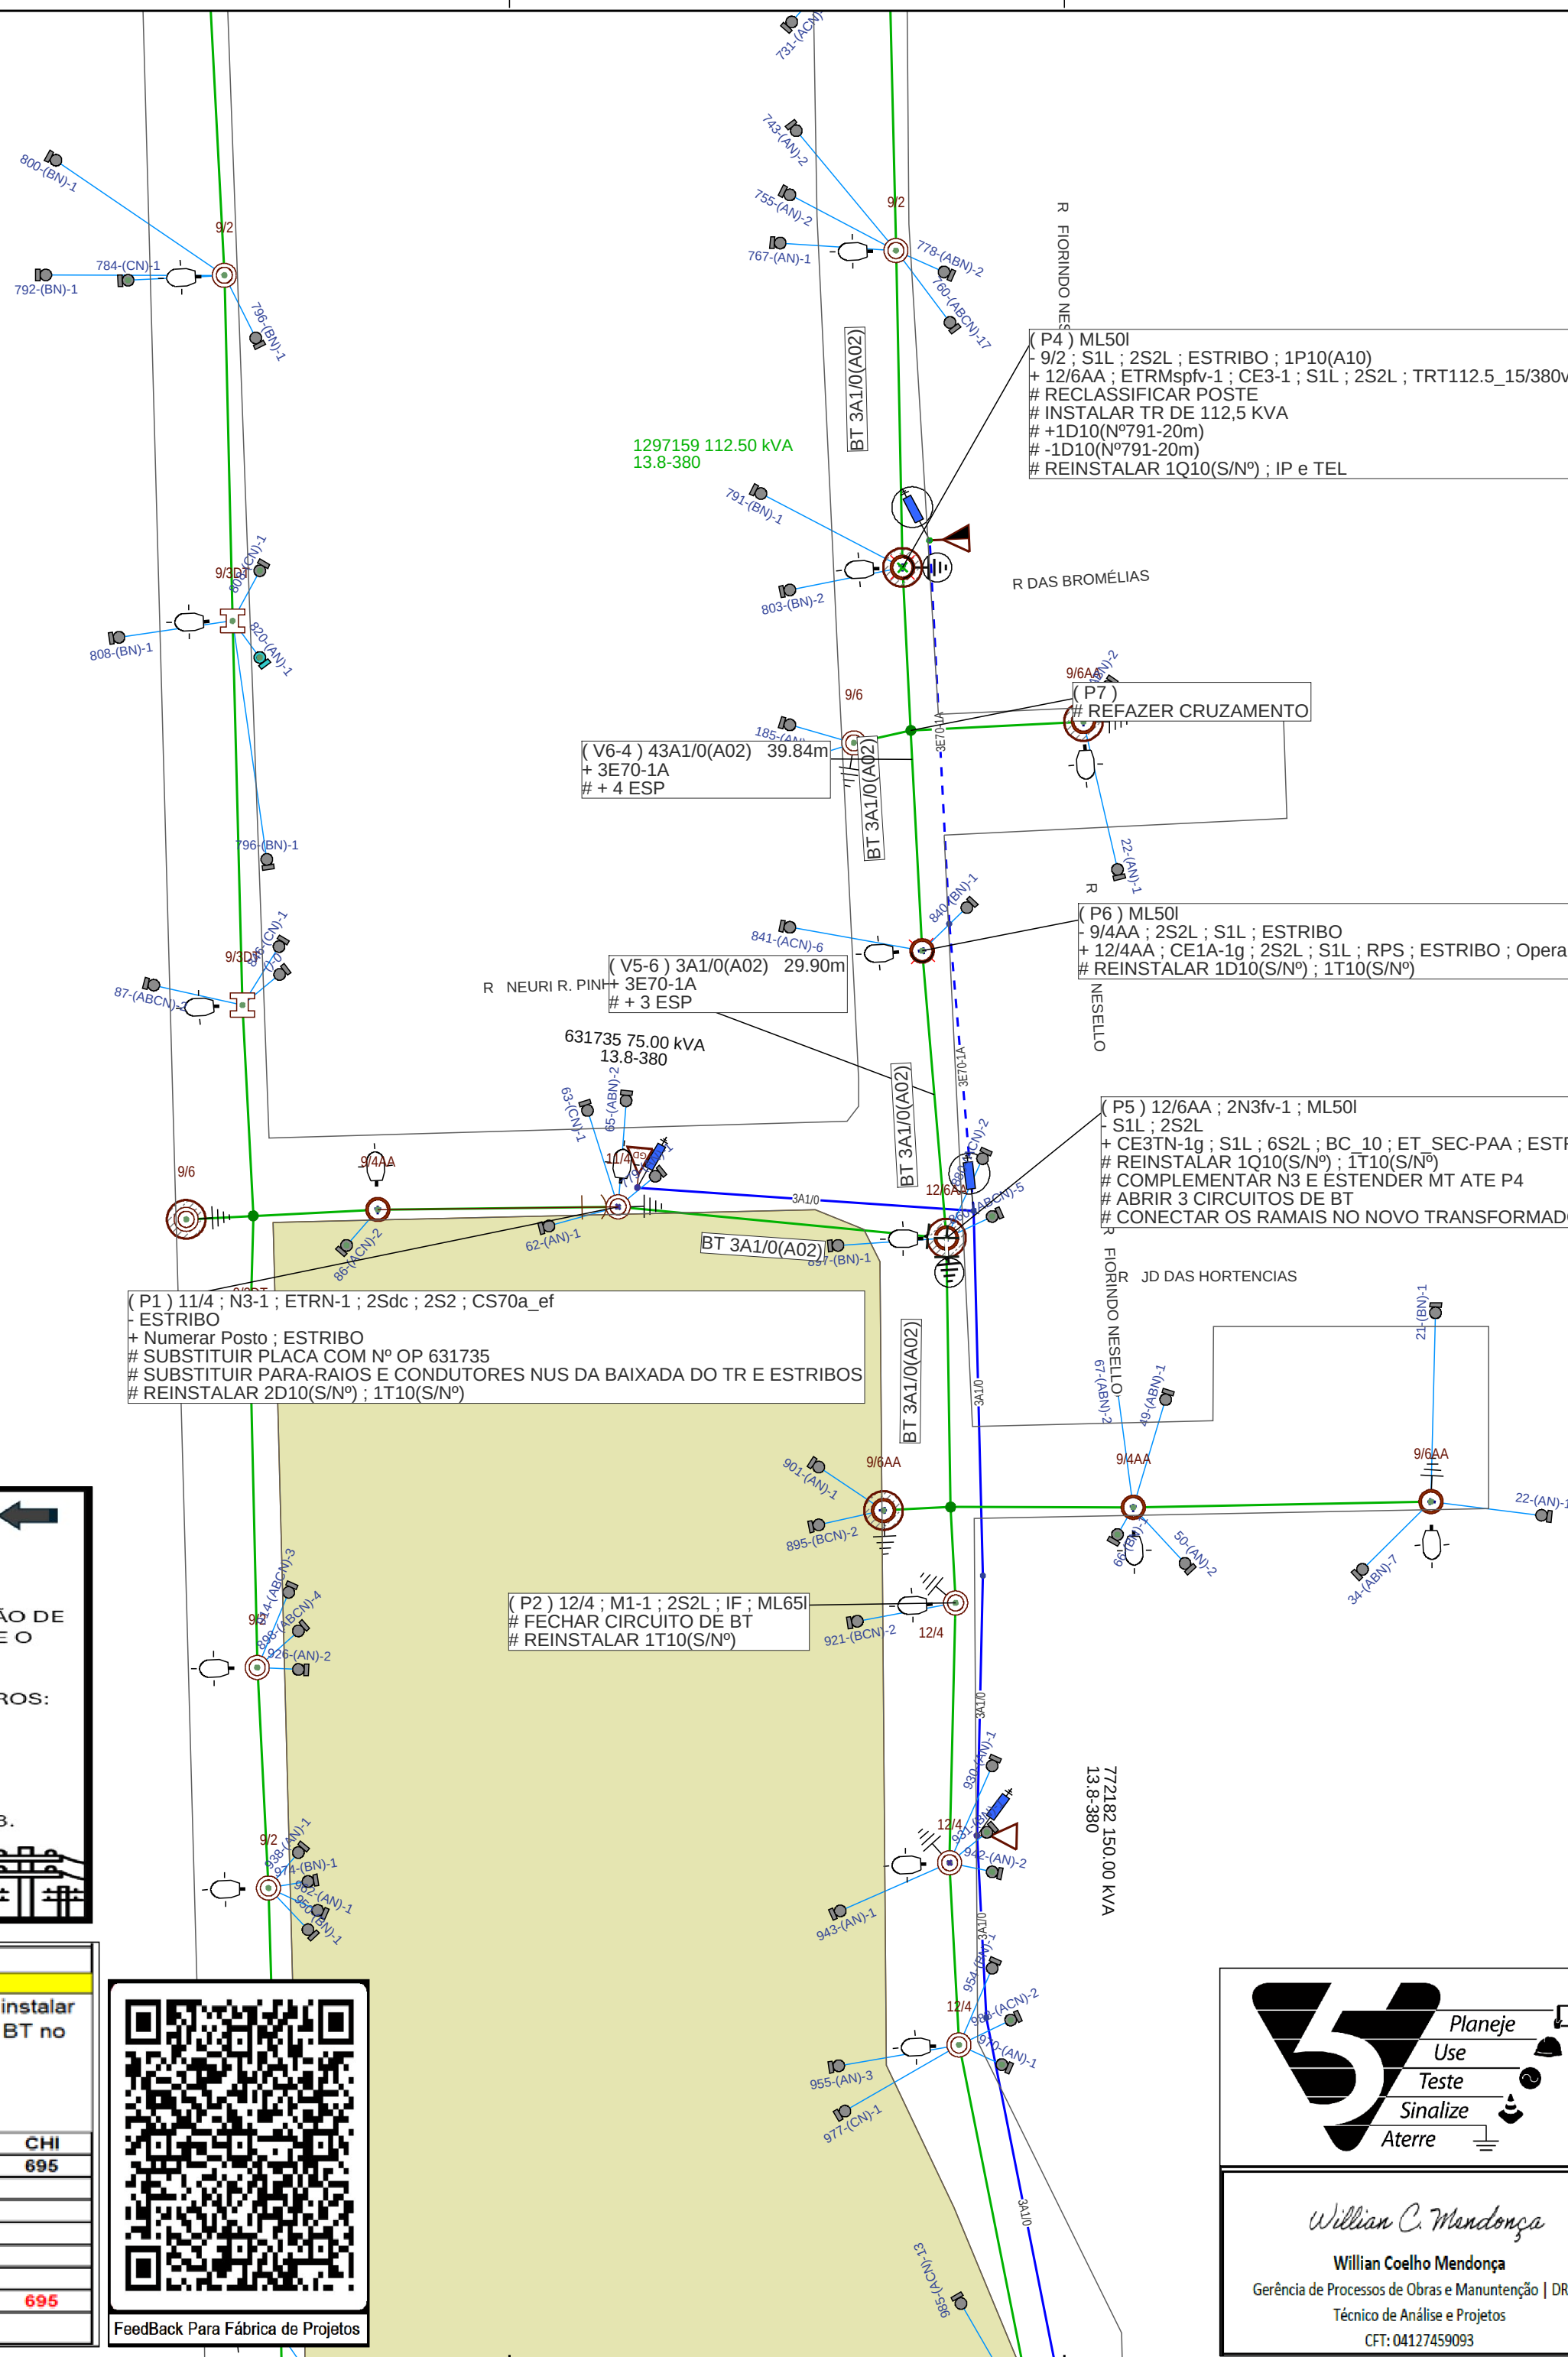

```

P4) ML50I
/ 9/2; S1L; 2S2L; ESTRIBO; 1P10(A10)
+ 12/6AA; ETRMpslv-1; CE3-1; S1L; 2S2L; TRT112.5_15/380v; 3X 6K; ESTRIBO; D10_n; 1P10(A10); RPS; BC_10; ET_TRCOMP-PAA
# RECLASSIFICAR POSTE
# INSTALAR TR DE 112,5 KVA
# +1D10(Nº791-20m)
# -1D10(Nº791-20m)
# REINSTALAR 1Q10(S/Nº); IP e TEL

```

(P6) ML50l
- 9/4AA ; 2S2L ; S1L ; ESTRIBO
+ 12/4AA ; CE1A-1g ; 2S2L ; S1L ; RPS ; ESTRIBO ; Operar Chaves ; CELOSA-1g
REINSTALAR 1D10(S/Nº) : 1T10(S/Nº)

```

P5 | 12/6AA ; 2N3fv-1 ; ML50I
S1L ; 2S2L
# CE3TN-1g ; S1L ; 6S2L ; BC_10 ; ET_SEC-PAA ; ESTRIBO ; CELOSA-1g
# REINSTALAR IQ10(S/N0) ; IT10(S/N0)
# COMPLEMENTAR N3 E ESTENDER MT ATE P4
# ABRIR 3 CIRCUITOS DE BT
# CONECTAR OS RAMAIS NO NOVO TRANSFORMADOR

```

```
(P1) 11/4; N3-1; ETRN-1; 2Sdc; 2S2; CS70a_ef
- ESTRIBO
+ Numerar Posto; ESTRIBO
# SUBSTITUIR PLACA COM Nº OP 631735
# SUBSTITUIR PARA-RAIOS E CONDUTORES NUS DA BAIXADA DO TR E ESTRIBOS
# REINSTALAR 2D10(S/Nº); 1T10(S/Nº)
```

(P2) 12/4 ; M1-1 ; 2S2L ; IF ; ML65I
FECHAR CIRCUITO DE BT
REINSTALAR 1T10(S/Nº)

OS POSTES DO TIPO TRONCO CÔNICO E
FIBRA DE VIDRO CONTIDOS NOS
GED'S 1347 E 14606
SEMPRE DEVERÃO SER SUBMETIDOS A AVALIAÇÃO DE
RECLASSIFICAÇÃO DOS MESMOS CONFORME O
GED 18968

DEVERÃO SEMPRE SER AVALIADOS 3 PARÂMETROS:

- # CARACTERÍSTICAS TÉCNICAS;
- # FISSURAS;
- # APARÊNCIAS.

O DETALHAMENTO DE CADA PARÂMETRO DEVE SER VERIFICADO JUNTO AO GED 18968.



Abrir chave faca e, em LM estender 2 vãos de MT para instalar novo TR de 112,5 kVA no P4. Abrir os três circuitos de BT no P5.

[illegible]

☐ Poste novo a ser instalado (quando indicado em planta)




FeedBack Para Fábrica de Projetos

Não improvise ferramentas,



**Quando já existem aquelas
que trazem segurança a
nossa vida!**

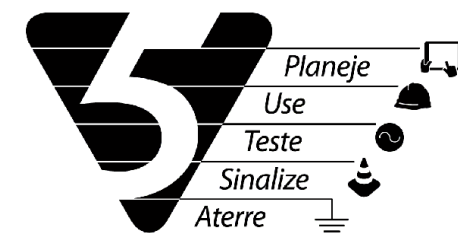

Willian C. Mendonça
Willian Coelho Mendonça
 Gerência de Processos de Obras e Manutenção | DROF
 Técnico de Análise e Projetos
 CEF: 04127459093



Gerência de Obras e Manutenção

Município: Caxias do Sul

Cliente: RGE SUL DISTRIBUIDORA DE ENERGIA S/A

Obra: Plano Sobrecarga 2025

Endereço: R FIORINDO NESELLO - CIDADE NOVA - CAXIAS DO SUL

Responsável Técnico:



Eng. Ederson Paulo Vogel

CREA: RS135794 ART: 10911826

Escala: 1:600
Classe de isolamento: 15kV
Projetista: Willian Co

	Data: 14/11/2025	Nota: 000006914093
	AL: CXH41	Folha 1
no	Projeto: 000007927381	Levantador: Ricardo Cavendo