


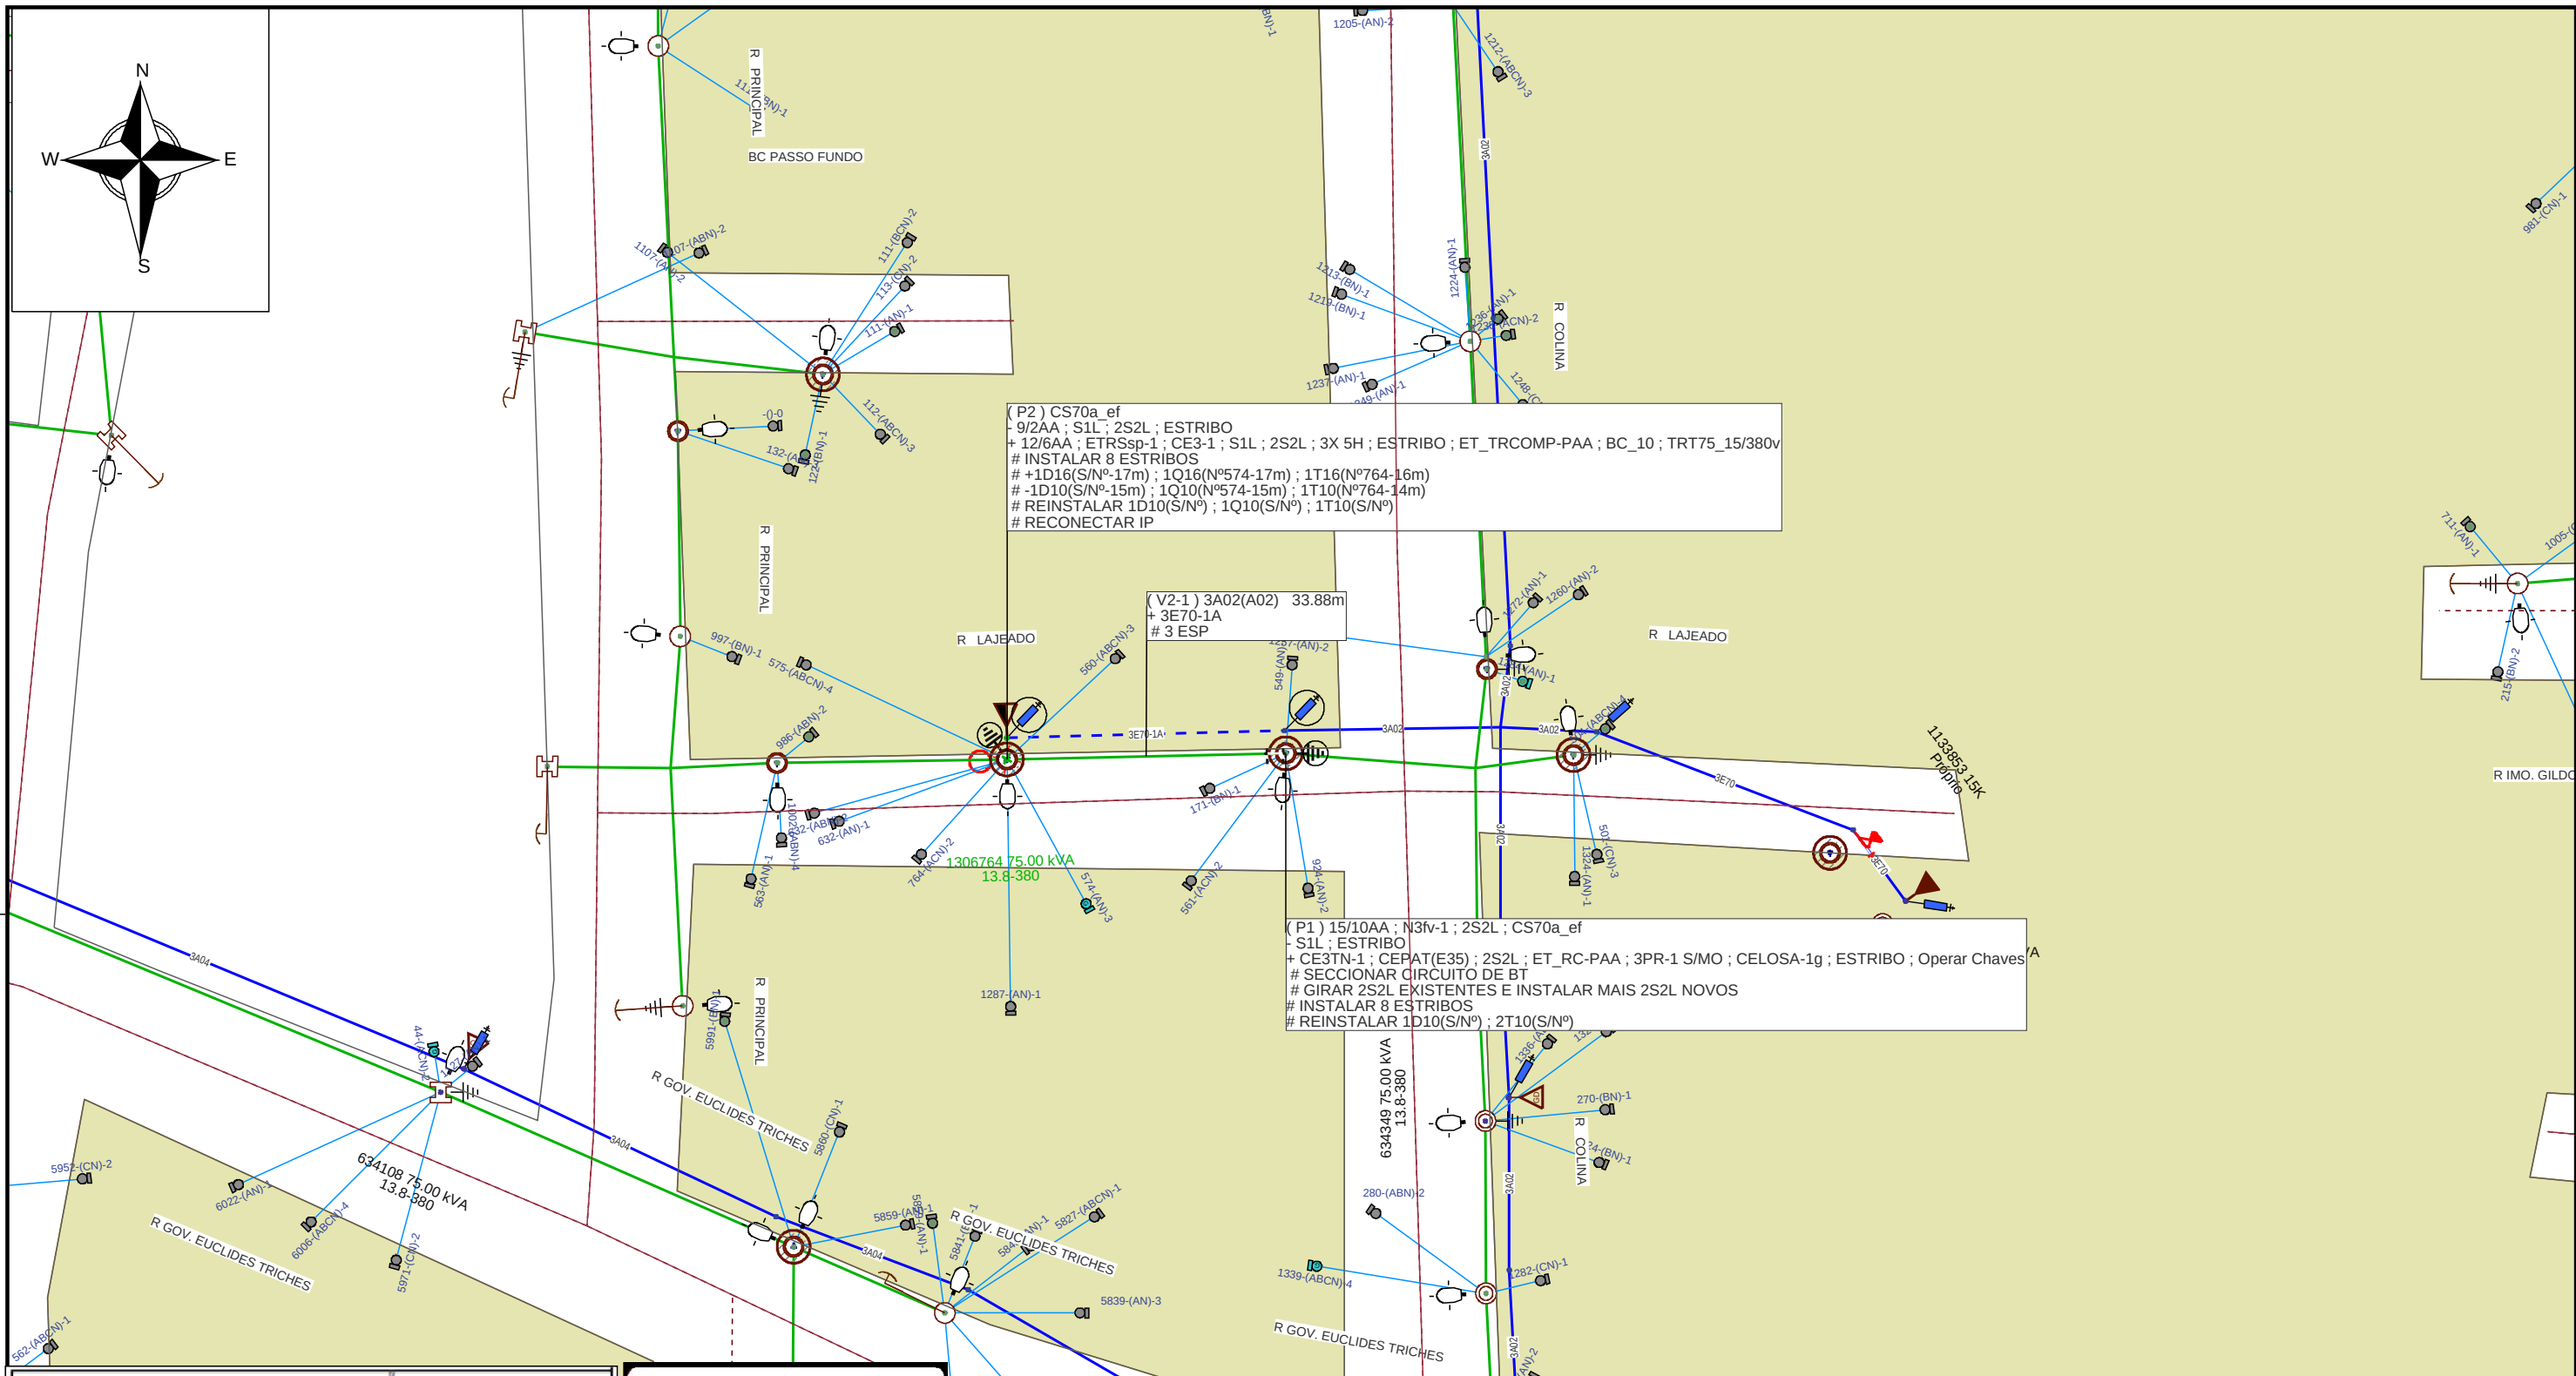

PLANO DE EXECUÇÃO					
EXECUTAR ABRA SEGUINDO OS PASSOS DE SEGURANÇA					
REALIZAR OBRA COM LINHA VIVA EM P1. PARA BT, DESLIGAR TR ABAIXO. RECLASSIFICAR POSTE DO P2.					
Ação	Equipamento	Número	Clientes	Duração	CHI
Desligar	Transformador	6954577	118	4	472
					0
Linha Viva?		Sim	CHI TOTAL		472
☐ Poste novo a ser instalado (quando indicado em planta)					

FeedBack Para Fábrica de Projetos

Planeje
Use
Teste
Sinalize
Aterre

Priscila Braganhol
Gerência de Processos de Obras e Manutenção | DROP
Técnico de Análise e Projetos
CFT: 02909484017

Gerência de Obras e Manutenção
Município: Caxias do Sul

Cliente: RGE SUL DISTRIBUIDORA DE ENERGIA S.A
Obra: Plano Sobrecarga 2026
Endereço: R LAJEADO, 561 - CAXIAS DO SUL

Responsável Técnico:

Eng. Ederson Paulo Vogel
CREA: RS135794 ART: 10911826

Escala: 1:800
Classe de isolamento:
15kV
Projetista: Priscila B.

Data: 29/12/2025
AL: unset
Projeto: 000007951720

Nota:
000006954577
Folha 1
Levantador: Marcio Bedin