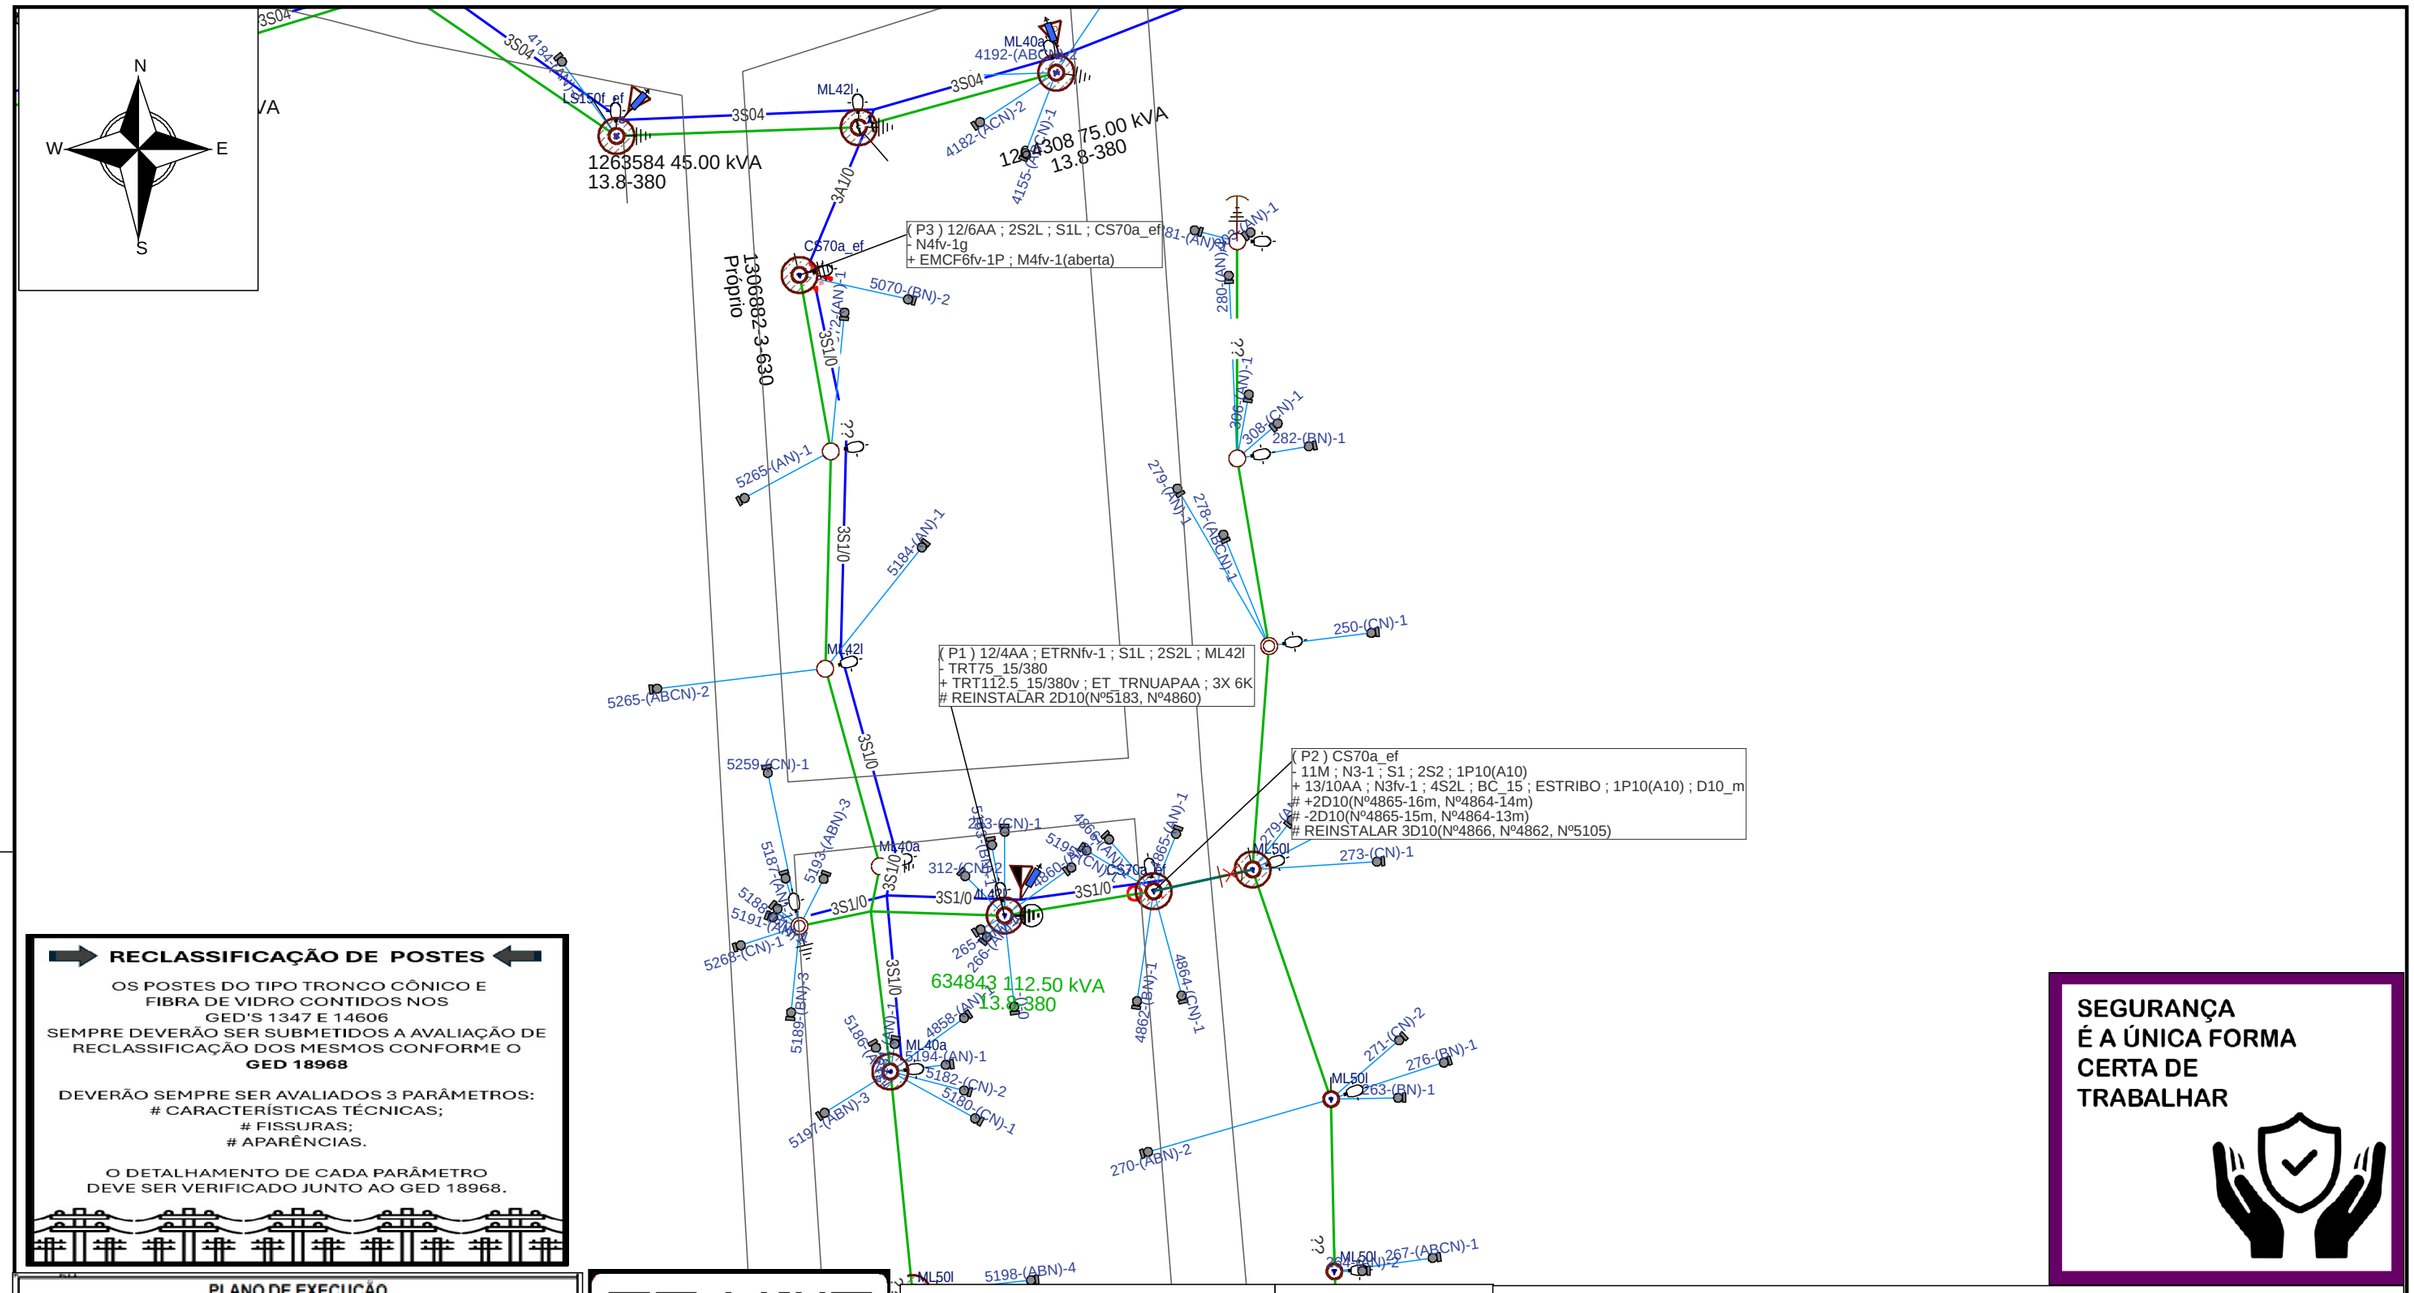

RECLASSIFICAÇÃO DE POSTES

OS POSTES DO TIPO TRONCO CÔNICO E FIBRA DE VIDRO CONTIDOS NOS GED'S 1347 E 14606 SEMPRE DEVERÃO SER SUBMETIDOS A AVALIAÇÃO DE RECLASSIFICAÇÃO DOS MESMOS CONFORME O **GED 18968**

DEVERÃO SEMPRE SER AVALIADOS 3 PARÂMETROS:
CARACTERÍSTICAS TÉCNICAS;
FISSURAS;
APARÊNCIAS.

O DETALHAMENTO DE CADA PARÂMETRO DEVE SER VERIFICADO JUNTO AO GED 18968.

PLANO DE EXECUÇÃO

ABRIR CAVAS, PREPARAR OS PONTOS DA OBRA.
REALIZAR ATIVIDADES COM LINHA VIVA NO P3 .
SE POSSIVEL EXECUTAR EM CONJUTO NOTA 300001072393, 300001036648
7144073, 6699874 E 30000894406.

REALIZAR TODAS AS ATIVIDADES SEGUINDO AS NORMAS DE SEGURANÇA.
ESSE PROJETO SÓ PODE SER ALTERADO POR SOLICITAÇÃO DE DI.

Ação	Equipamento	Número	Clientes	Duração	CHI
Abrir	Transformador	634843	90	4	360
Linha Viva?		Sim	CHI TOTAL		360

◯ Poste novo a ser instalado (quando indicado em planta)

FeedBack Para Fábrica de Projetos

Planeje
Use
Teste
Sinalize
Aterre

Gabriel Vergani
Gerência de Processos de Obras e Manutenção | DROP
Técnico de Análise e Projetos
CFT: 040.224.970-41

SEGURANÇA É A ÚNICA FORMA CERTA DE TRABALHAR

CPFL ENERGIA

Gerência de Obras e Manutenção

Município: Caxias do Sul

Cliente: RGE SUL DISTRIBUIDORA DE ENERGIA S/A

Obra: Plano Sobrecarga 2026

Endereço: R QUINZE LOT FAZ SOUZA, FAZ SOUZA, CAXIAS DO SUL RS

Responsável Técnico:
Eng. Ederson Paulo Vogel
CREA: RS135794 ART: 10911826

Escala: 1:1100	Data: 16/02/2026	Nota: 000006960542
Classe de isolação: 15kV	AL: CXD21	Folha 1
Projetista: Gabriel Vergani	Projeto: 000007981917	Levantador: Alessandro Severo de Oliveira