


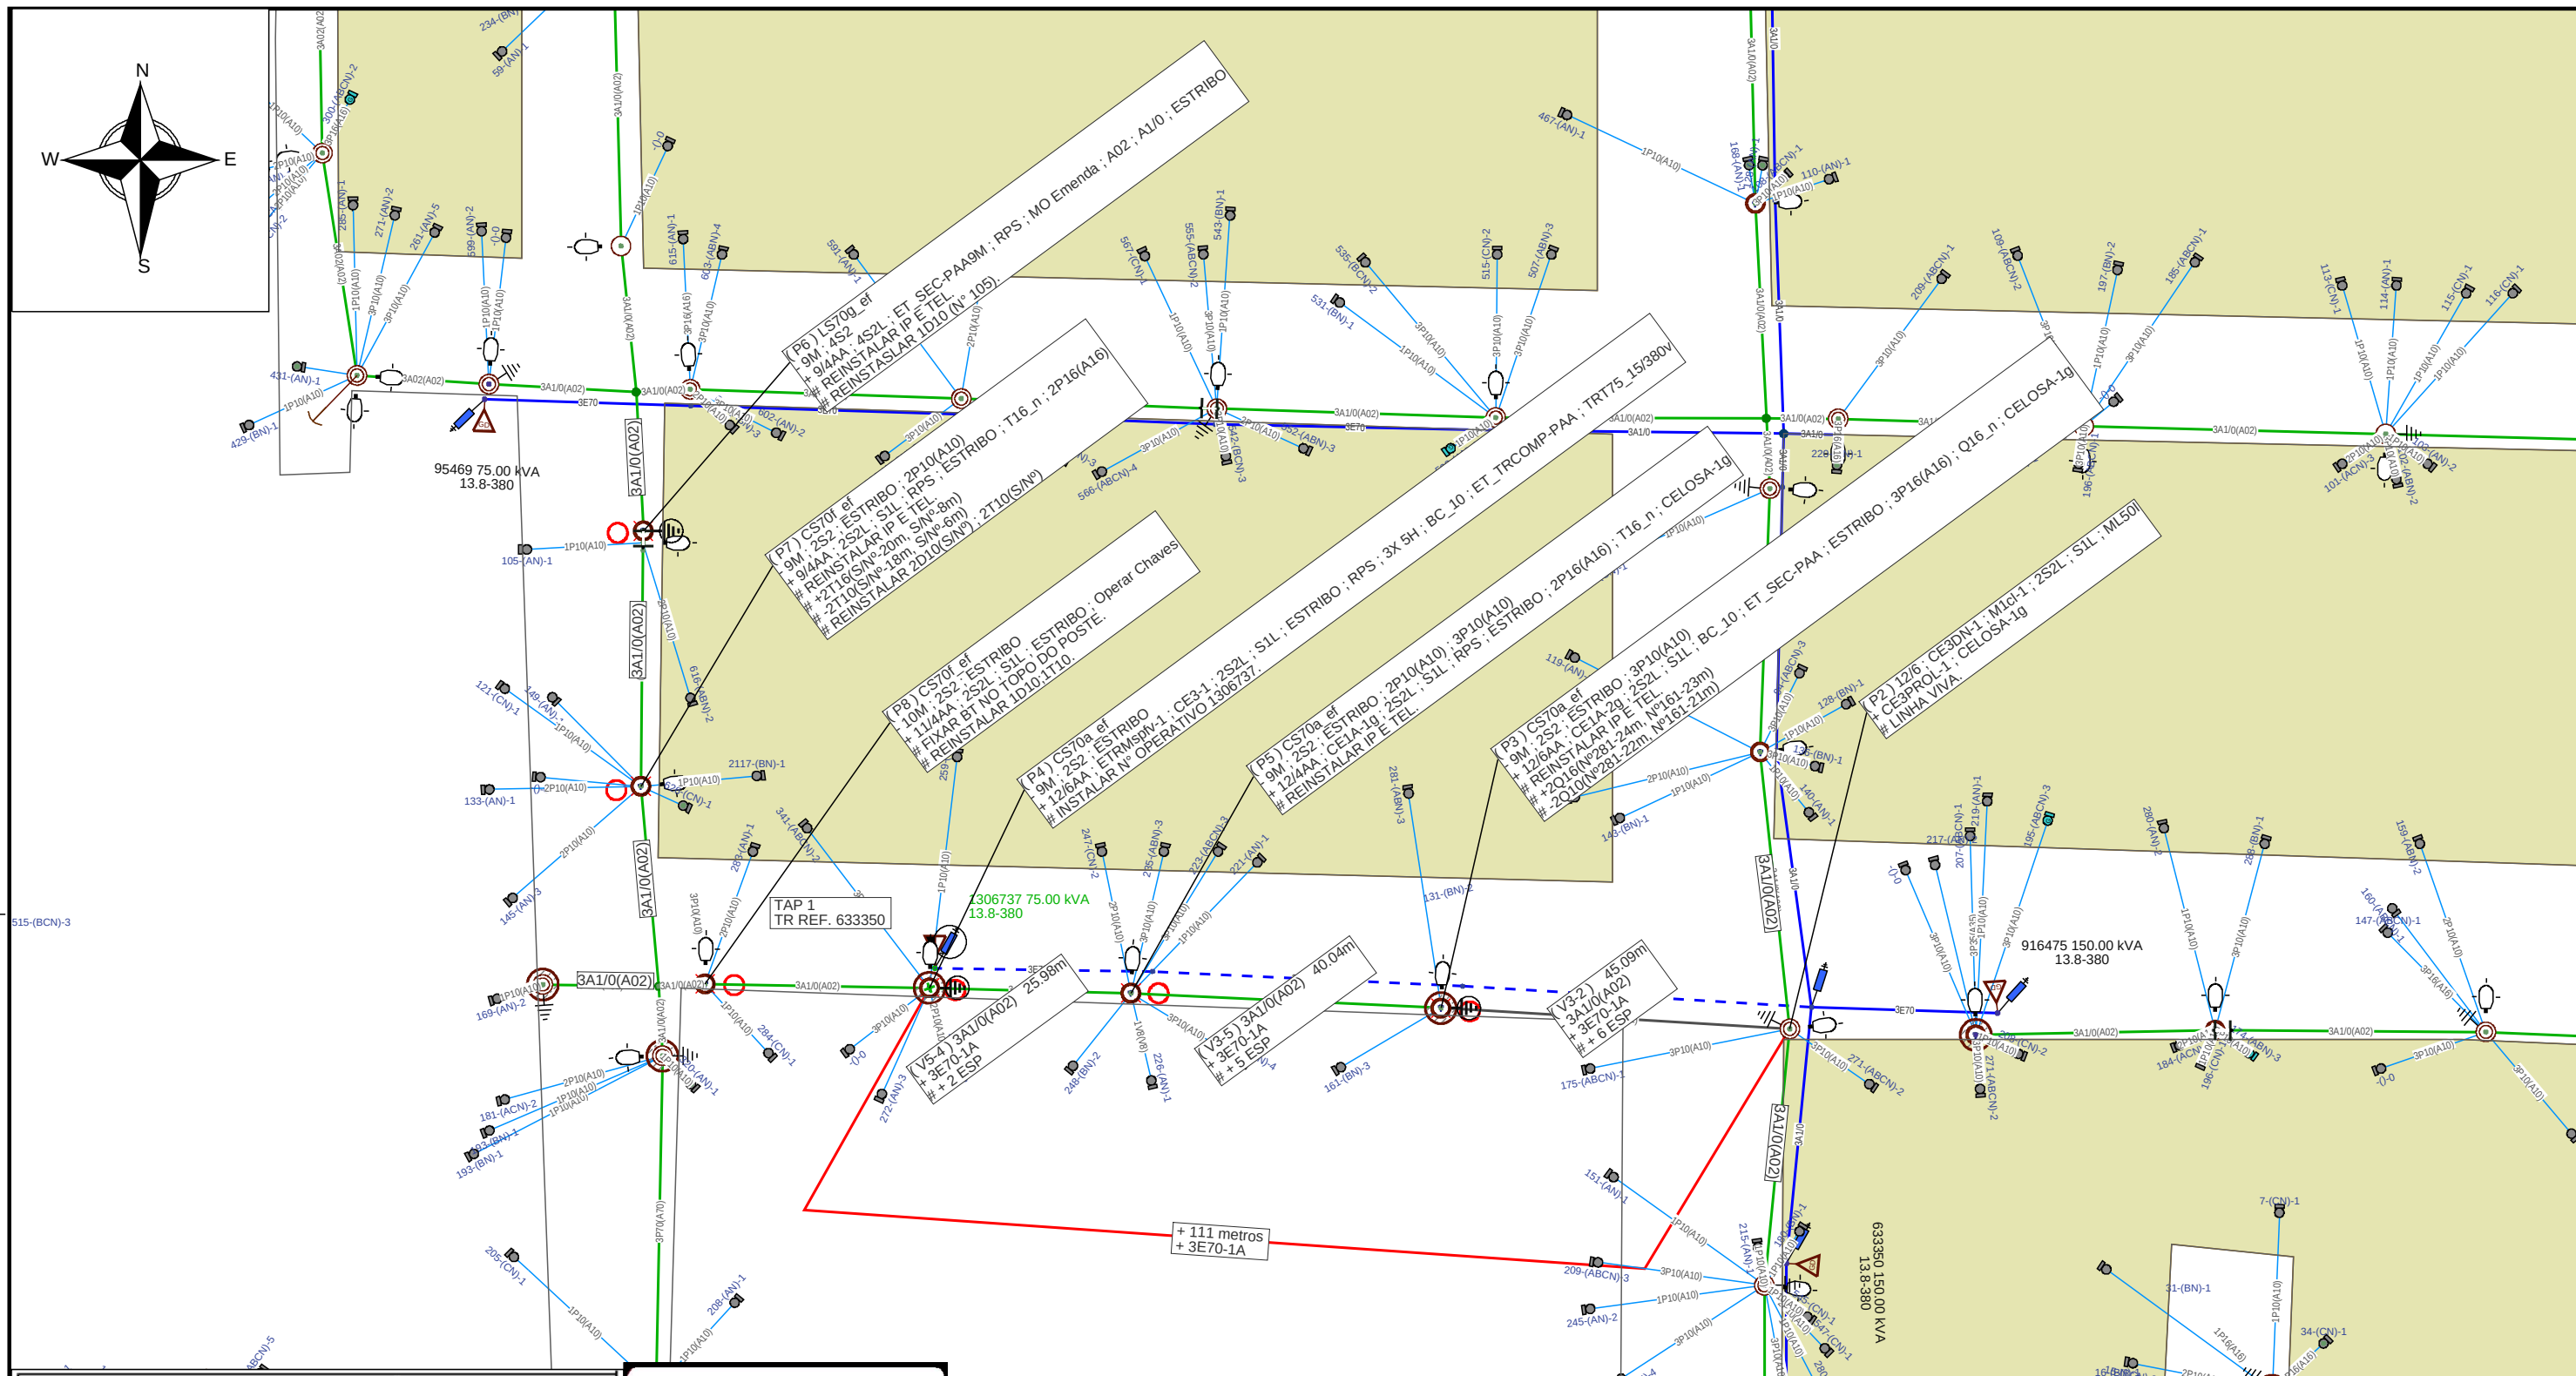

PLANO DE EXECUÇÃO

Executar a obra seguindo todos os passos de segurança!

Desligar Transformador (633350)

Substituir postes e derivar rede primária conforme croqui.
Para intervir no P2, utilizar linha viva na rede primária.

Ação	Equipamento	Número	Cientes	Duração	CHI
Desligar	Transformador	633350	211	5	1055


Linha Viva? **Sim** CHI TOTAL **1055**

RECLASSIFICAR POSTES EM BOM ESTADO GED 18968

Poste novo a ser instalado (quando indicado em planta)



FeedBack Para Fábrica de Projetos

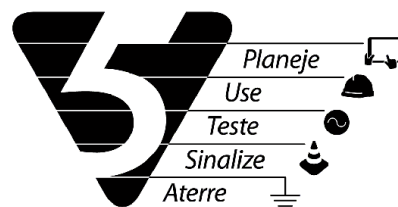

Renan Ramirez Moyses

Renan Ramirez Moyses

Gerência de Processos de Obras e Manutenção | DROP

Técnico de Análise e Projetos

CFT: 041.013.340-05



Gerência de Obras e Manutenção

Município: Caxias do Sul

Cliente: CPFL RGE

Obra: Plano Sobrecarga 2026

Endereço: R JANICE CANDIDO DOS SANTOS,, 195

Responsável Técnico:

Eng. Ederson Paulo Vogel
CREA: RS135794 ART: 10911826

Escala: 1:850

Classe de isolamento:

15kV

Projetista: Renan R. Moyses

Data: 20/02/2026

AL: CXC15

Projeto: 000007984408

Nota:
000006960622

Folha 1

Levantador: Reinholdo Brulinger