


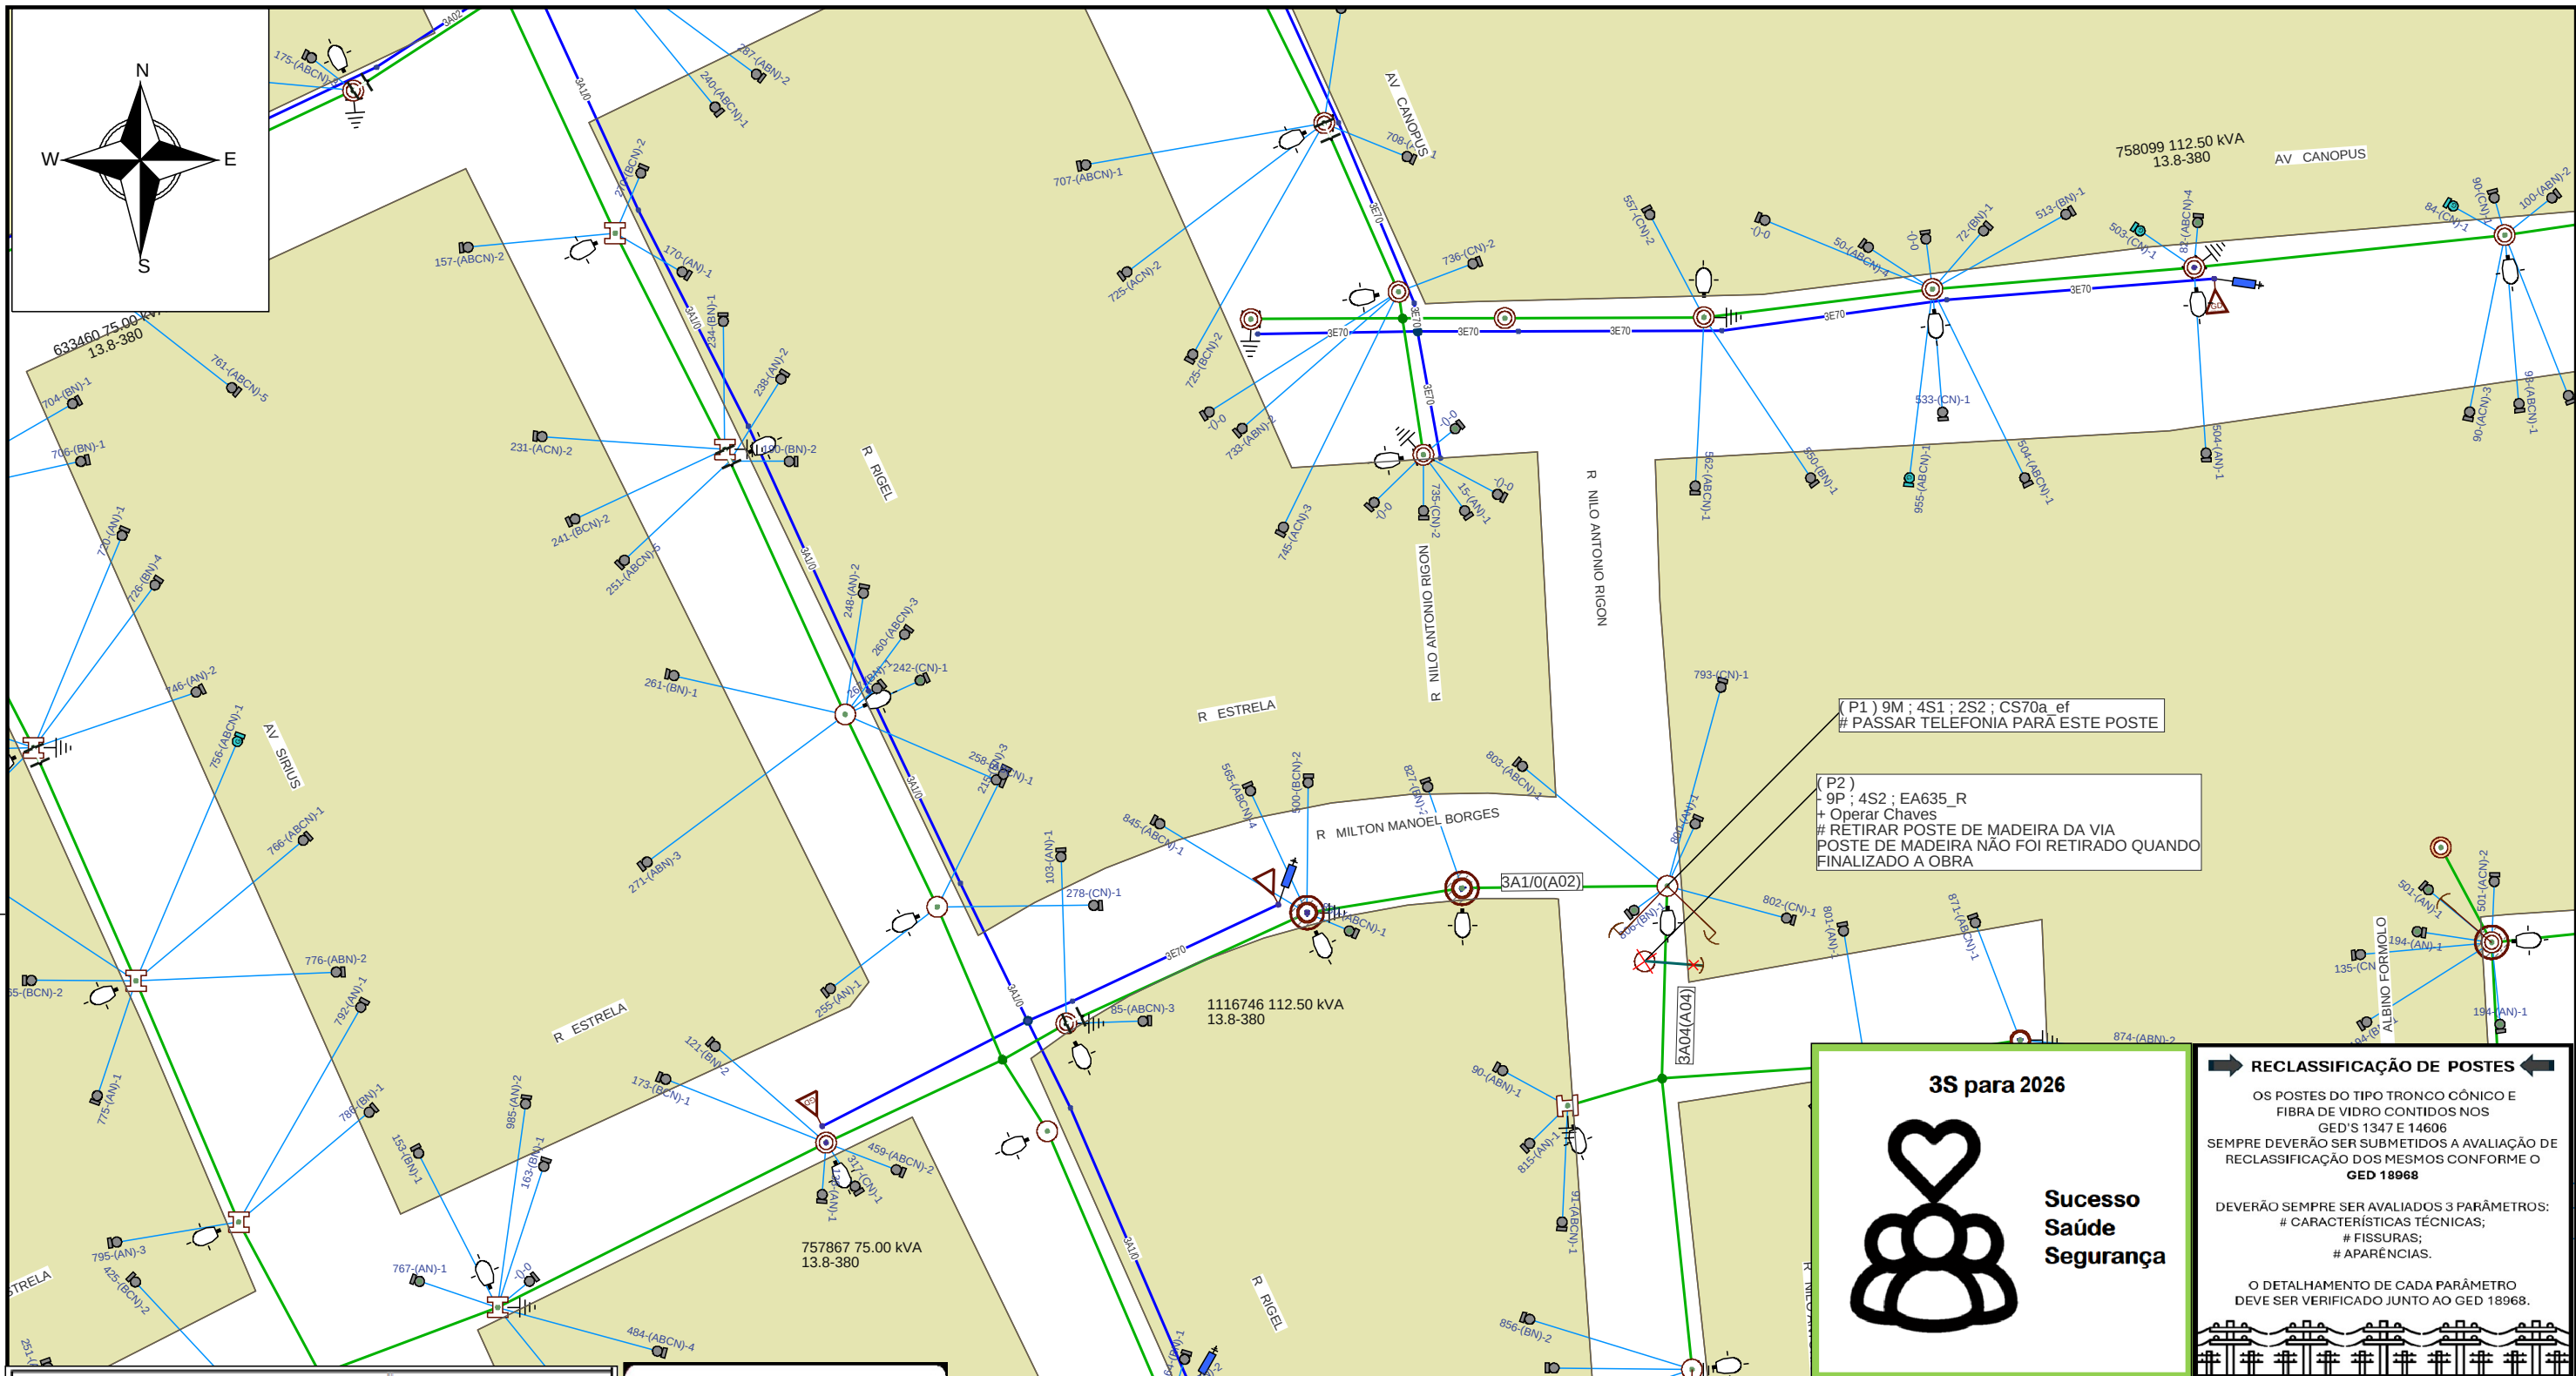

3S para 2026

**Sucesso
Saúde
Segurança**

RECLASSIFICAÇÃO DE POSTES

OS POSTES DO TIPO TRONCO CÔNICO E FIBRA DE VIDRO CONTIDOS NOS GED'S 1347 E 14606 SEMPRE DEVERÃO SER SUBMETIDOS A AVALIAÇÃO DE RECLASSIFICAÇÃO DOS MESMOS CONFORME O GED 18968

DEVERÃO SEMPRE SER AVALIADOS 3 PARÂMETROS:
CARACTERÍSTICAS TÉCNICAS;
FISSURAS;
APARÊNCIAS.

O DETALHAMENTO DE CADA PARÂMETRO DEVE SER VERIFICADO JUNTO AO GED 18968.

PLANO DE EXECUÇÃO					
Executar a obra seguindo todos os passos de segurança!					
SUBSTITUIR POSTES INDICADOS EM PLANTA SEGUINDO OS PROCEDIMENTOS DE SEGURANÇA					

FeedBack Para Fábrica de Projetos

**Planeje
Use
Teste
Sinalize
Aterre**

Breno Ardenghy
Breno Ardenghy Da Silva
Gerência de Processos de Obras e Manutenção | DROP
Técnico de Análise e Projetos
CFT: 03188101074

		Gerência de Obras e Manutenção			
		Município: Caxias do Sul			
Cliente: RGE SUL DISTRIBUIDORA DE ENERGIA S.A					
Obra: Levantamento - Ofício 6971782					
Endereço: R NILO ANTONIO RIGON 793 CRUZEIRO CAXIAS DO SUL					
Responsável Técnico: Eng. Ederson Paulo Vogel CREA: RS135794 ART: 10911826		Escala: 1:800 Classe de isolamento: 15kV Projetista: BRENO ARDENGHY	Data: 25/08/2025 AL: CXG12 Projeto: 000007861290		
			Nota: 000006980481 Folha 1 Levantador REINHOLDO BRULINGER		