



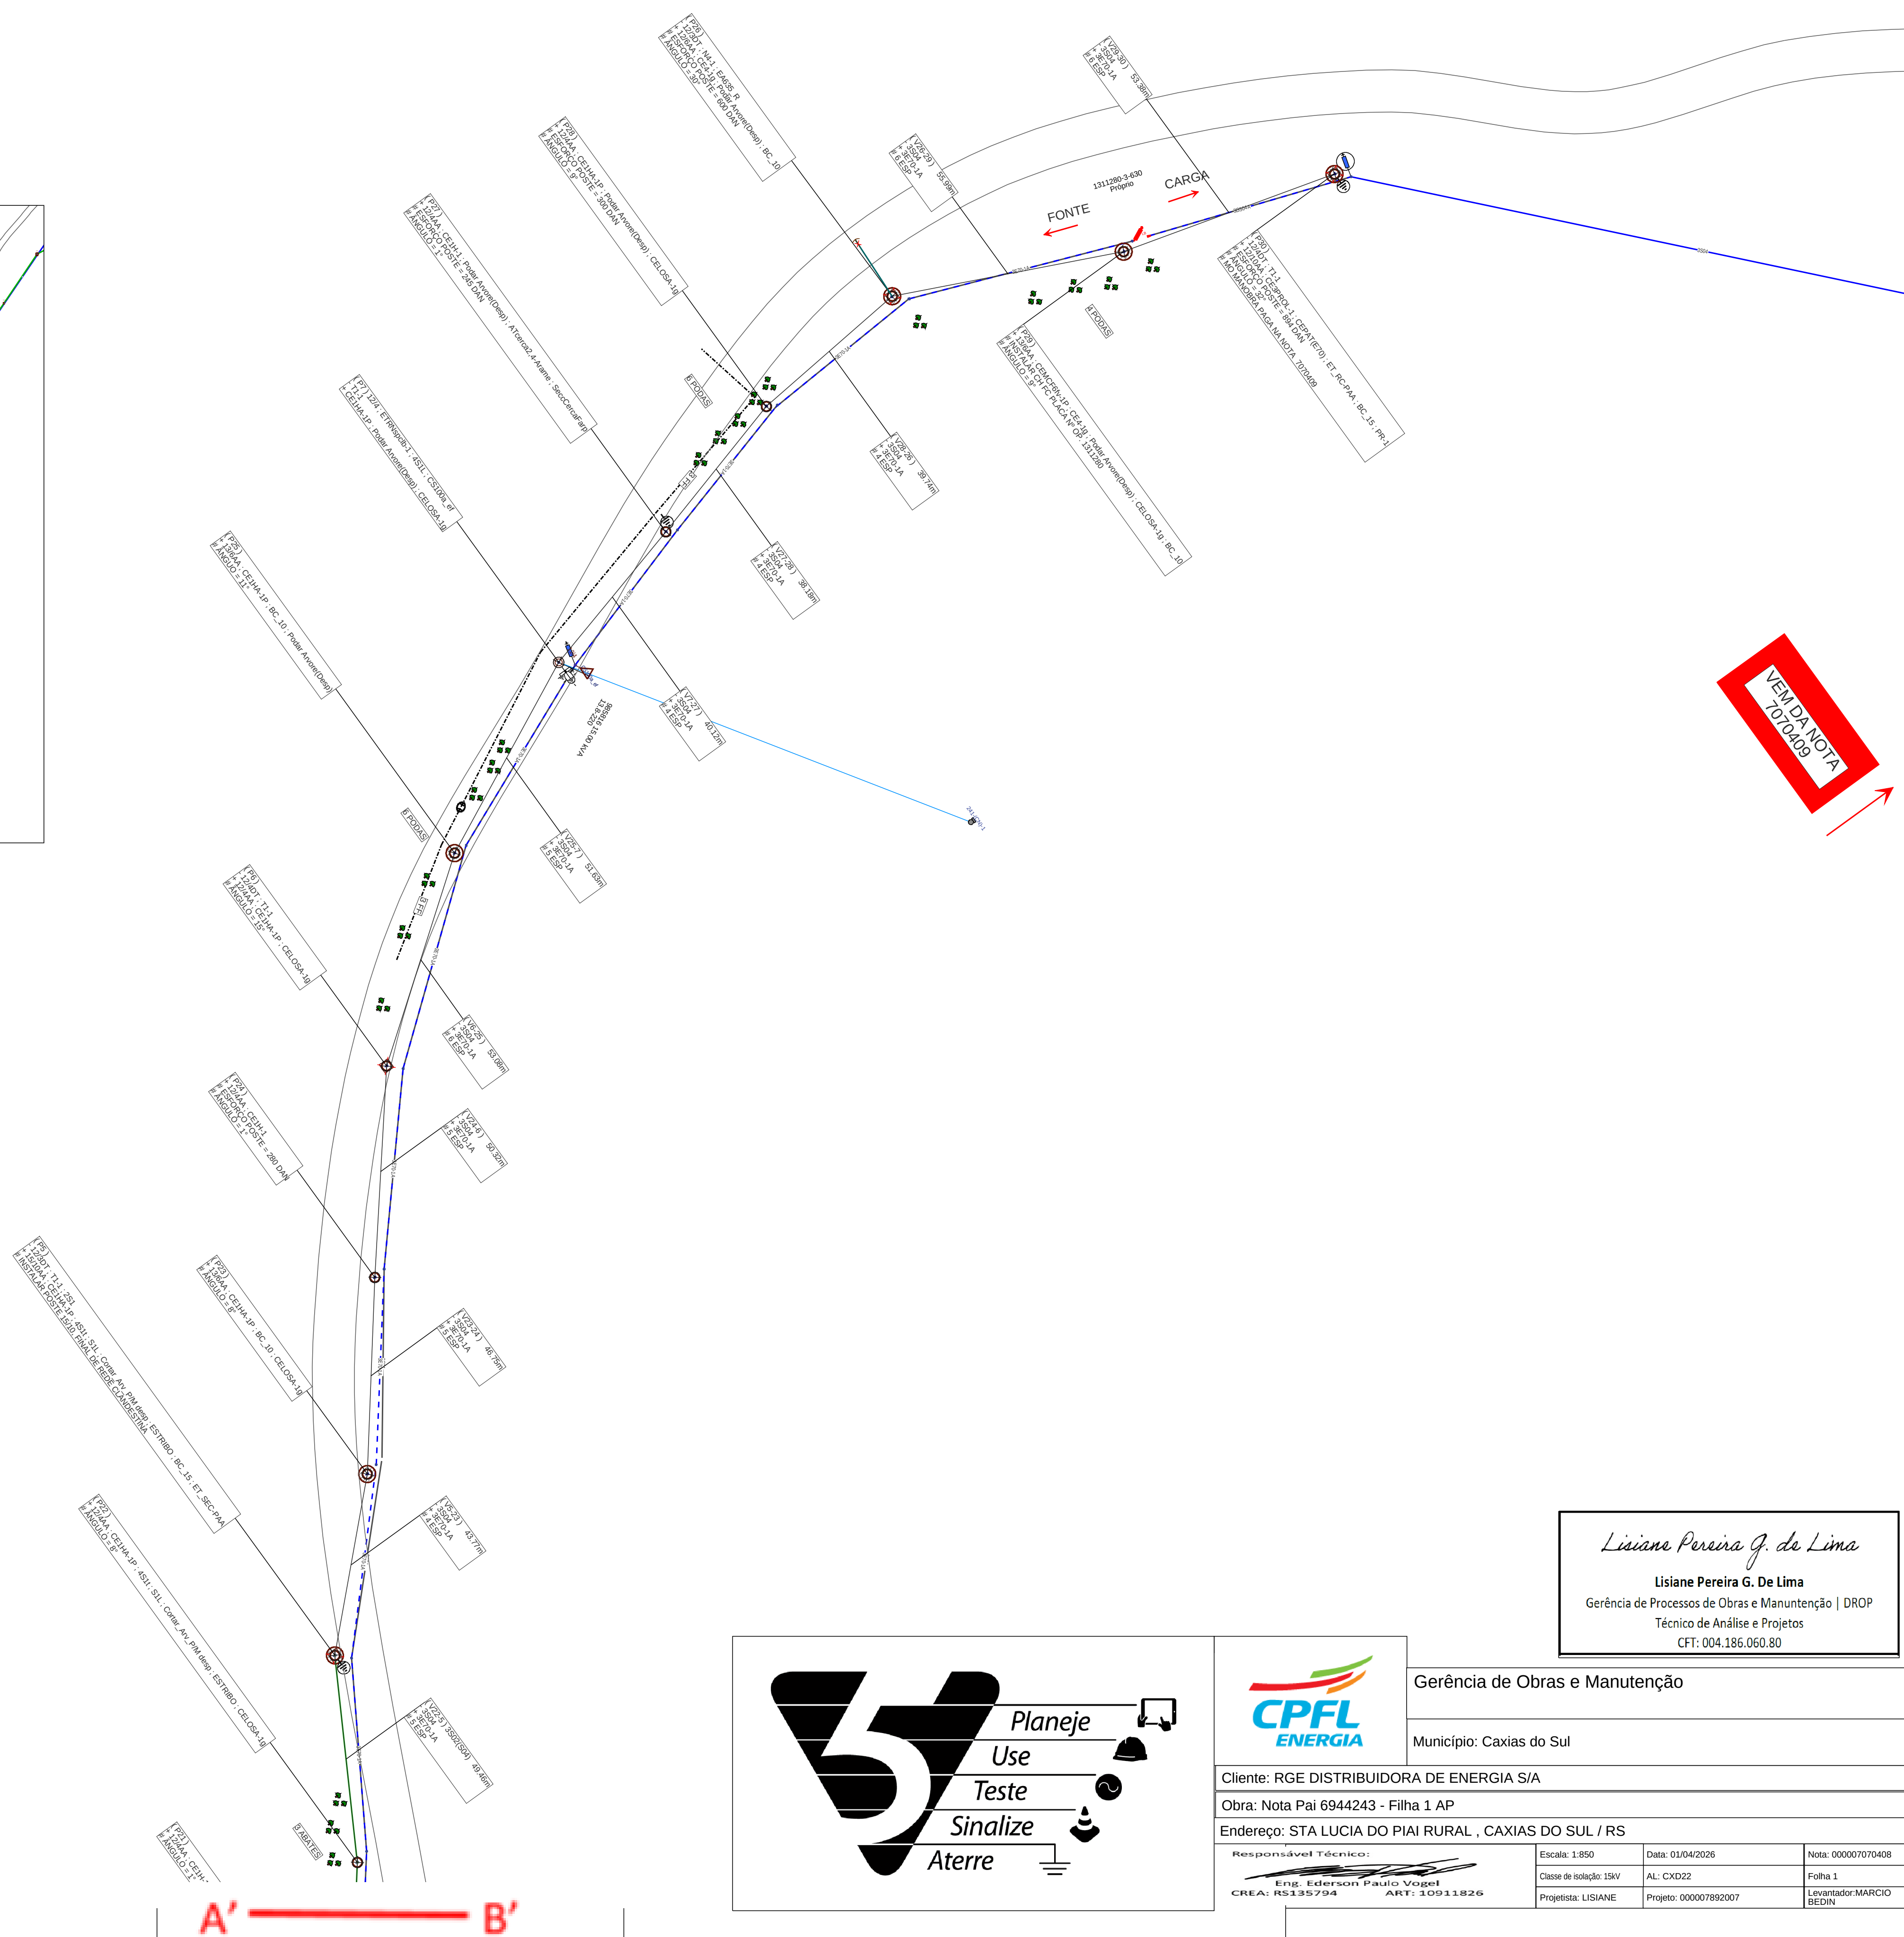


PLANO DE EXECUÇÃO					
EXECUTAR OBRA SEGUINDO OS PASSOS DE SEGURANÇA					
SEGUIR PLANO DE EXECUÇÃO DA NOTA 7070409 ; EXECUTAR EM CONJUNTO					
INSTALAR CH FACA NO P29 PARA DESLIGAMENTO DA NOTA 7070409 ; RECONDUTORAR REDE MT PARA COMPACTA					
UTILIZAR LU					

Ação	Equipamento	Número	Clientes	Duração	CHI
Ligar		608971	76	5	380
Linha Viva?		Não	CHI TOTAL		380

☐ Poste novo a ser instalado (quando indicado em planta)

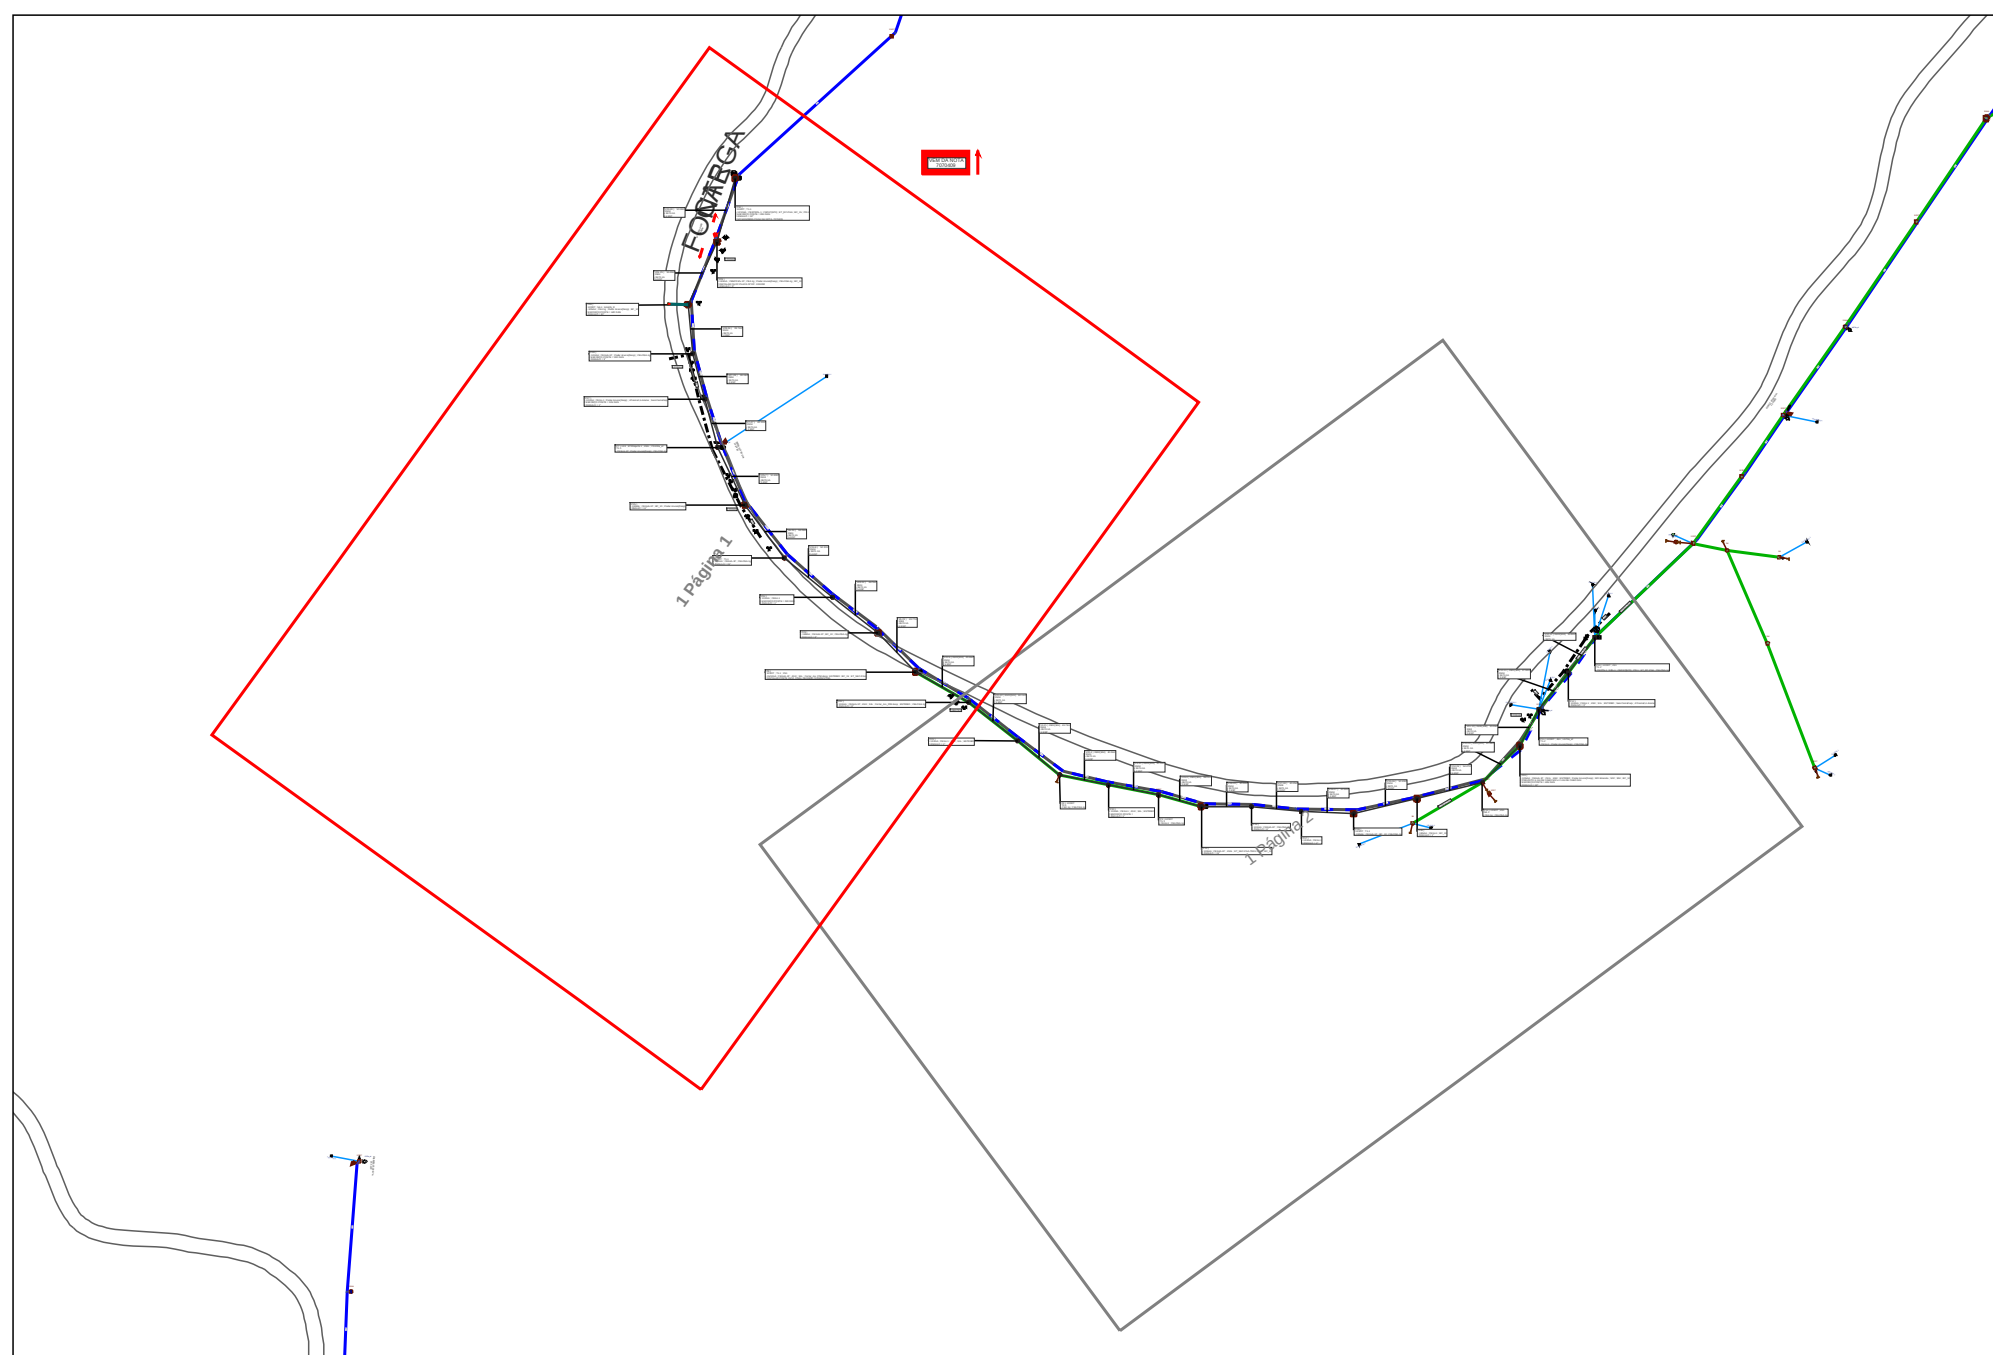

FeedBack Para Fábrica de Projetos

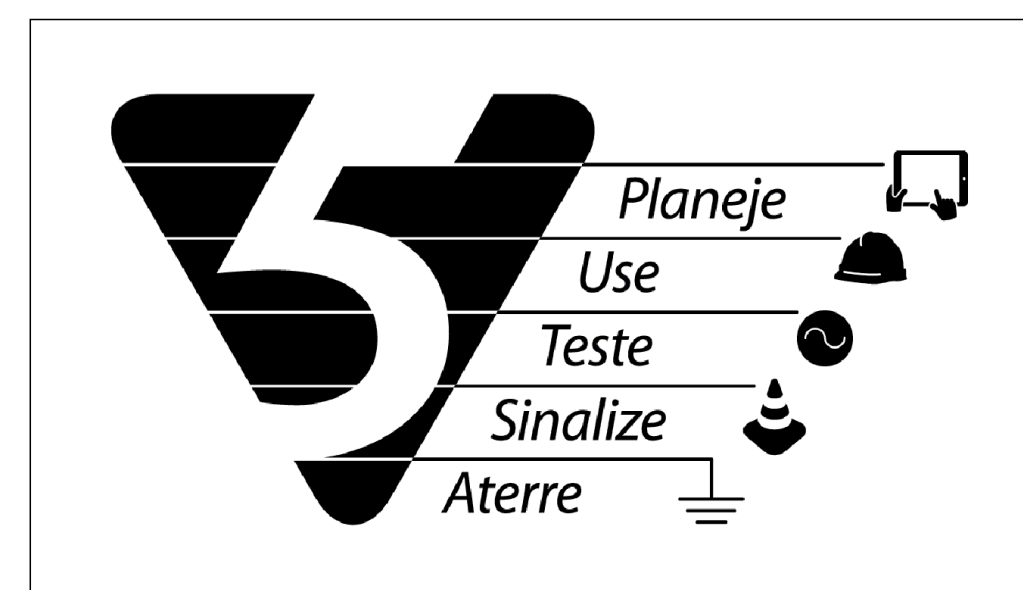

Município: Caxias do Sul

Endereço: STA LUCIA DO PIAI RURAL , CAXIAS DO SUL / RS

Eng. Ederson Paulo Vogel
CREA: RS135794 ART: 10911826

De'Anna, LIGANE

000007000007

Levantador: MARCIO



Lisiane Pereira J. de Lima

Lisiane Pereira G. De Lima

Gerência de Processos de Obras e Manutenção | DROP



Técnico de Análise e Projetos

CFT: 004.186.060.80

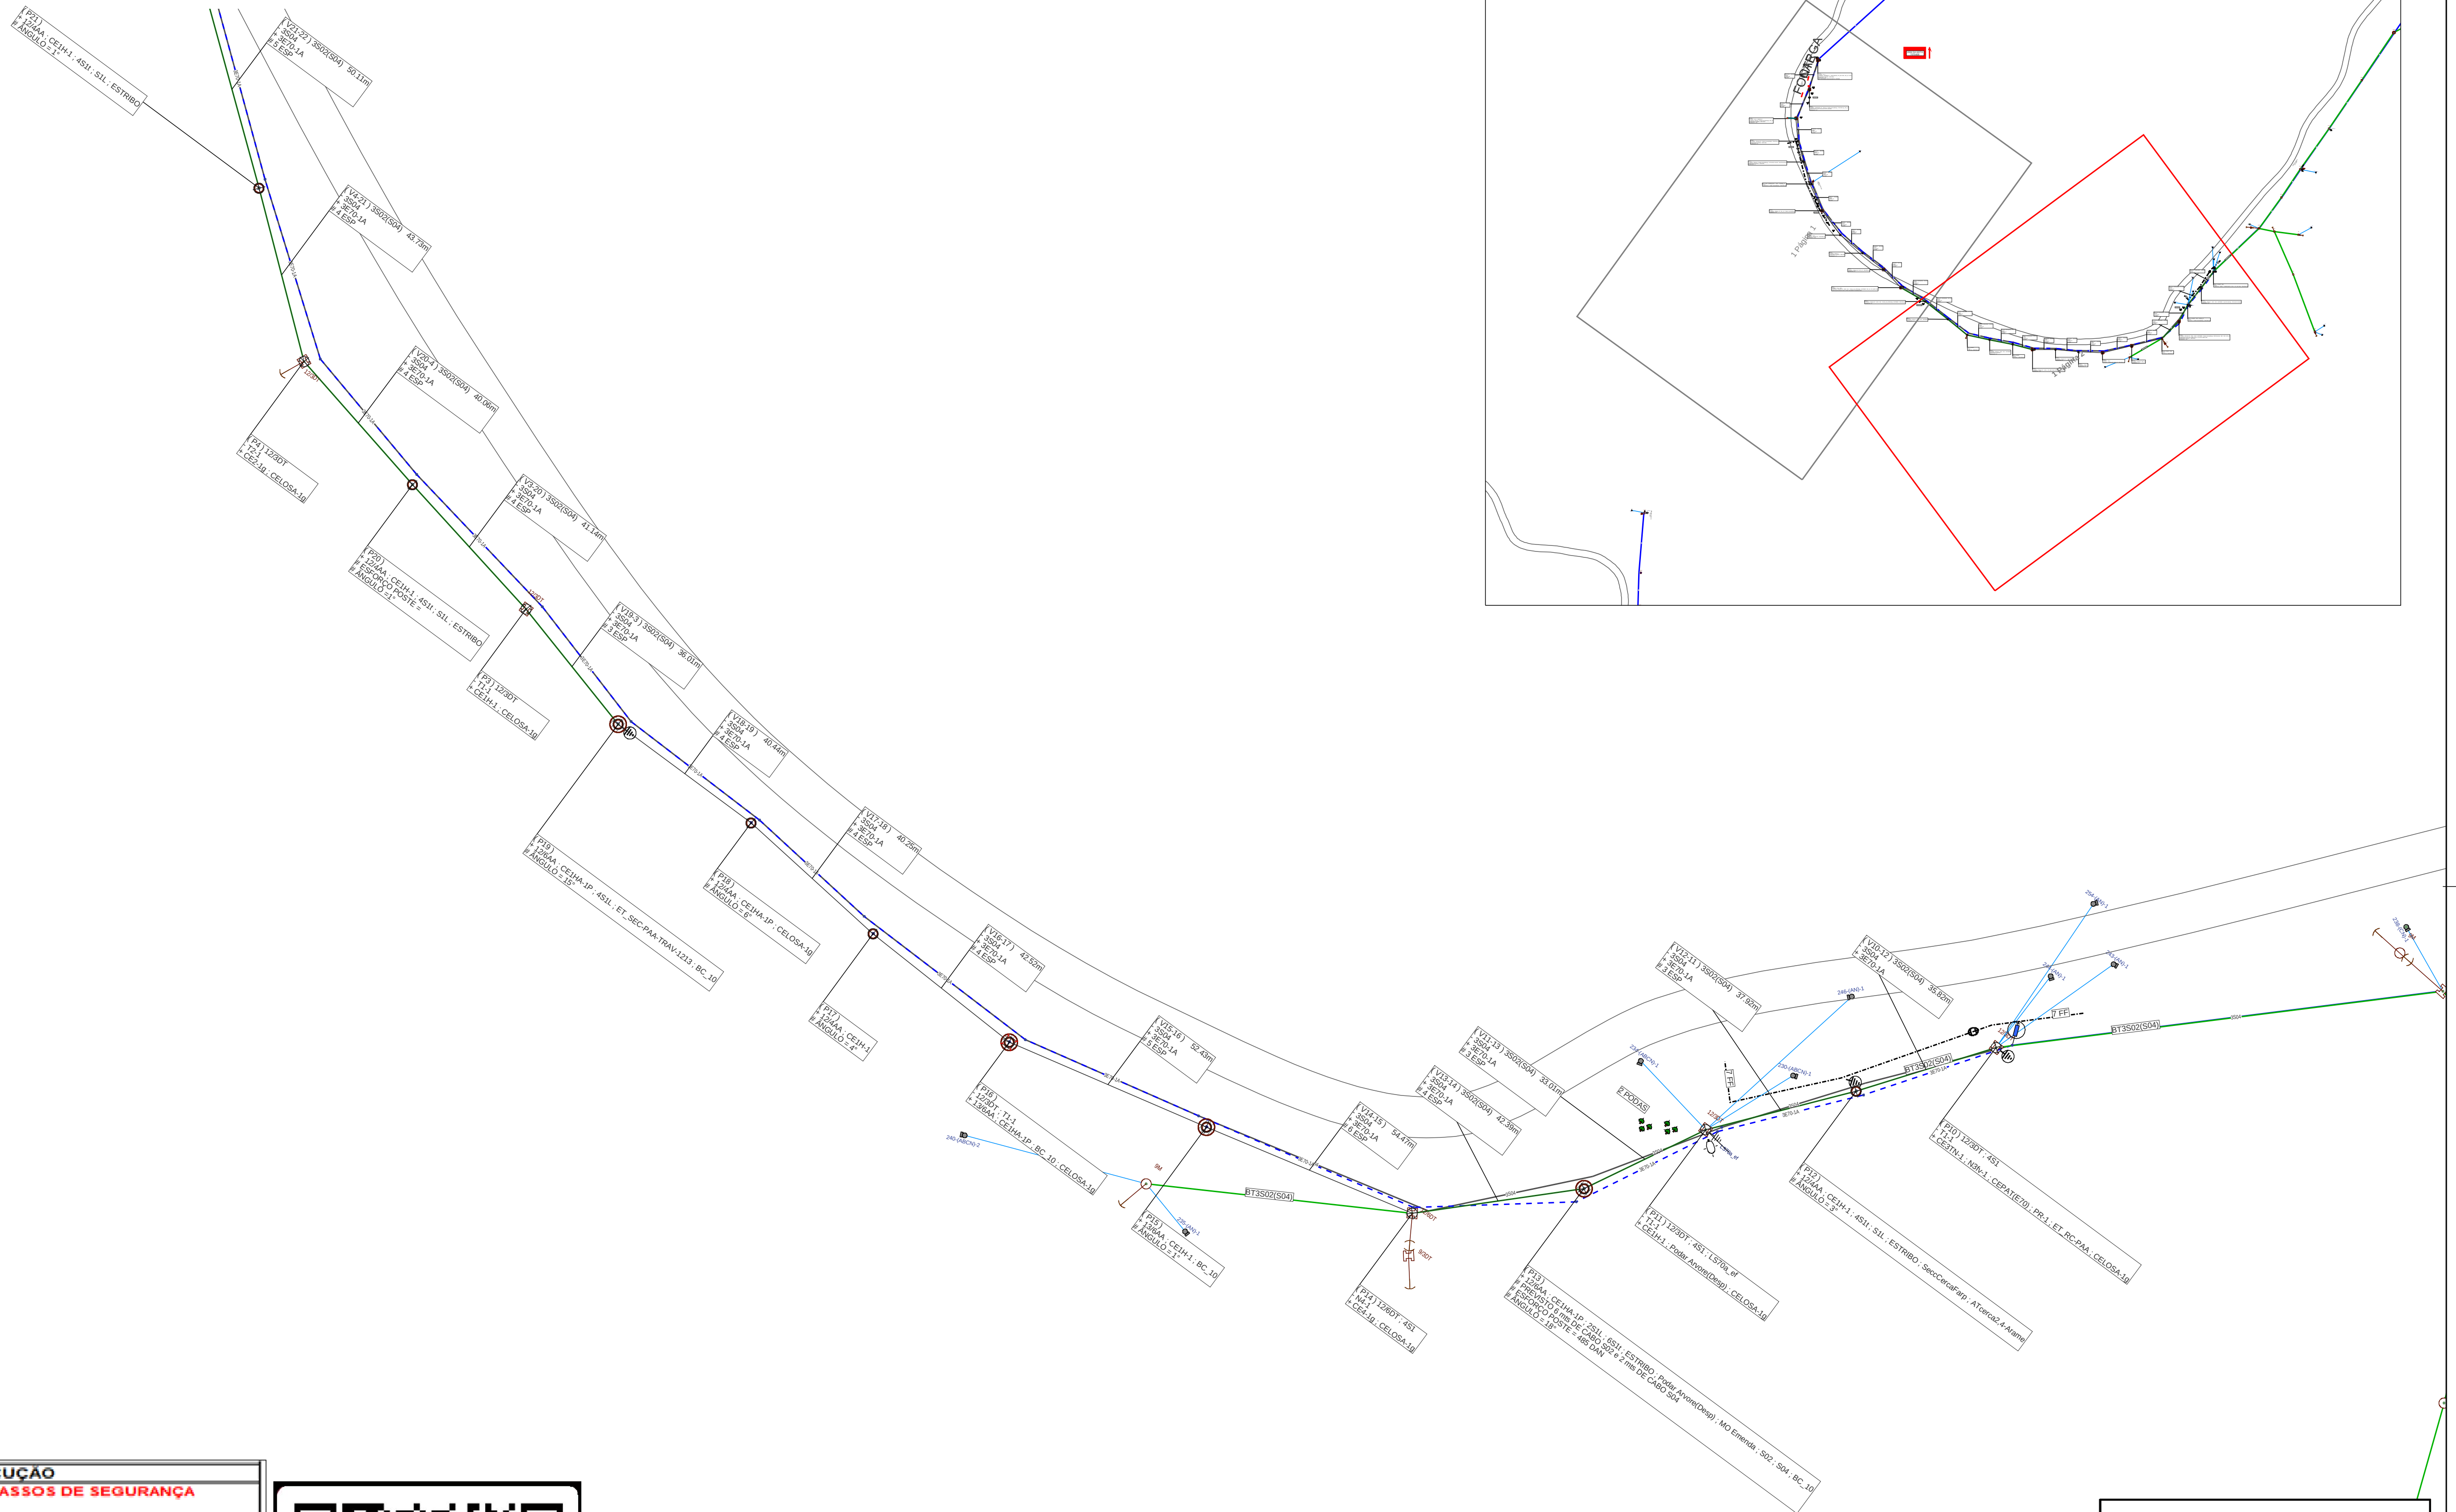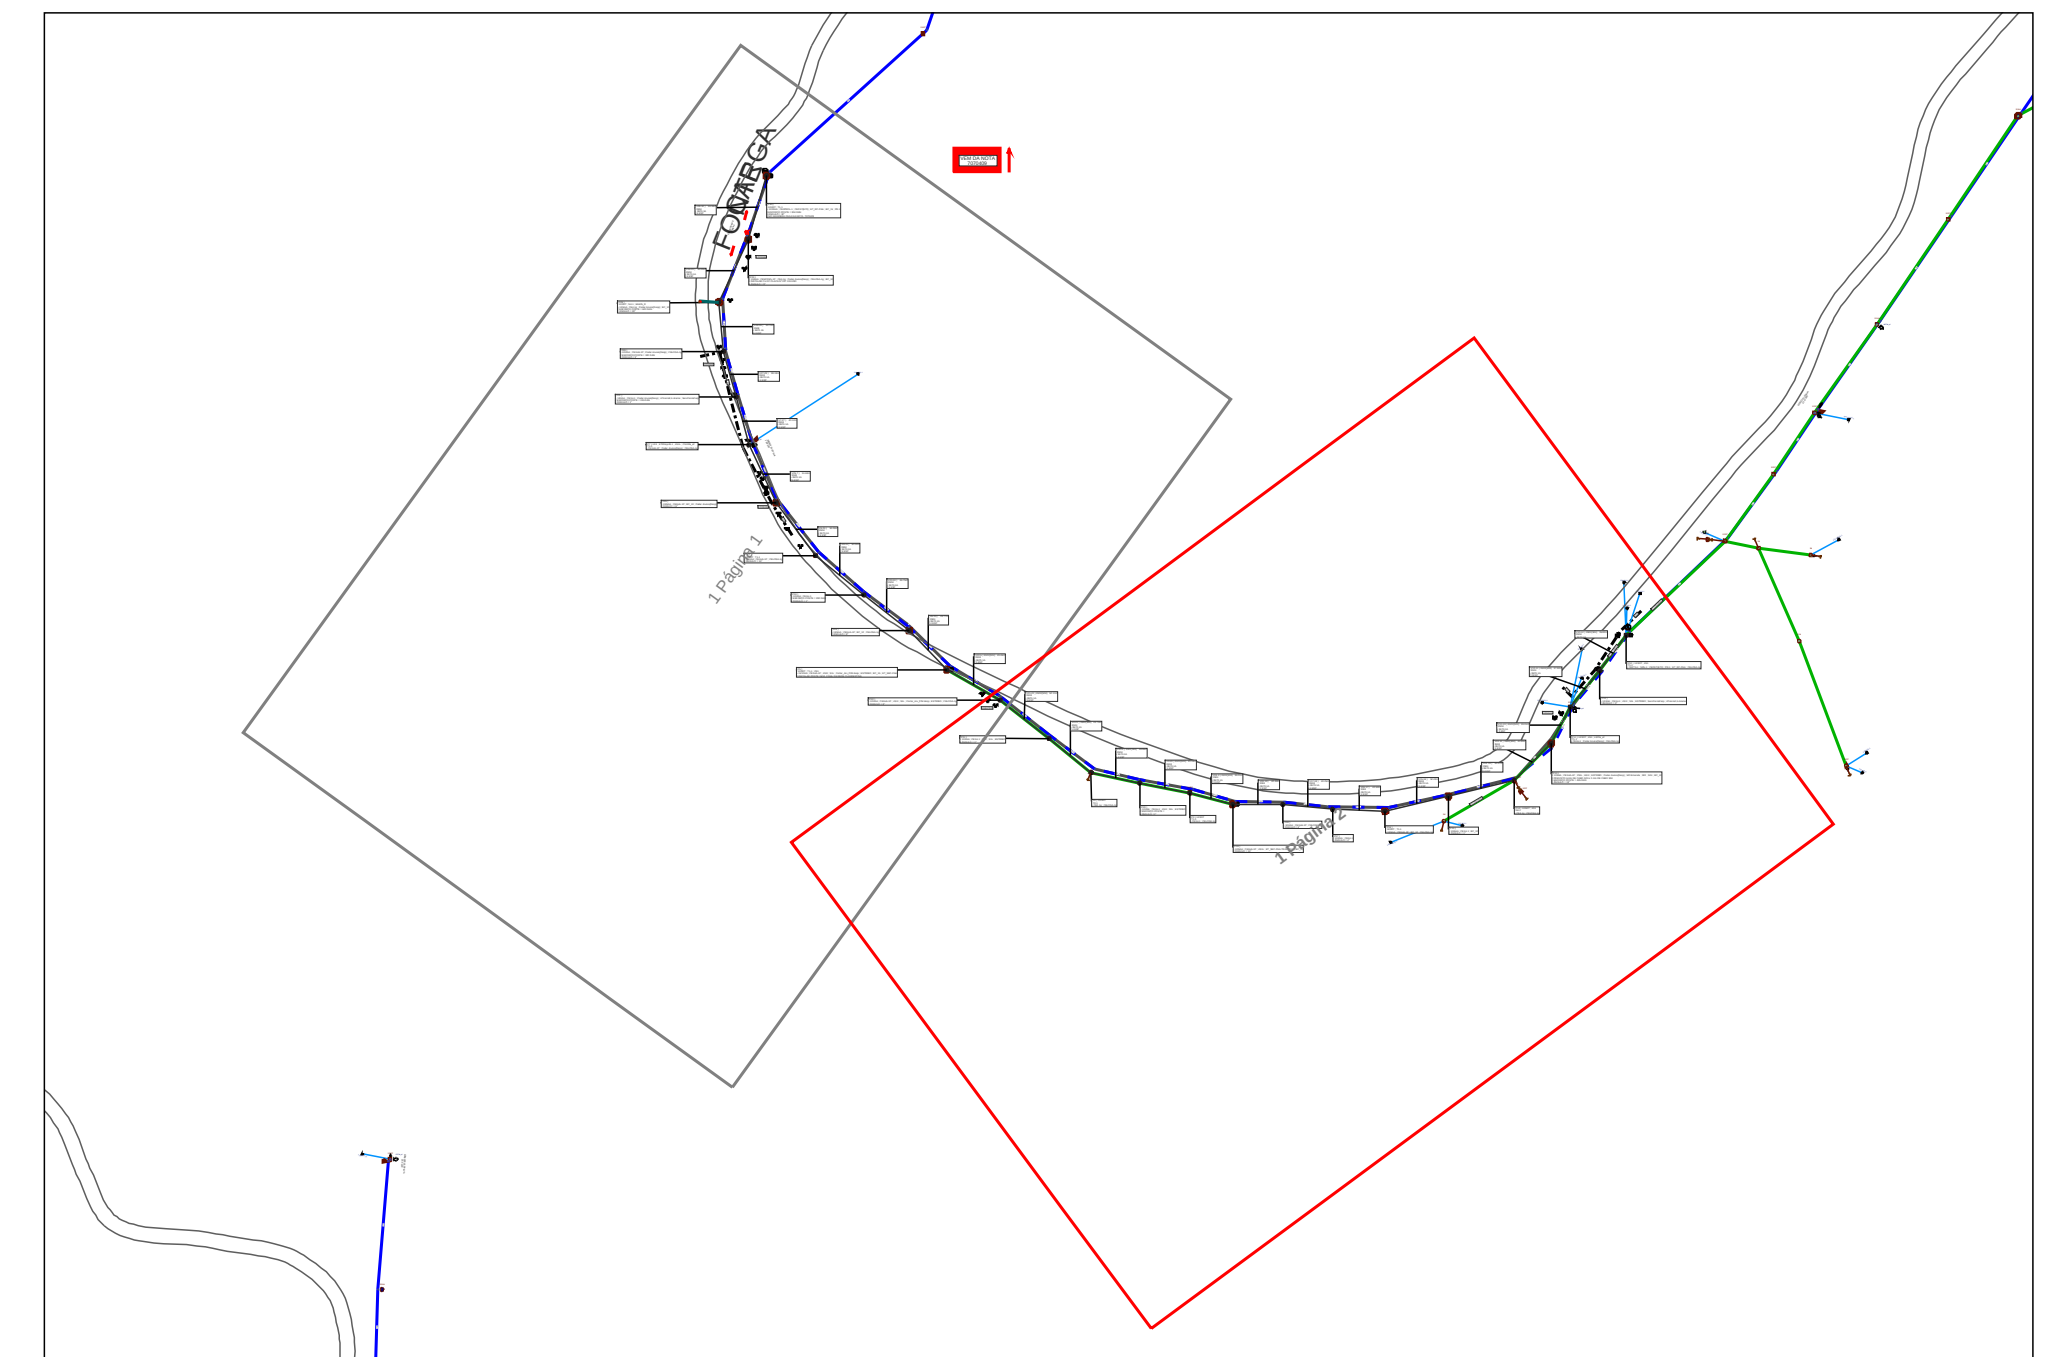

EXECUTAR OBRA SEGUINDO OS PASSOS DE SEGURANÇA

UTILIZAR LU

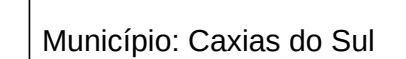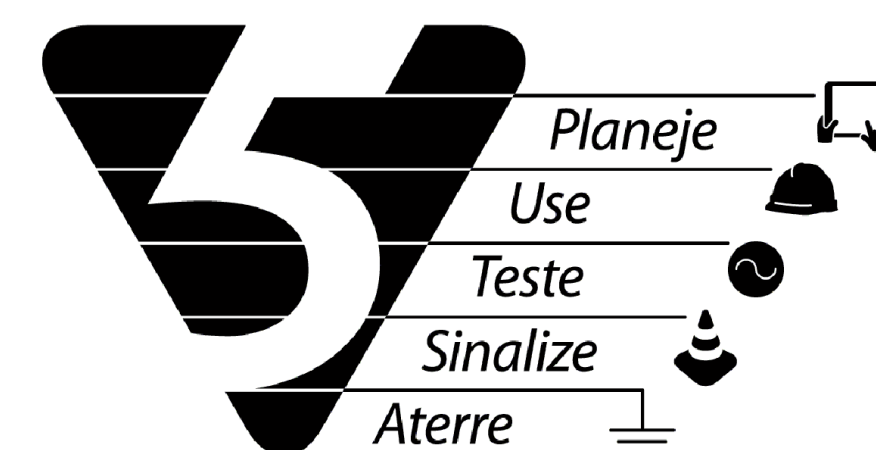☐ Poste novo a ser instalado (quando indicado em planta)

Classe de isolamento: 15kV	AL: CXD22	Folha 2
Projetista: LISIANE	Projeto: 000007892007	Levantador: MARCIO

CFT: 004.186.060.80