


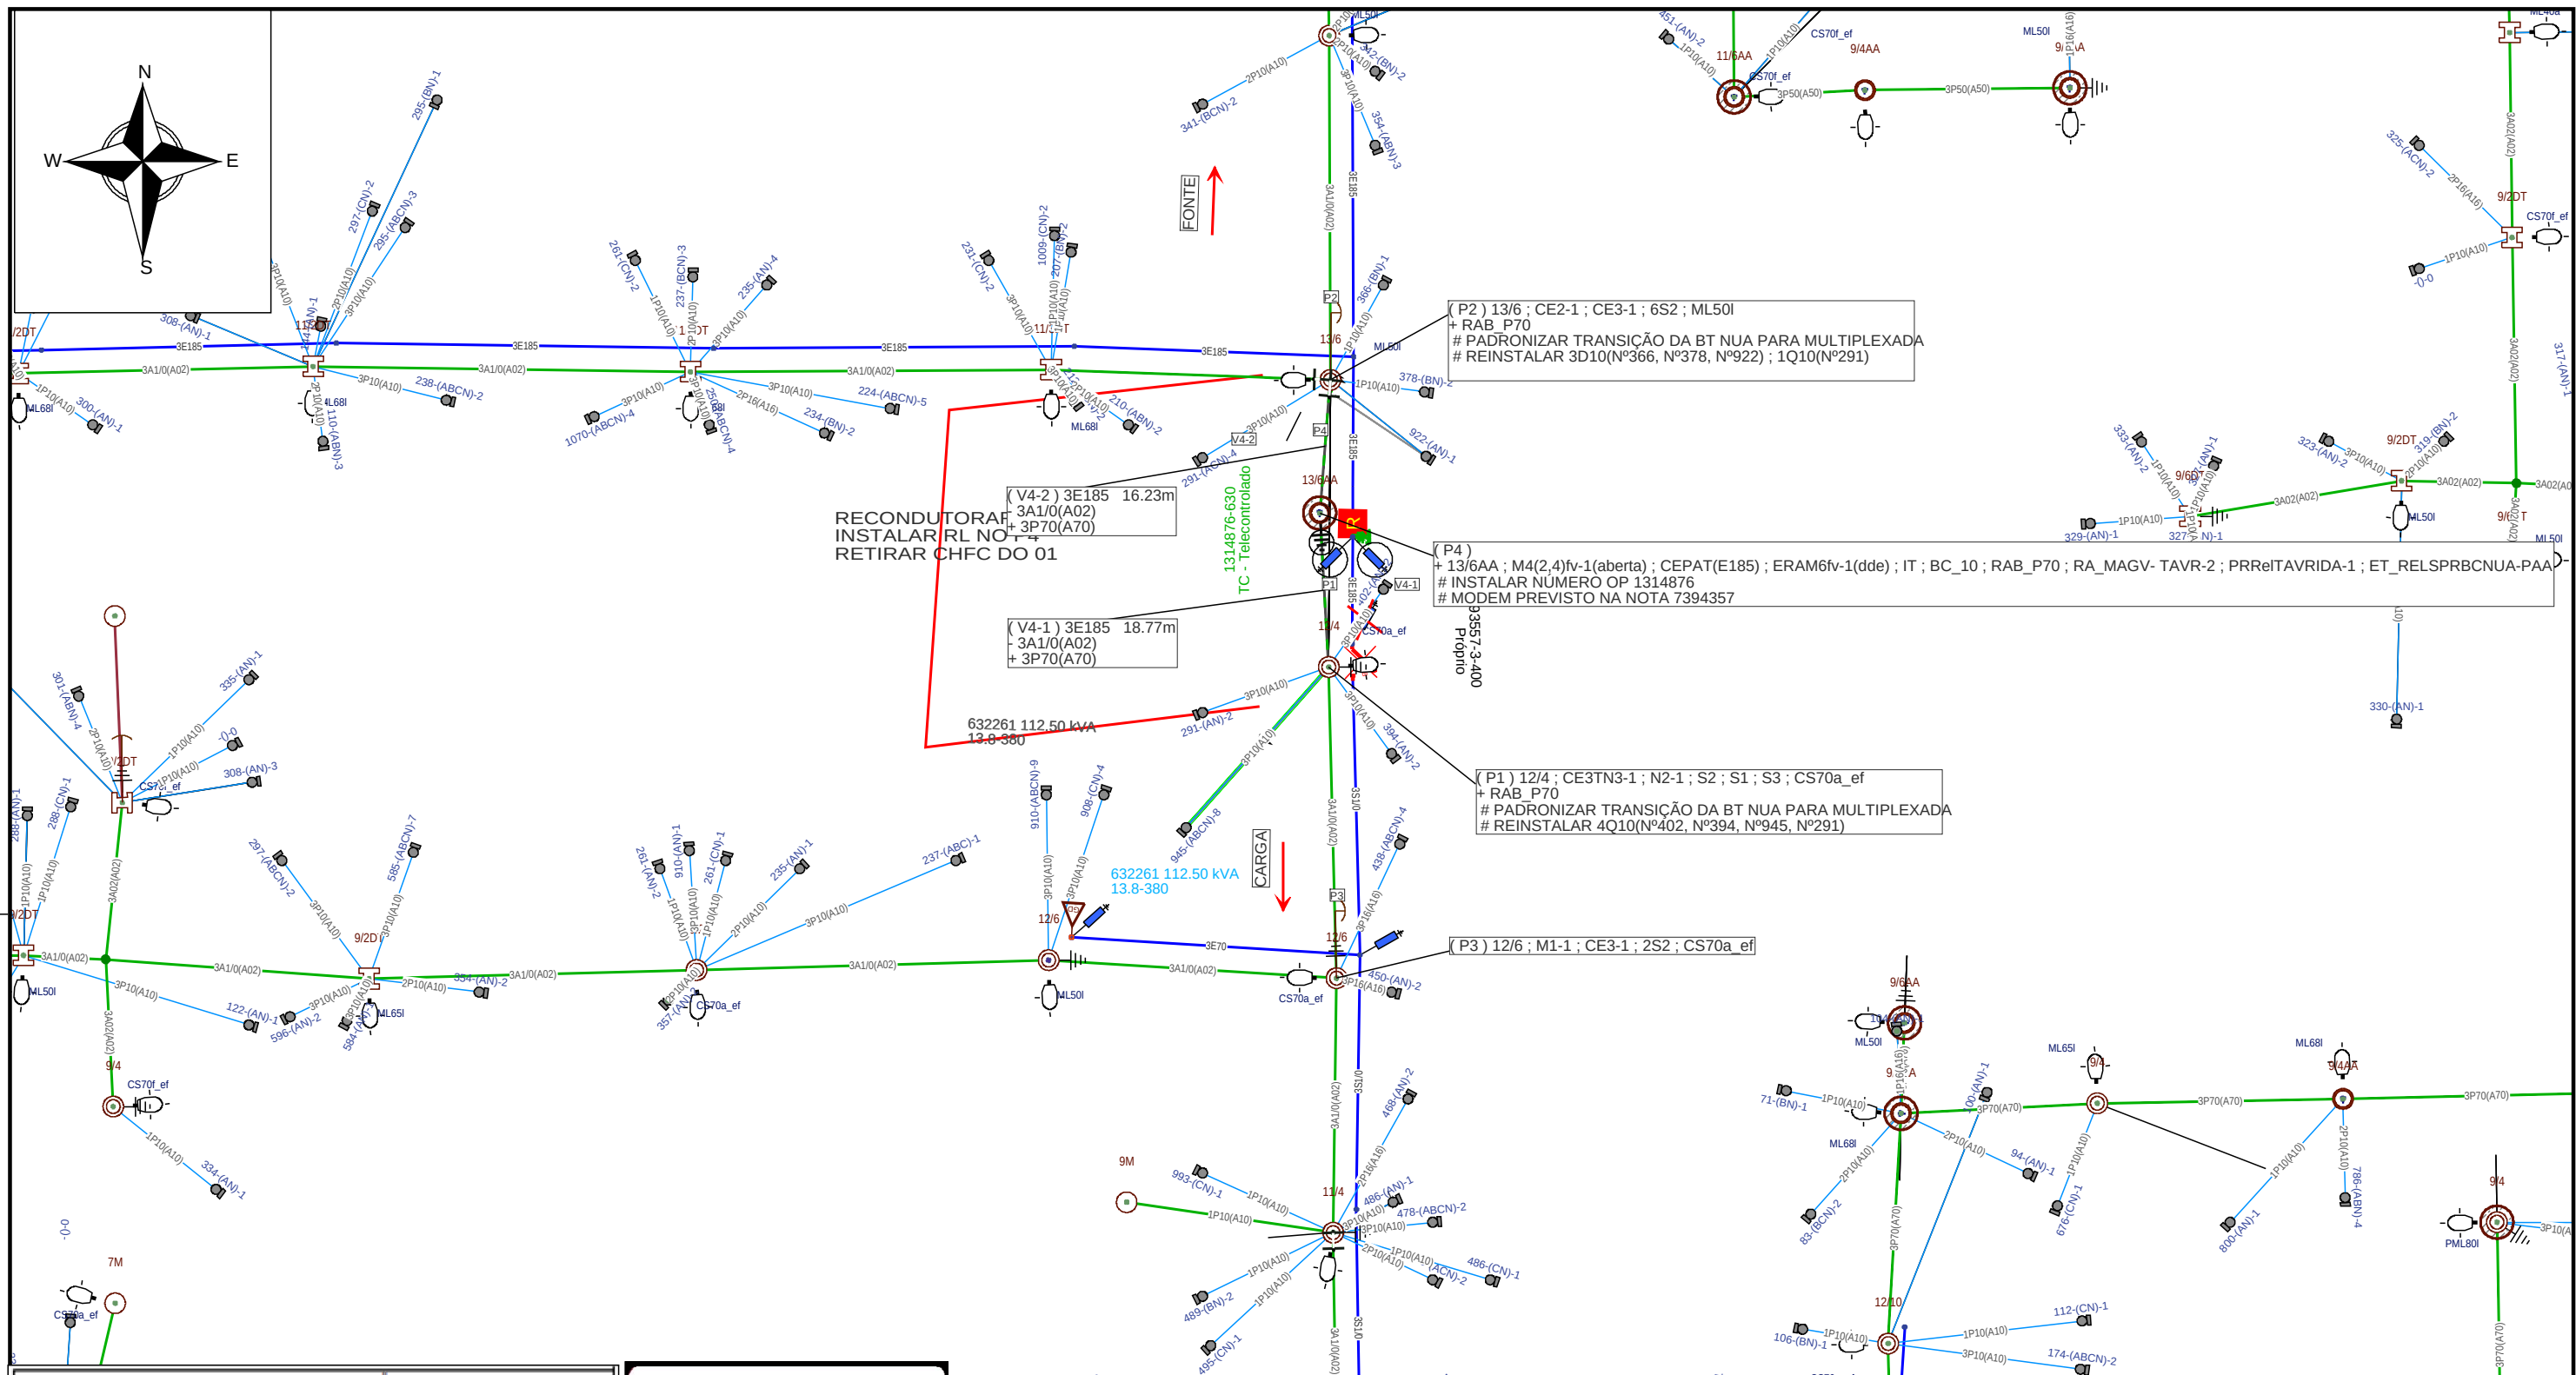

PLANO DE EXECUÇÃO					
RECONDUTORAR BT DO P1 AO P2 ABRIR CAVAS E PREPARAR A OBRA. PROJETO PREVISTO SER REALIZADO COM LV					
Ação	Equipamento	Número	Clientes	Duração	CHI
Desligar	Transformador	632261	131	3	393
					0
					0
					0
					0
Linha Viva?			Sim	CHI TOTAL	393
☐ Poste novo a ser instalado (quando indicado em planta)					



FeedBack Para Fábrica de Projetos

Planeje
Use
Teste
Sinalize
Aterre

Maykou Cardoso
Maykou Luis Cardoso Ribeiro
Gerência de Processos de Obras e Manutenção | DROP
Técnico de Análise e Projetos
CFT: 04262510085

	Gerência de Obras e Manutenção		
	Município: Caxias do Sul		
Cliente: RGE SUL DISTRIBUIDORA DE ENERGIA S.A.			
Obra: RL TRI AVULSO - PLANO 2026			
Endereço: AV DOS LIRIOS S FRANCISCO 402, CHARQUEADAS, CAXIAS DO SUL RS			
Responsável Técnico:  Eng. Ederson Paulo Vogel CREA: RS135794 ART: 10911826	Escala: 1:800	Data: 23/01/2026	Nota: 000007083640
	Classe de isolamento: 15kV	AL: CXA15	Folha 1
	Projetista: Maykou Cardozo	Projeto: 000007964218	Levantador