


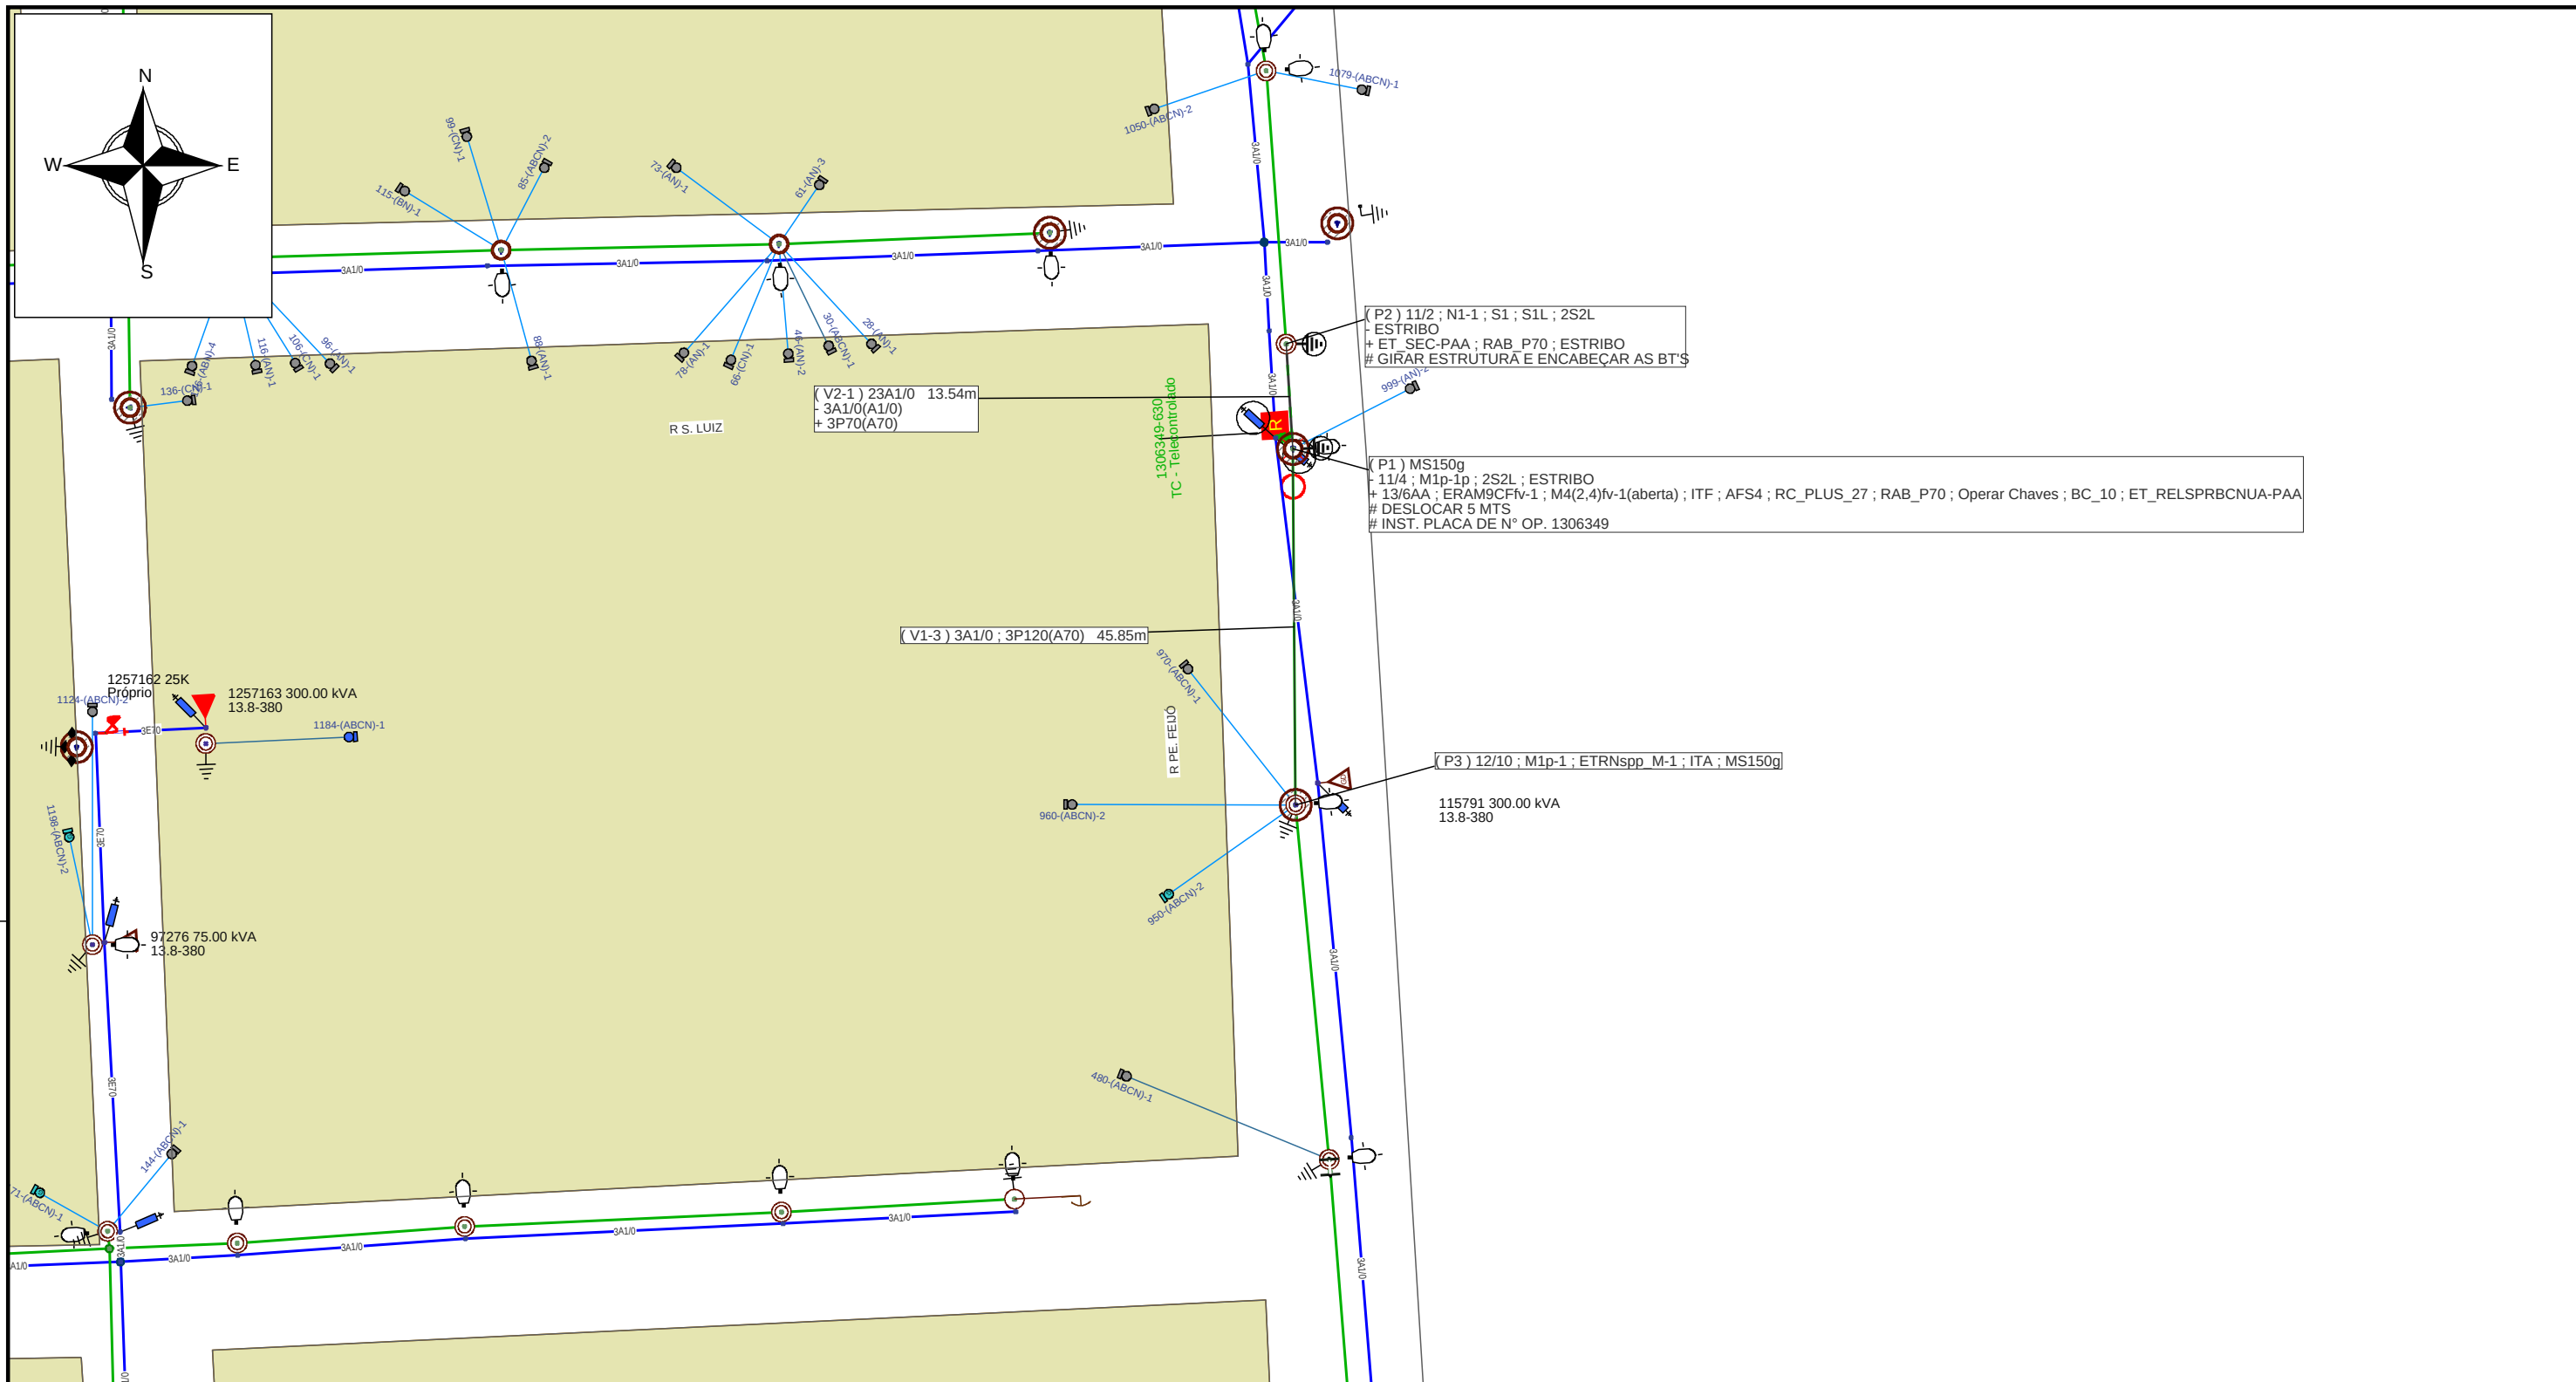

PLANO DE EXECUÇÃO
Para Execução De Obra, Executar As Manobras Abaixo

INSTALAR RELIGADOR COM LV CABO 3A1/0

Ação	Equipamento	Número	Clientes	Duração	CHI
Abrir	Transformador	115791	16	6	96
					0
					0
					0
					0
					0
Linha Viva?	Sim	CHI TOTAL			96

○ Poste novo a ser instalado (quando indicado em planta)

R LUIZ NICOLETTI

Henrique Silva Erguy Junior
Gerência de Processos de Obras e Manutenção | DROP
Técnico de Análise Projetos I
CFT: 5287547404-9

Gerência de Obras e Manutenção

Município: São Marcos

Cliente: RIO GRANDE ENERGIA S.A.

Obra: RL TRI AVULSO - PLANO 2026

Endereço: São Marcos BR RS

Responsável Técnico:
Eng. Ederson Paulo Vogel
CREA: RS135794 ART: 10911826

Escala: 1:850	Data: 07/02/2026	Nota: 000007083800
Classe de isolamento: 15kV	AL: SMC11	Folha 1
Projetista: HENRIQUE ERGUY	Projeto: 000007976875	Levantador S/FC