


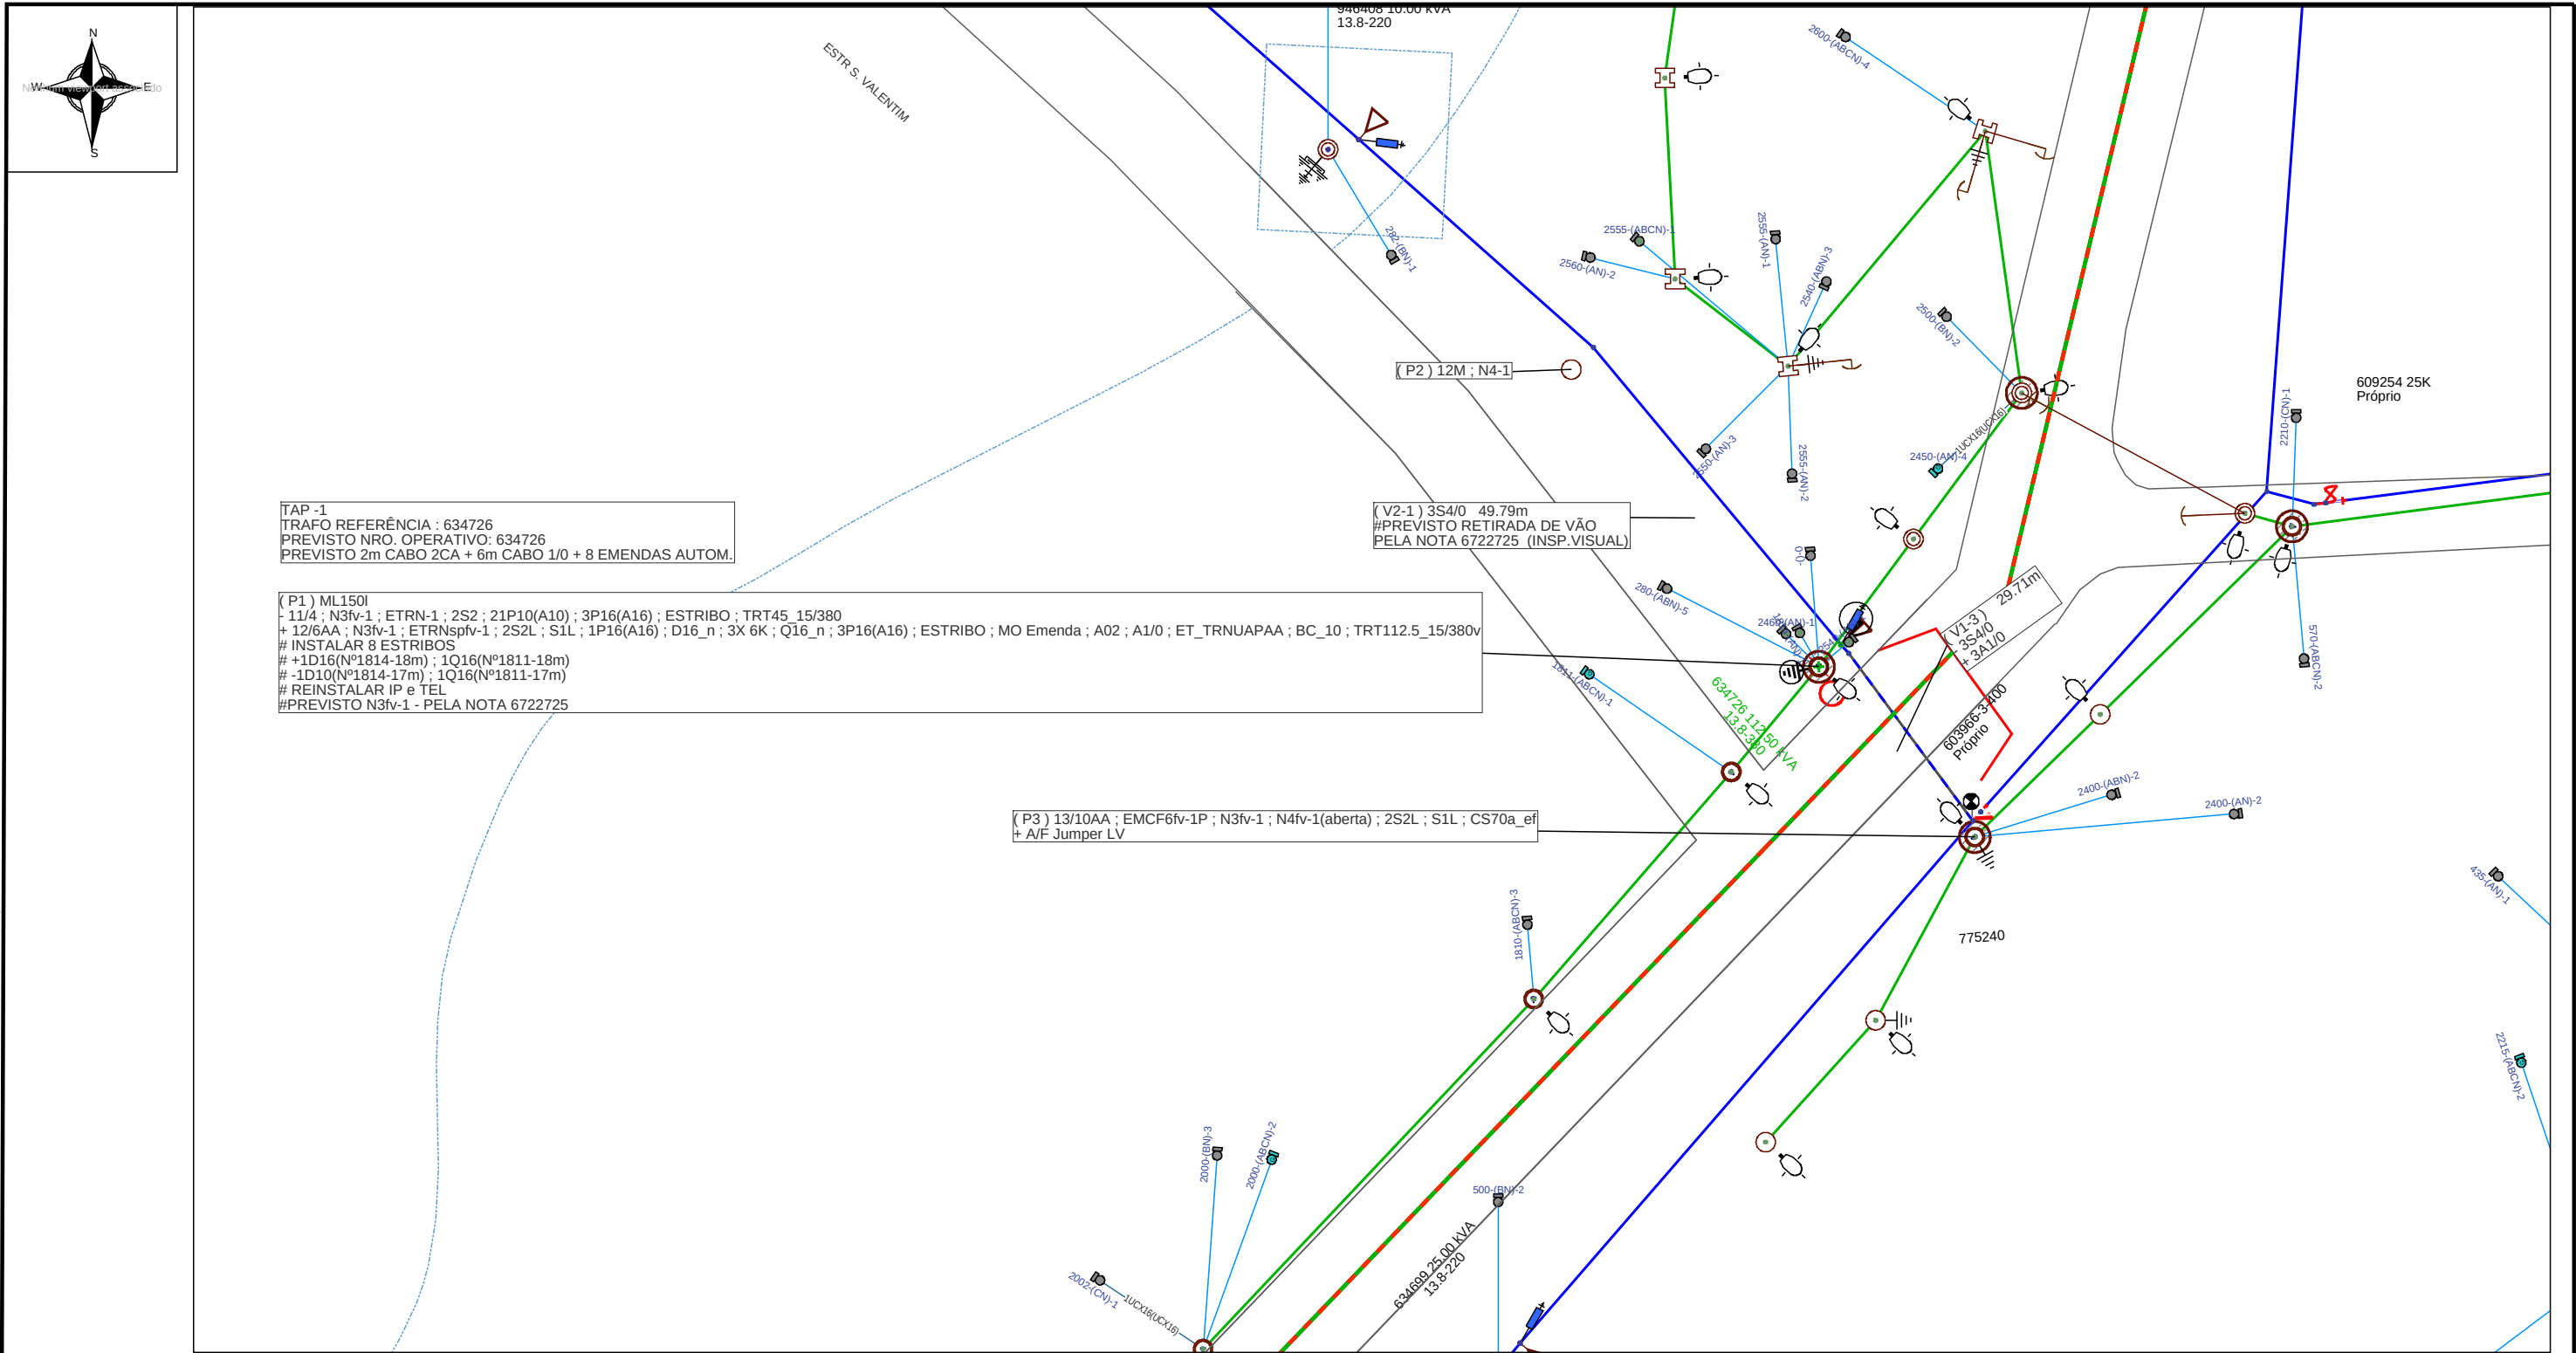

PLANO DE EXECUÇÃO					
!!!AS ATIVIDADES PLANEJADAS NESTE ESTUDO DEVE SER EXECUTADAS DE FORMA 100% SEGURA, RESPEITANDO AS NORMAS TÉCNICAS !!!					
Realizar atividade com linha viva - P3 - SUBST. 1 VÃO MT PARA REDUÇÃO DE ESFORÇO NO P1					
Ação	Equipamento	Número	Clientes	Duração	CHI
Abriu	Transformador	634726	41	4	164
					0
					0
					0
					0
					0
Linha Viva?		Sim	CHI TOTAL		164
☐ Poste novo a ser instalado (quando indicado em planta)					

FeedBack Para Fábrica de Projetos

Planeje
Use
Teste
Sinalize
Aterre

João Batista R. da Silva

JOÃO BATISTA R.DA SILVA

Gerência de Processos de Obras e Manutenção | DROP

Técnico de Análise e Projetos

CFT: 48162671072

Gerência de Obras e Manutenção

Município: Caxias do Sul

Cliente: RGE SUL DISTRIBUIDORA DE ENERGIA S/A

Obra: Plano Sobrecarga 2026

Endereço: EST FEDERAL BR 116,2540

Responsável Técnico:

Eng. Ederson Paulo Vogel

CREA: RS135794 ART: 10911826

Nenhum viewport associado

Classe de isolamento: 15kV

Projetista: JOÃO BATISTA

Data: 16/02/2026

AL: CXD15

Projeto: 000007981995

Nota: 000007114224

Folha 1

Levantador: RICARDO Q DE ALBUQUERQUE