


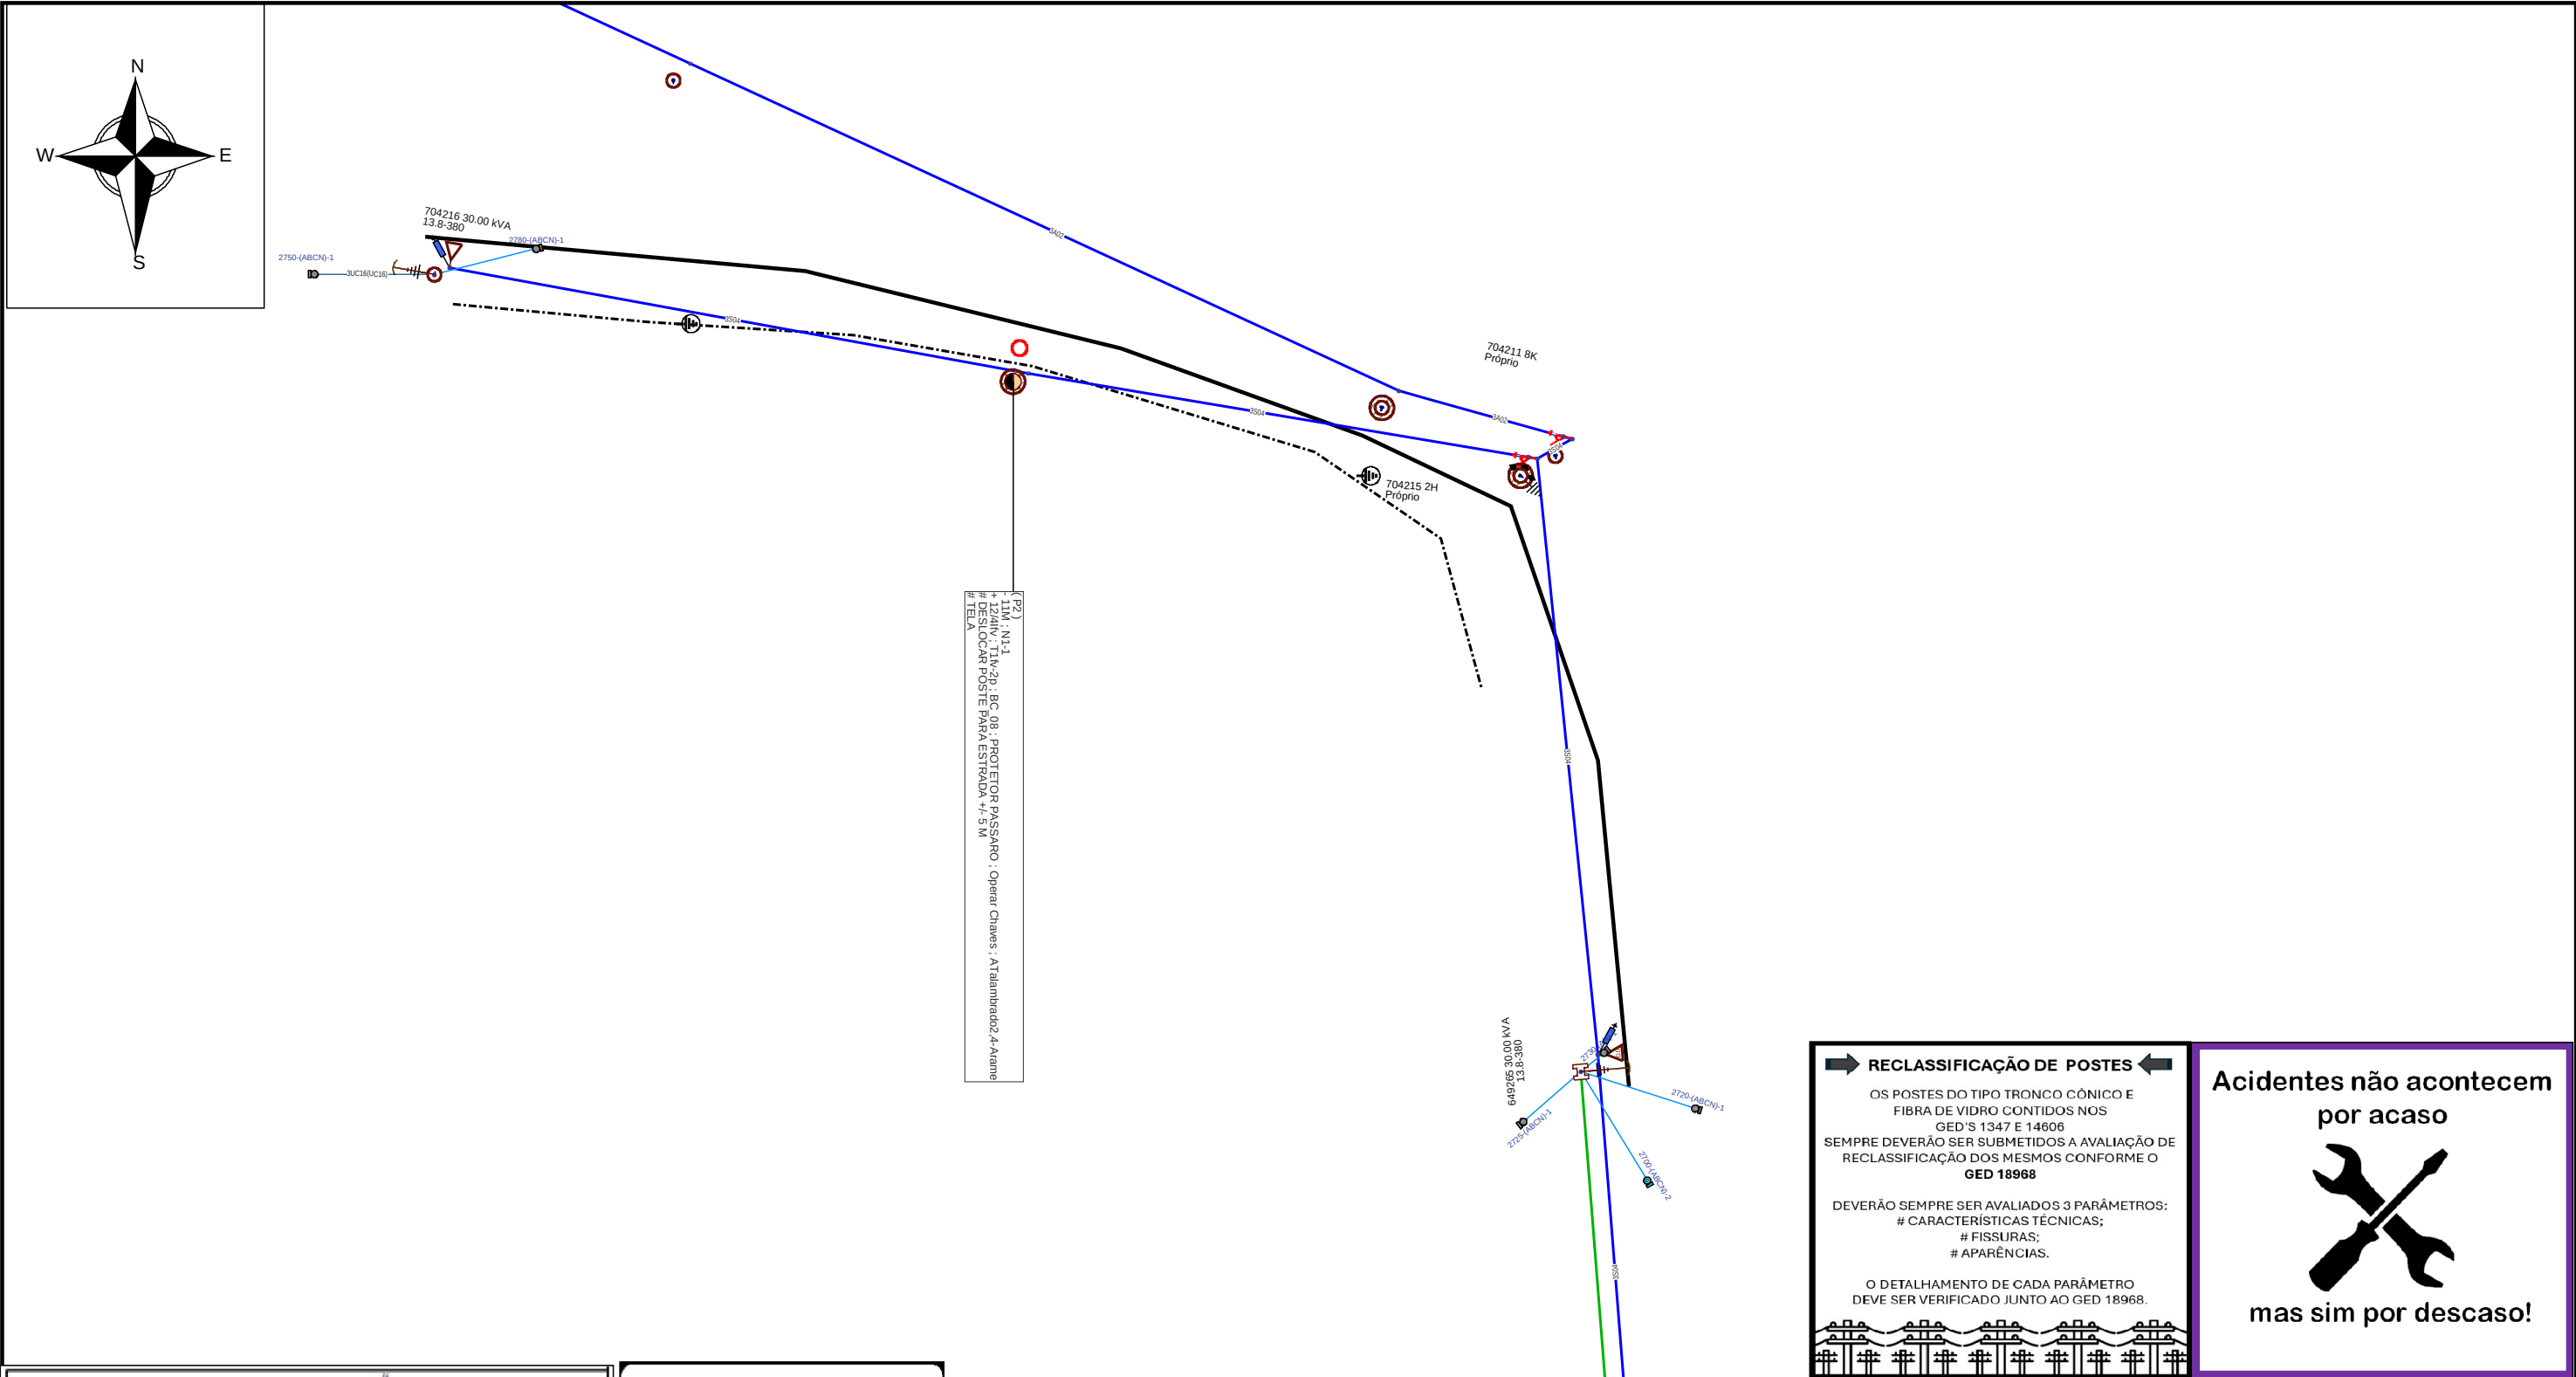

PLANO DE EXECUÇÃO					
Executar a obra seguindo todos os passos de segurança!					
SUBSTITUIR POSTES INDICADOS EM PLANTA SEGUINDO OS PROCEDIMENTOS DE SEGURANÇA					

FeedBack Para Fábrica de Projetos

Breno Ardenghy

Breno Ardenghy Da Silva

Gerência de Processos de Obras e Manutenção | DROP

Técnico de Análise e Projetos

CFT: 03188101074

Gerência de Obras e Manutenção

Município: Flores da Cunha

Cliente: RGE SUL DISTRIBUIDORA DE ENERGIA S.A

Obra: Substituição de Poste - OS 101084255

Endereço: R ALESSANDRIA 2750 S GOTARDO FLORES DA CUNHA

Responsável Técnico:

Eng. Ederson Paulo Vogel
CREA: RS135794 ART: 10911826

Escala: 1:1100

Classe de isolamento: 15kV

Projetista: BRENO ARDENGHY

Data: 13/12/2025

AL: FCU13

Projeto: 000007943156

Nota: 000007143264

Folha 1

Levantador REINHOLDO BRULINGER