


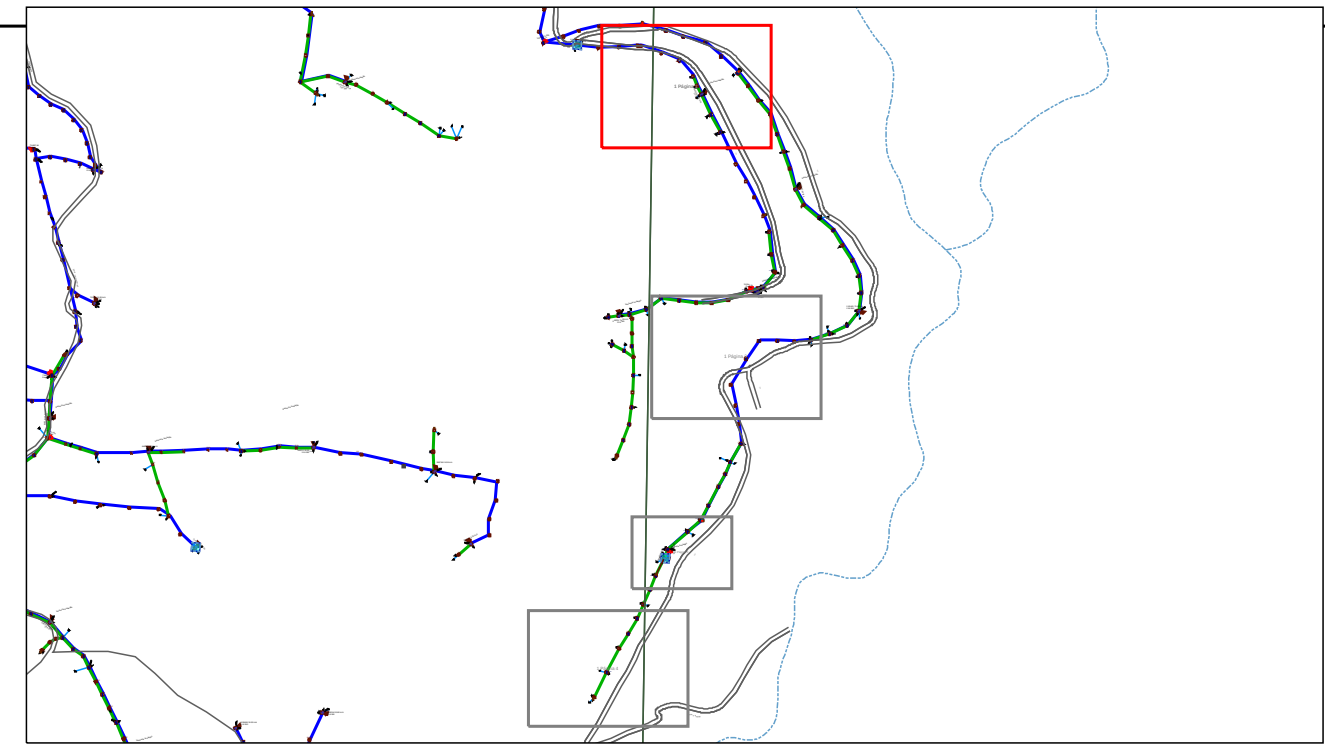


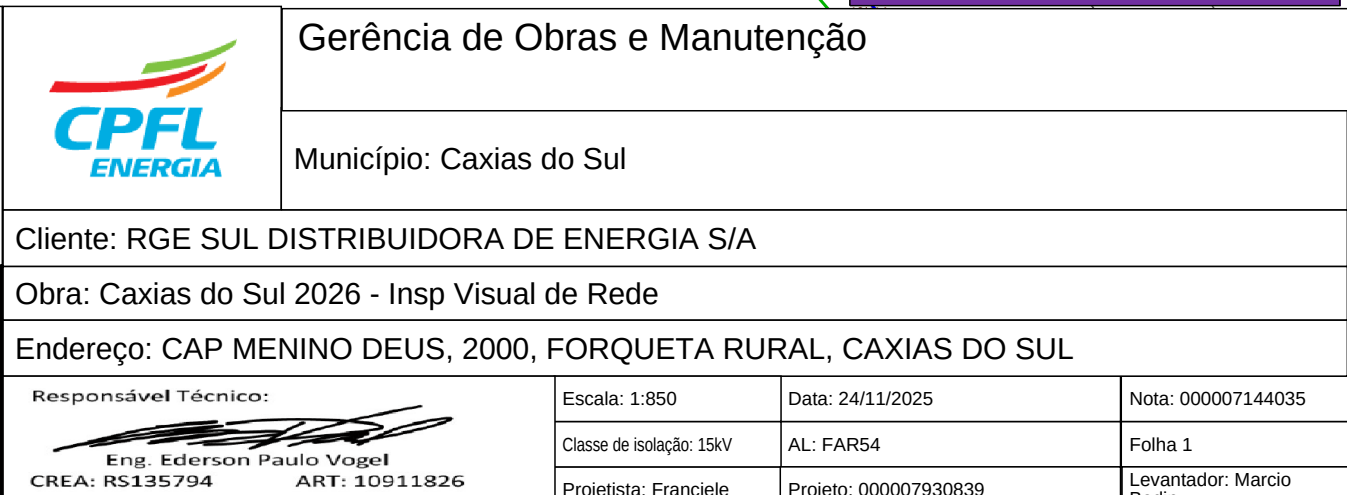

FeedBack Para Fábrica de Projetos

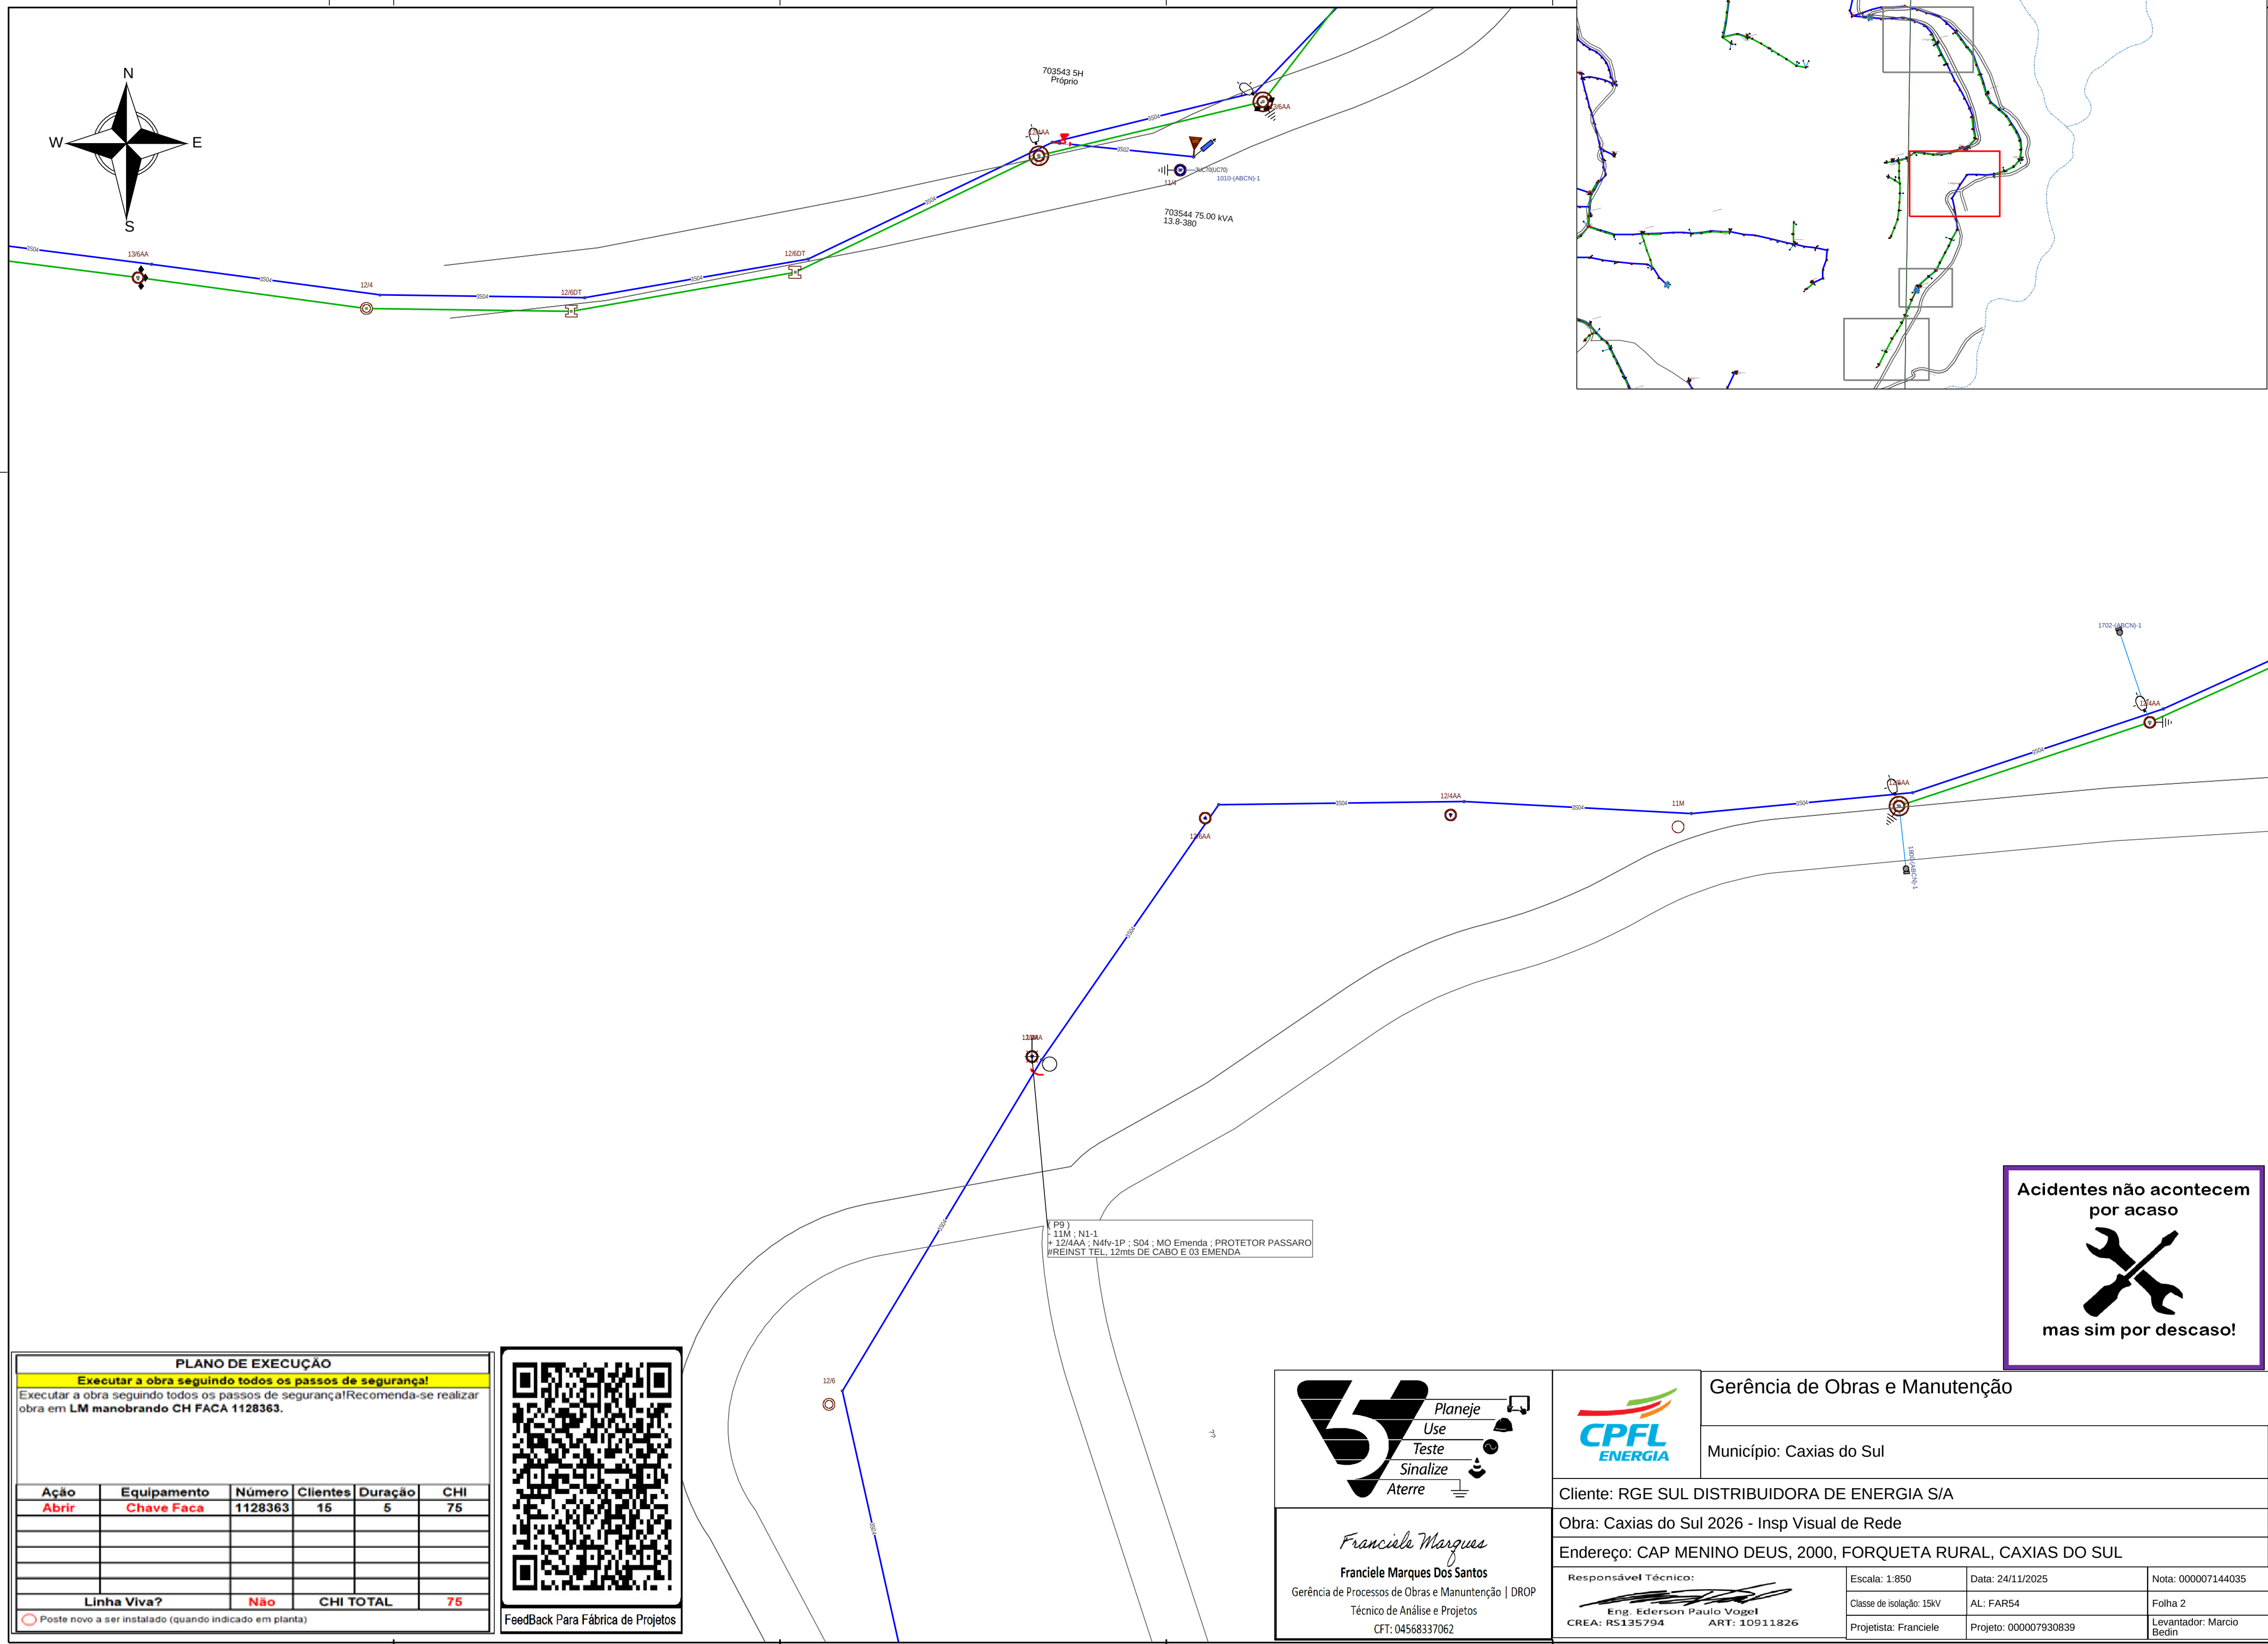


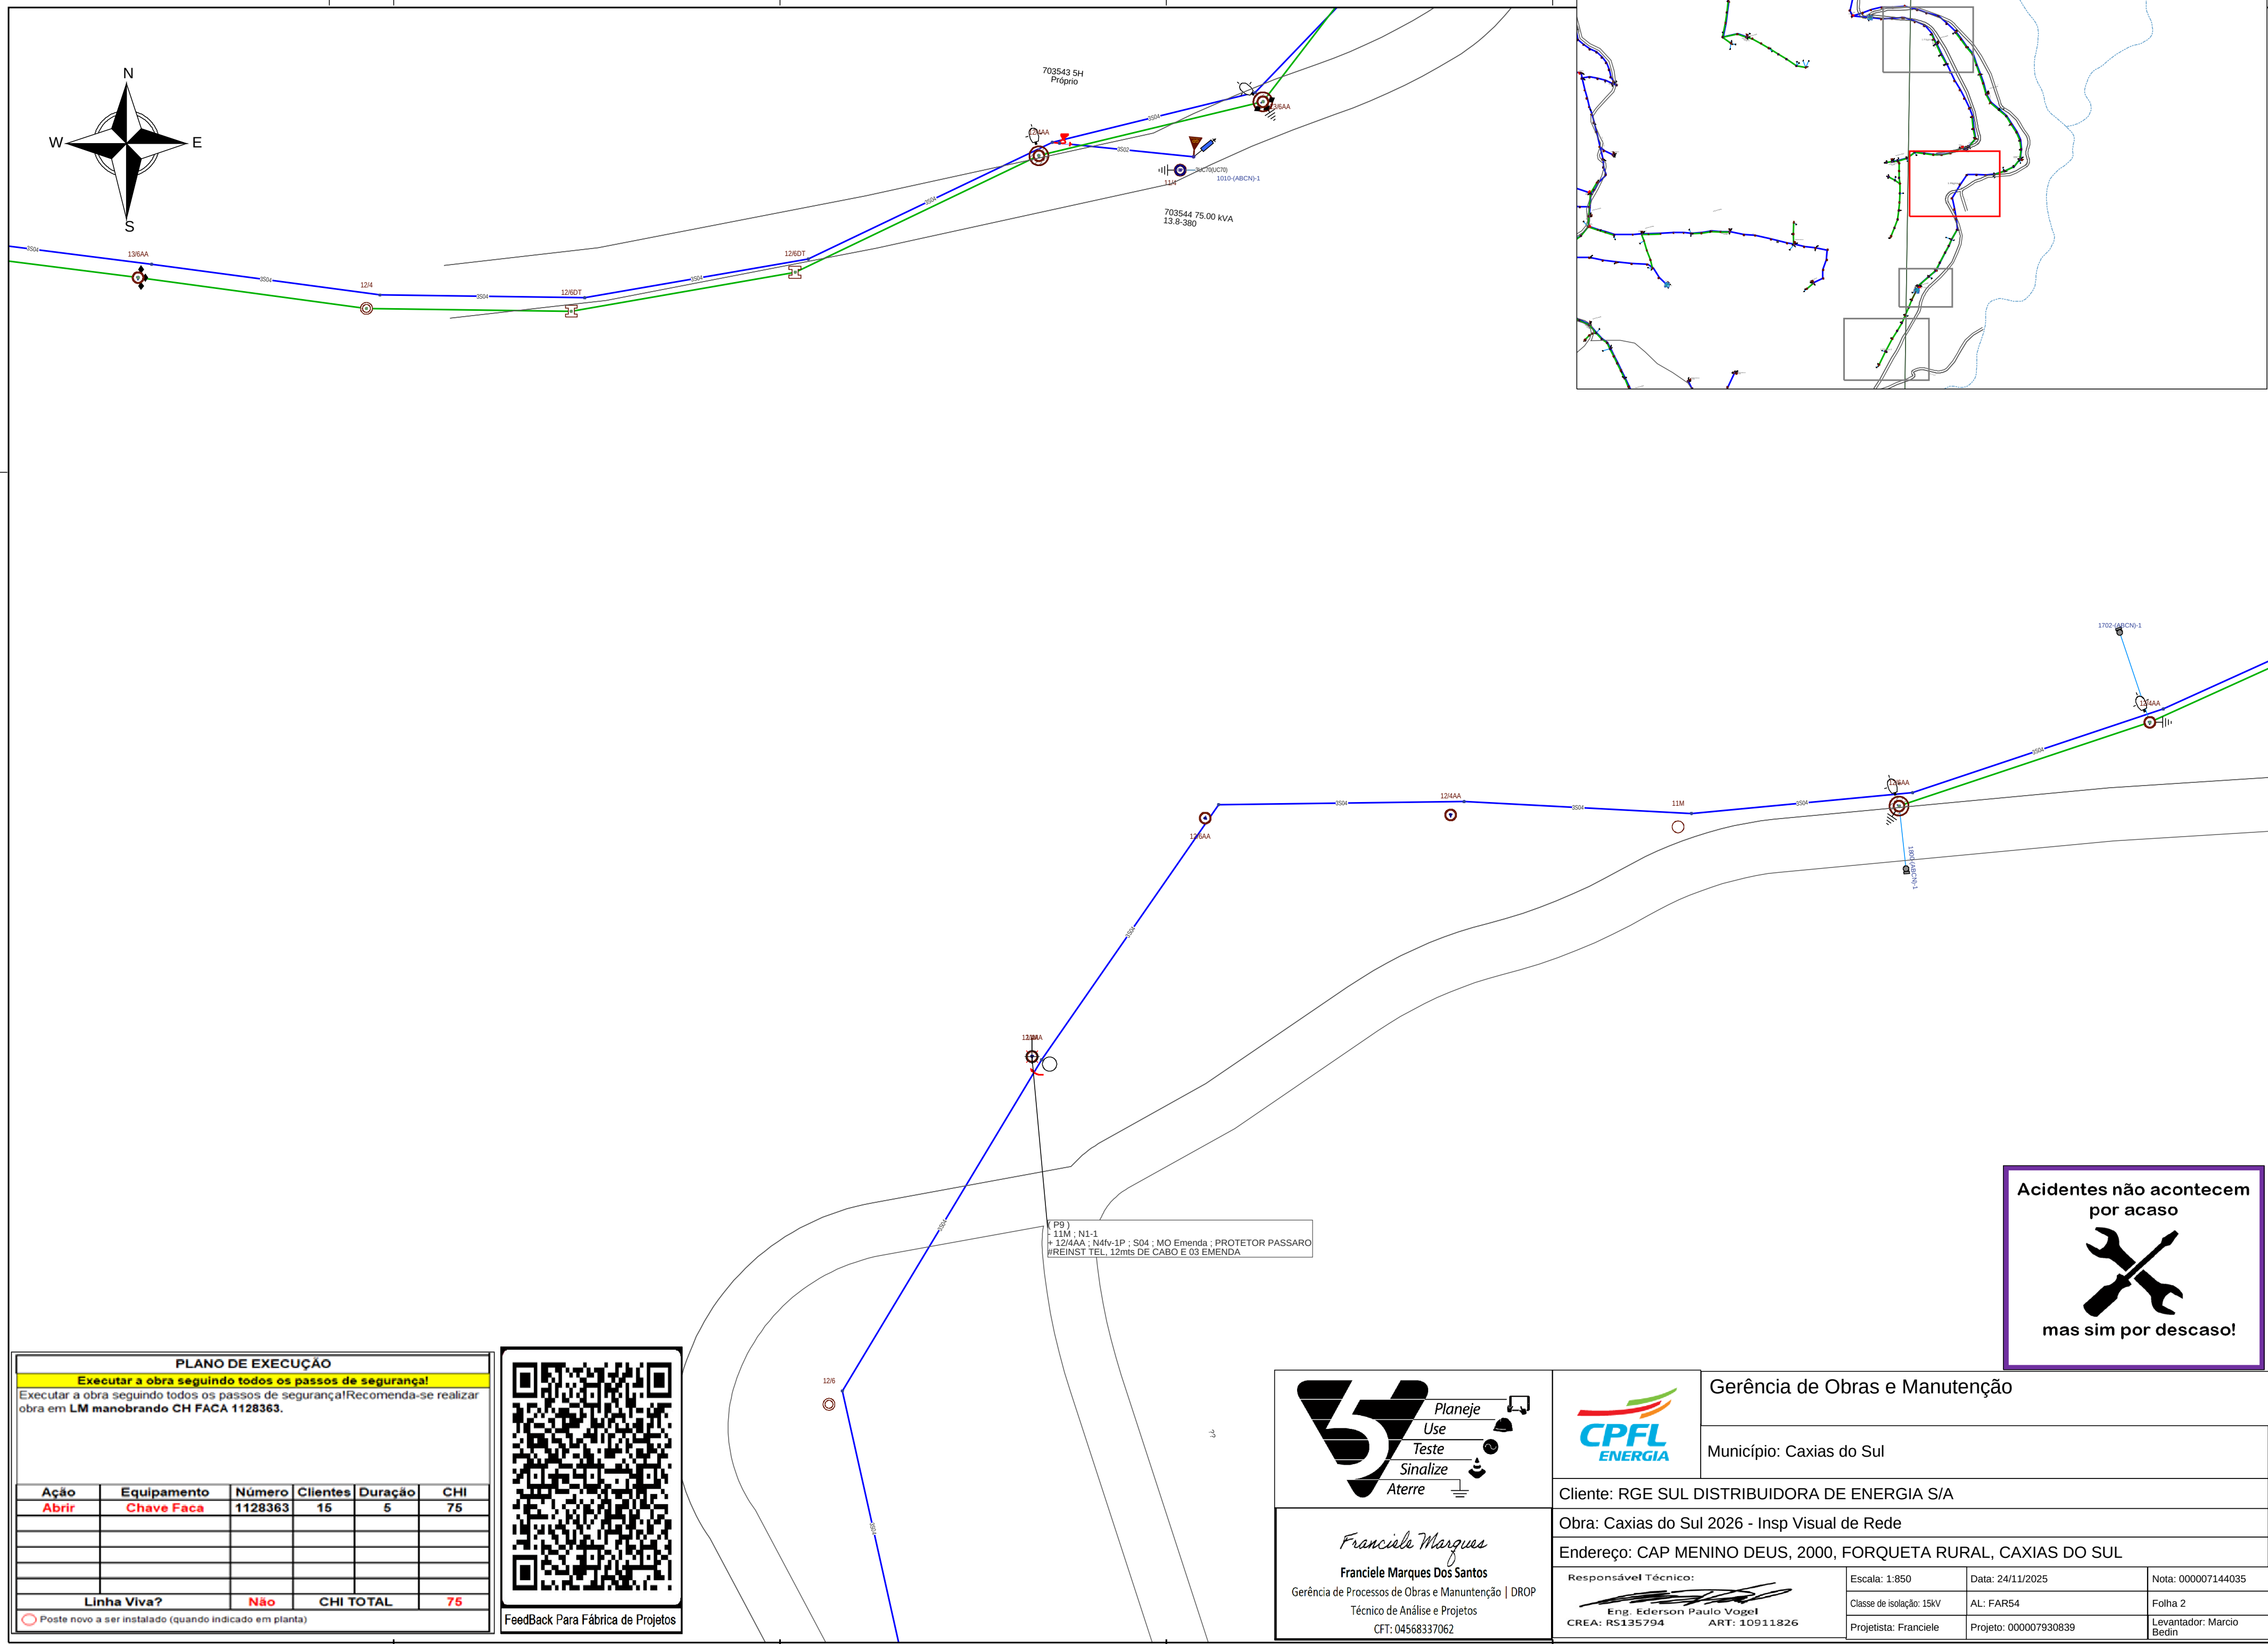



mas sim por descaso!



FeedBack Para Fábrica de Projetos

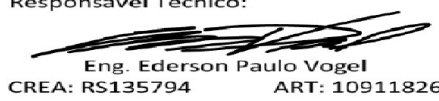

|                       |                    |
|-----------------------|--------------------|
| Projeto: 000007930839 | Levantador: Marcio |
|-----------------------|--------------------|

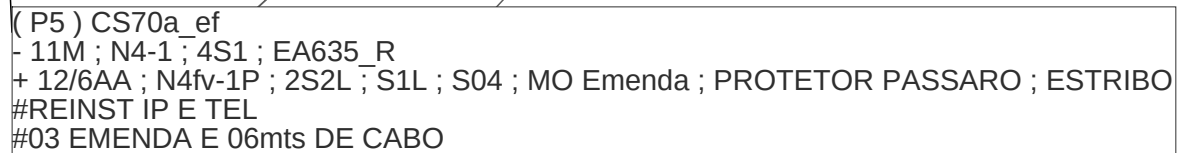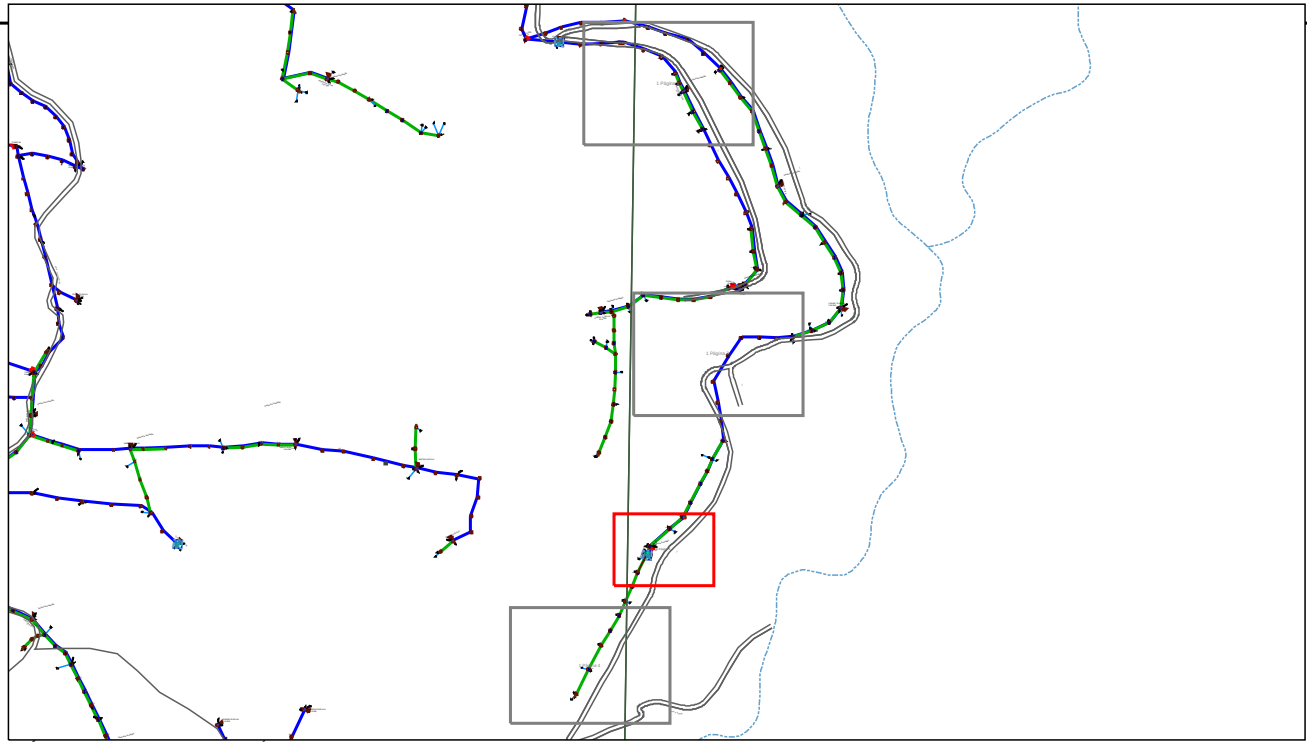

**mas sim por descaso!**

## FeedBack Para Fábrica de Projetos



Eng. Ederson Paulo Vogel  
CREA: RS135794      ART: 10911826




Folha 3

Projetista: Franciele

Projeto: 000007930839

Levantador: Marcio  
Rodin




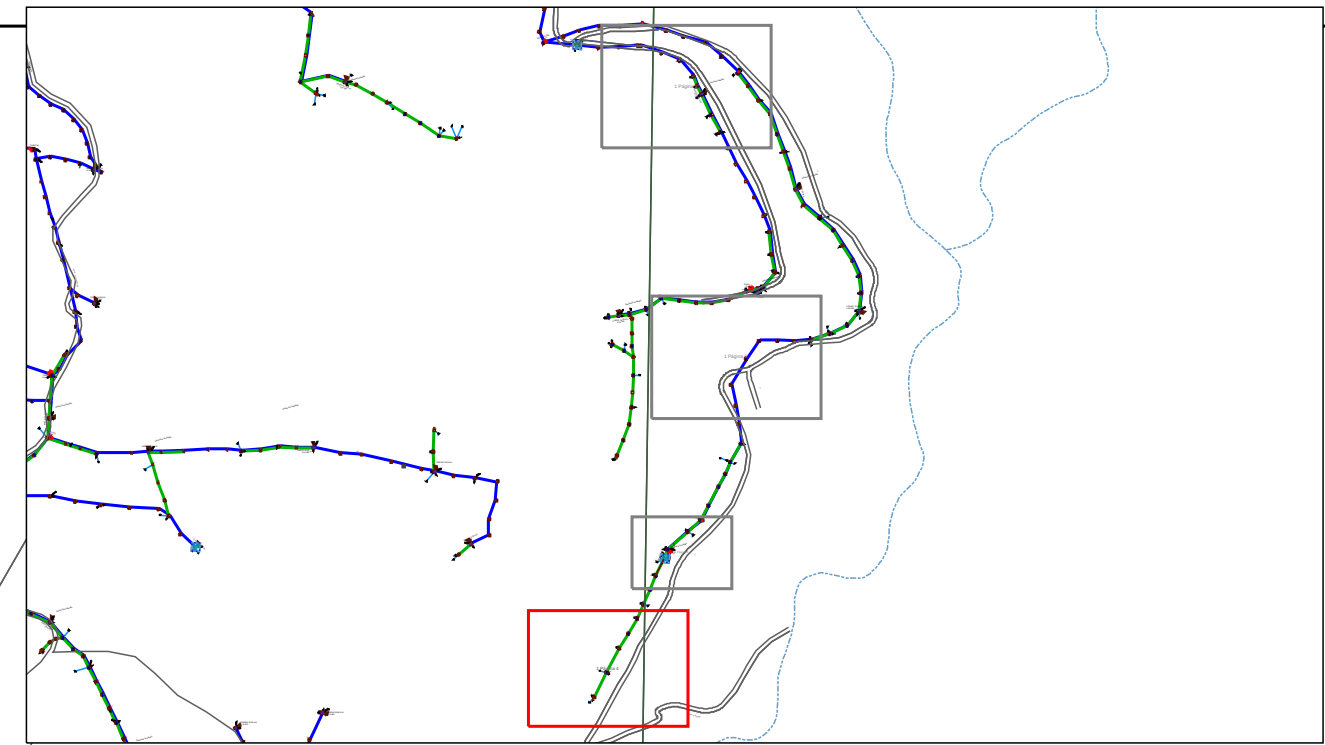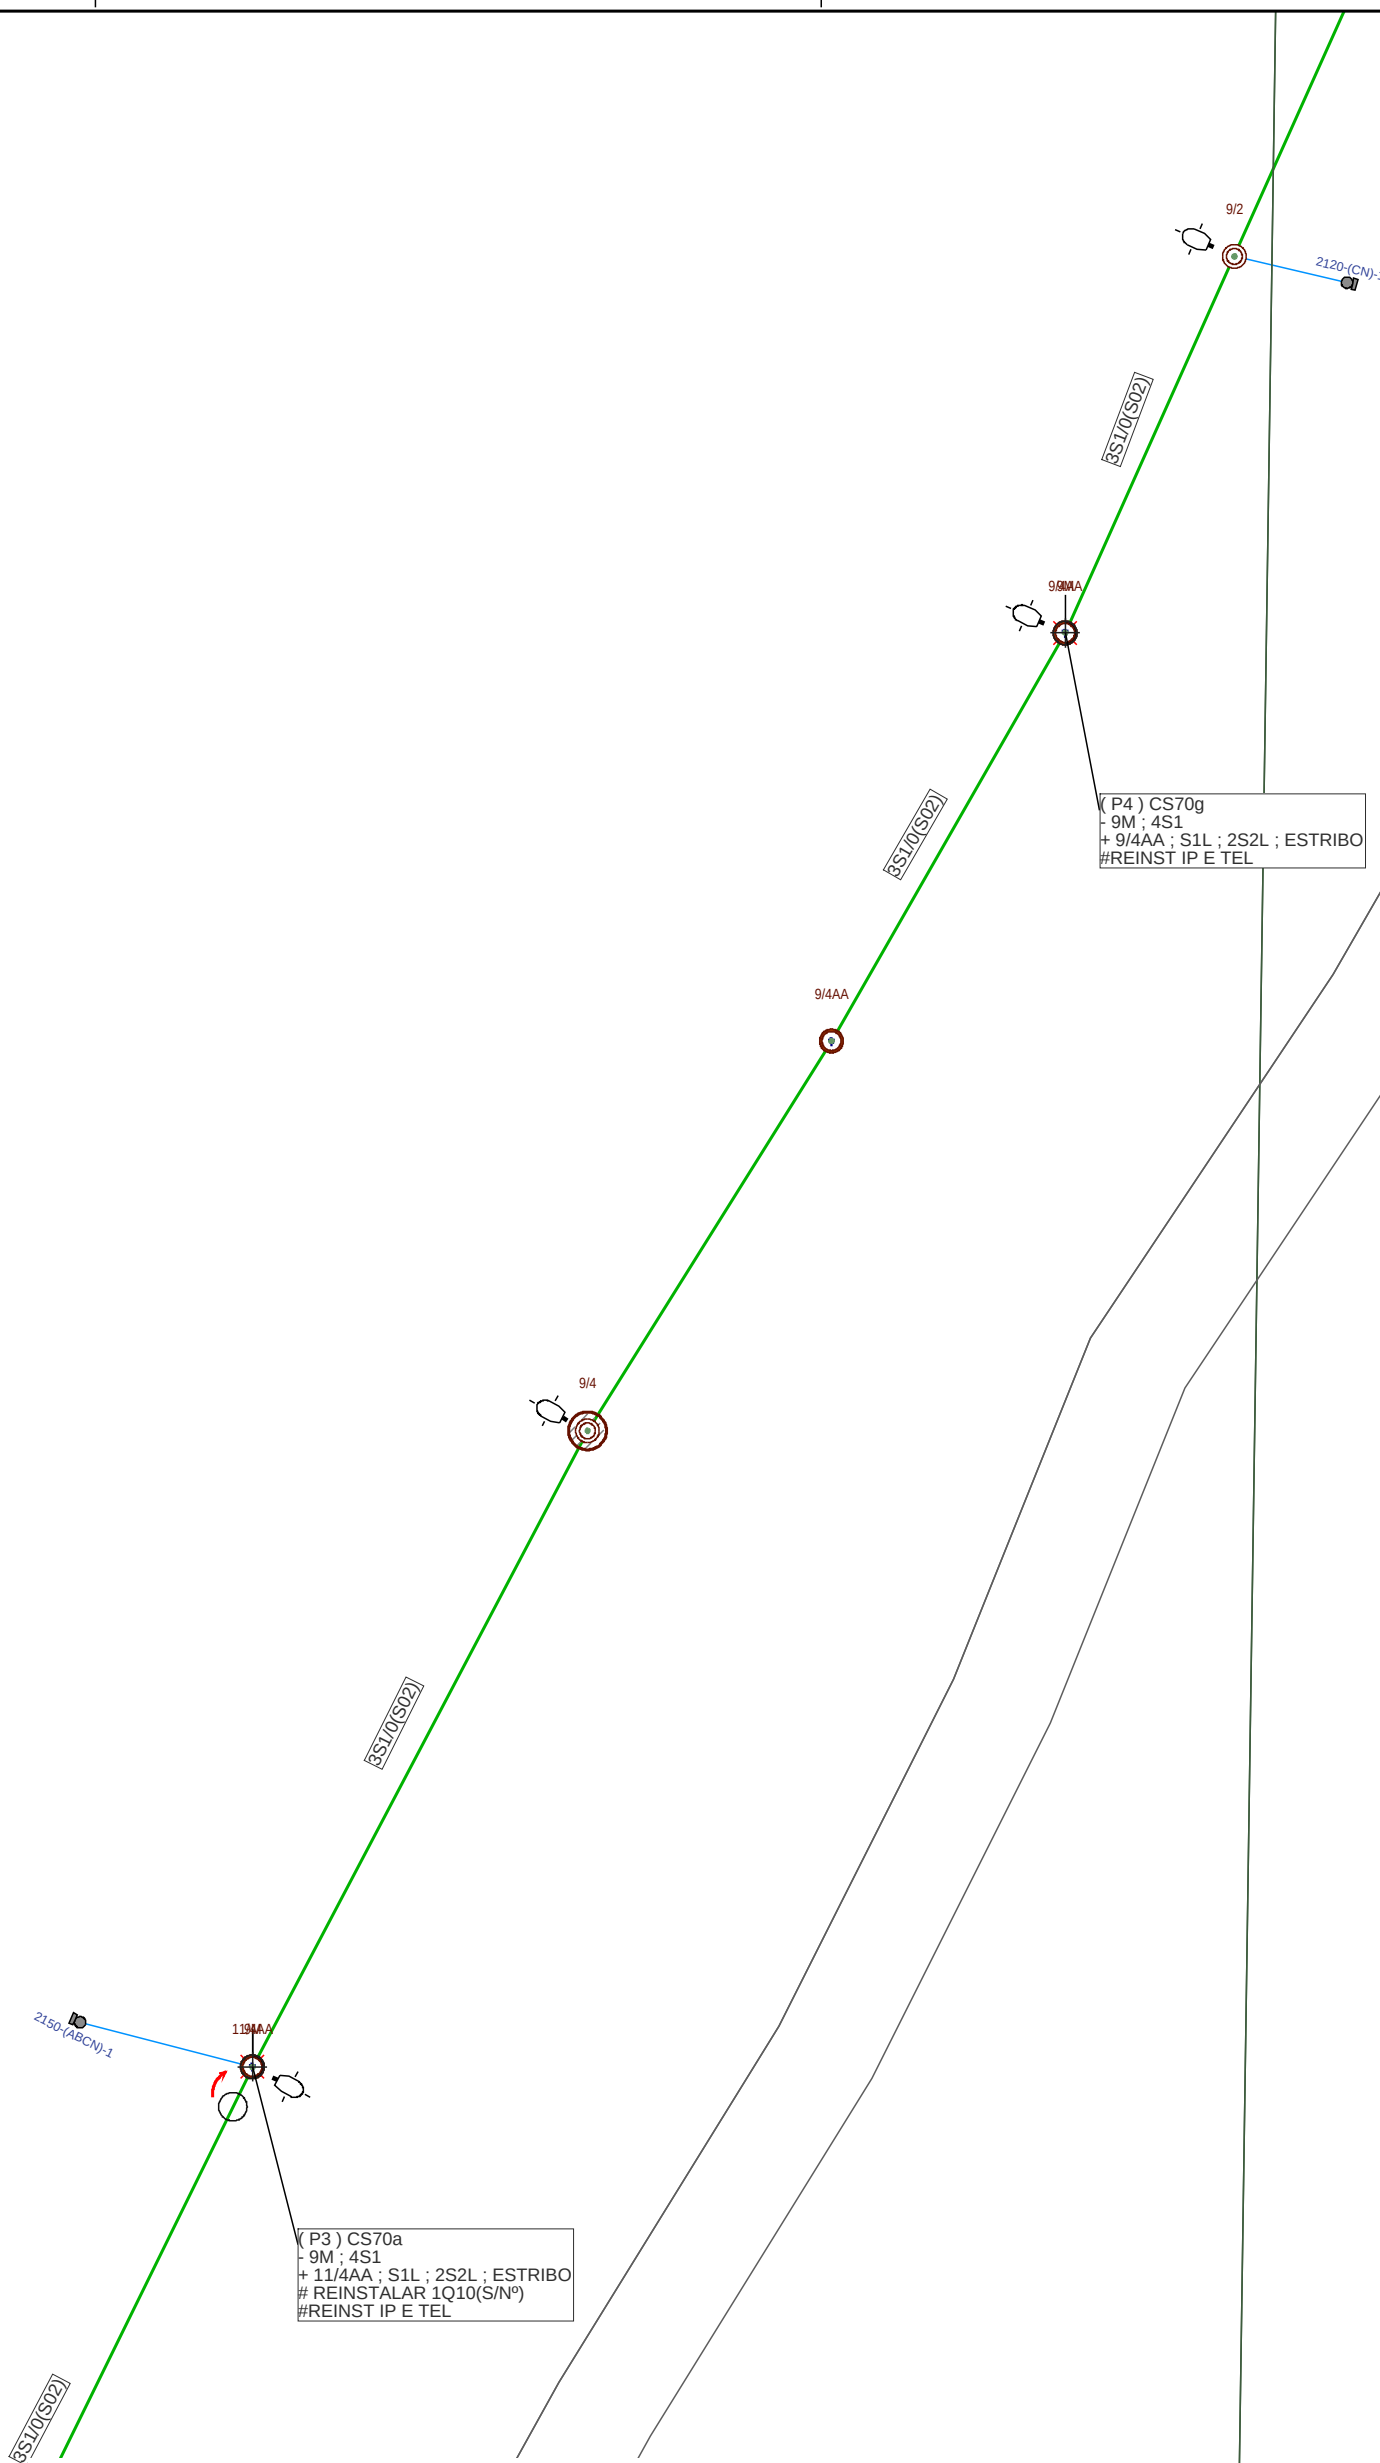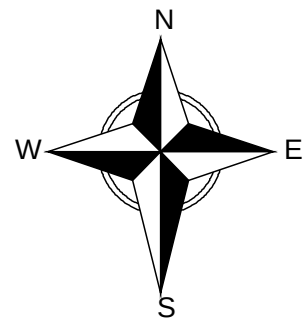

FeedBack Para Fábrica de Projetos

| PLANO DE EXECUÇÃO                                                                                                  |             |         |          |           |     |
|---|-------------|---------|----------|-----------|-----|
| Executar a obra seguindo todos os passos de segurança!                                                             |             |         |          |           |     |
| Executar a obra seguindo todos os passos de segurança!Recomenda-se realizar obra em LM manobrando CH FACA 1128363. |             |         |          |           |     |
|   |             |         |          |           |     |
| Ação   | Equipamento | Número  | Cilentes | Duração   | CHI |
| Abriu   | Chave Faca  | 1128363 | 15       | 5         | 75  |
|   |             |         |          |           |     |
|   |             |         |          |           |     |
|   |             |         |          |           |     |
|   |             |         |          |           |     |
| Linha Viva?   |             |         | Não      | CHI TOTAL | 75  |
| ○ Poste novo a ser instalado (quando indicado em planta)                                                           |             |         |          |           |     |

COORDENADAS  
TR 648208 REF  
29°15'54.1"S  
51°15'54.3"W  
CAP MENINO  
DEUS, 2428,  
FORQUETA  
RURAL,  
CAXIAS DO SUL

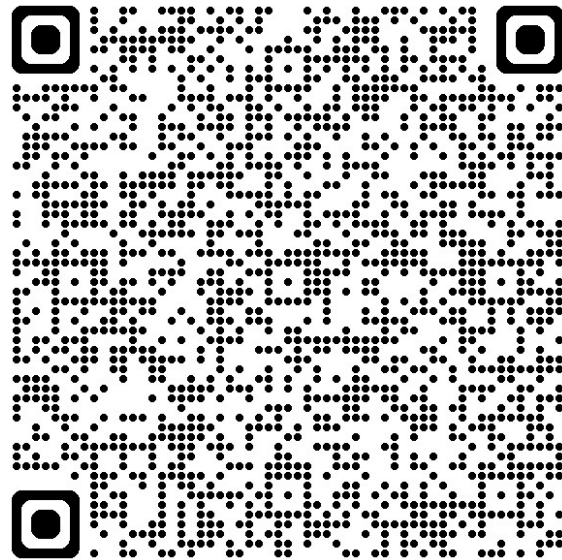

Acidentes não acontecem  
por acaso  
  
mas sim por descaso!



Planeje  
Use  
Teste  
Sinalize  
Aterre

Franciele Marques  
Gerência de Processos de Obras e Manutenção | DROP  
Técnico de Análise e Projetos  
CFT: 04568337062



Gerência de Obras e Manutenção

Município: Caxias do Sul

Ciente: RGE SUL DISTRIBUIDORA DE ENERGIA S/A

Obra: Caxias do Sul 2026 - Insp Visual de Rede

Endereço: CAP MENINO DEUS, 2000, FORQUETA RURAL, CAXIAS DO SUL

|   |                                                                      |                                                        |                                                           |
|---|----------------------------------------------------------------------|--------------------------------------------------------|-----------------------------------------------------------|
| Responsável Técnico:<br><br>Eng. Ederson Paulo Vogel<br>CREA: RS135794      ART: 10911826 | Escala: 1:800<br>Classe de isolamento: 15kV<br>Projetista: Franciele | Data: 24/11/2025<br>AL: FAR54<br>Projeto: 000007930839 | Nota: 000007144035<br>Folha 4<br>Levantador: Marcio Bedin |
|---|----------------------------------------------------------------------|--------------------------------------------------------|-----------------------------------------------------------|