


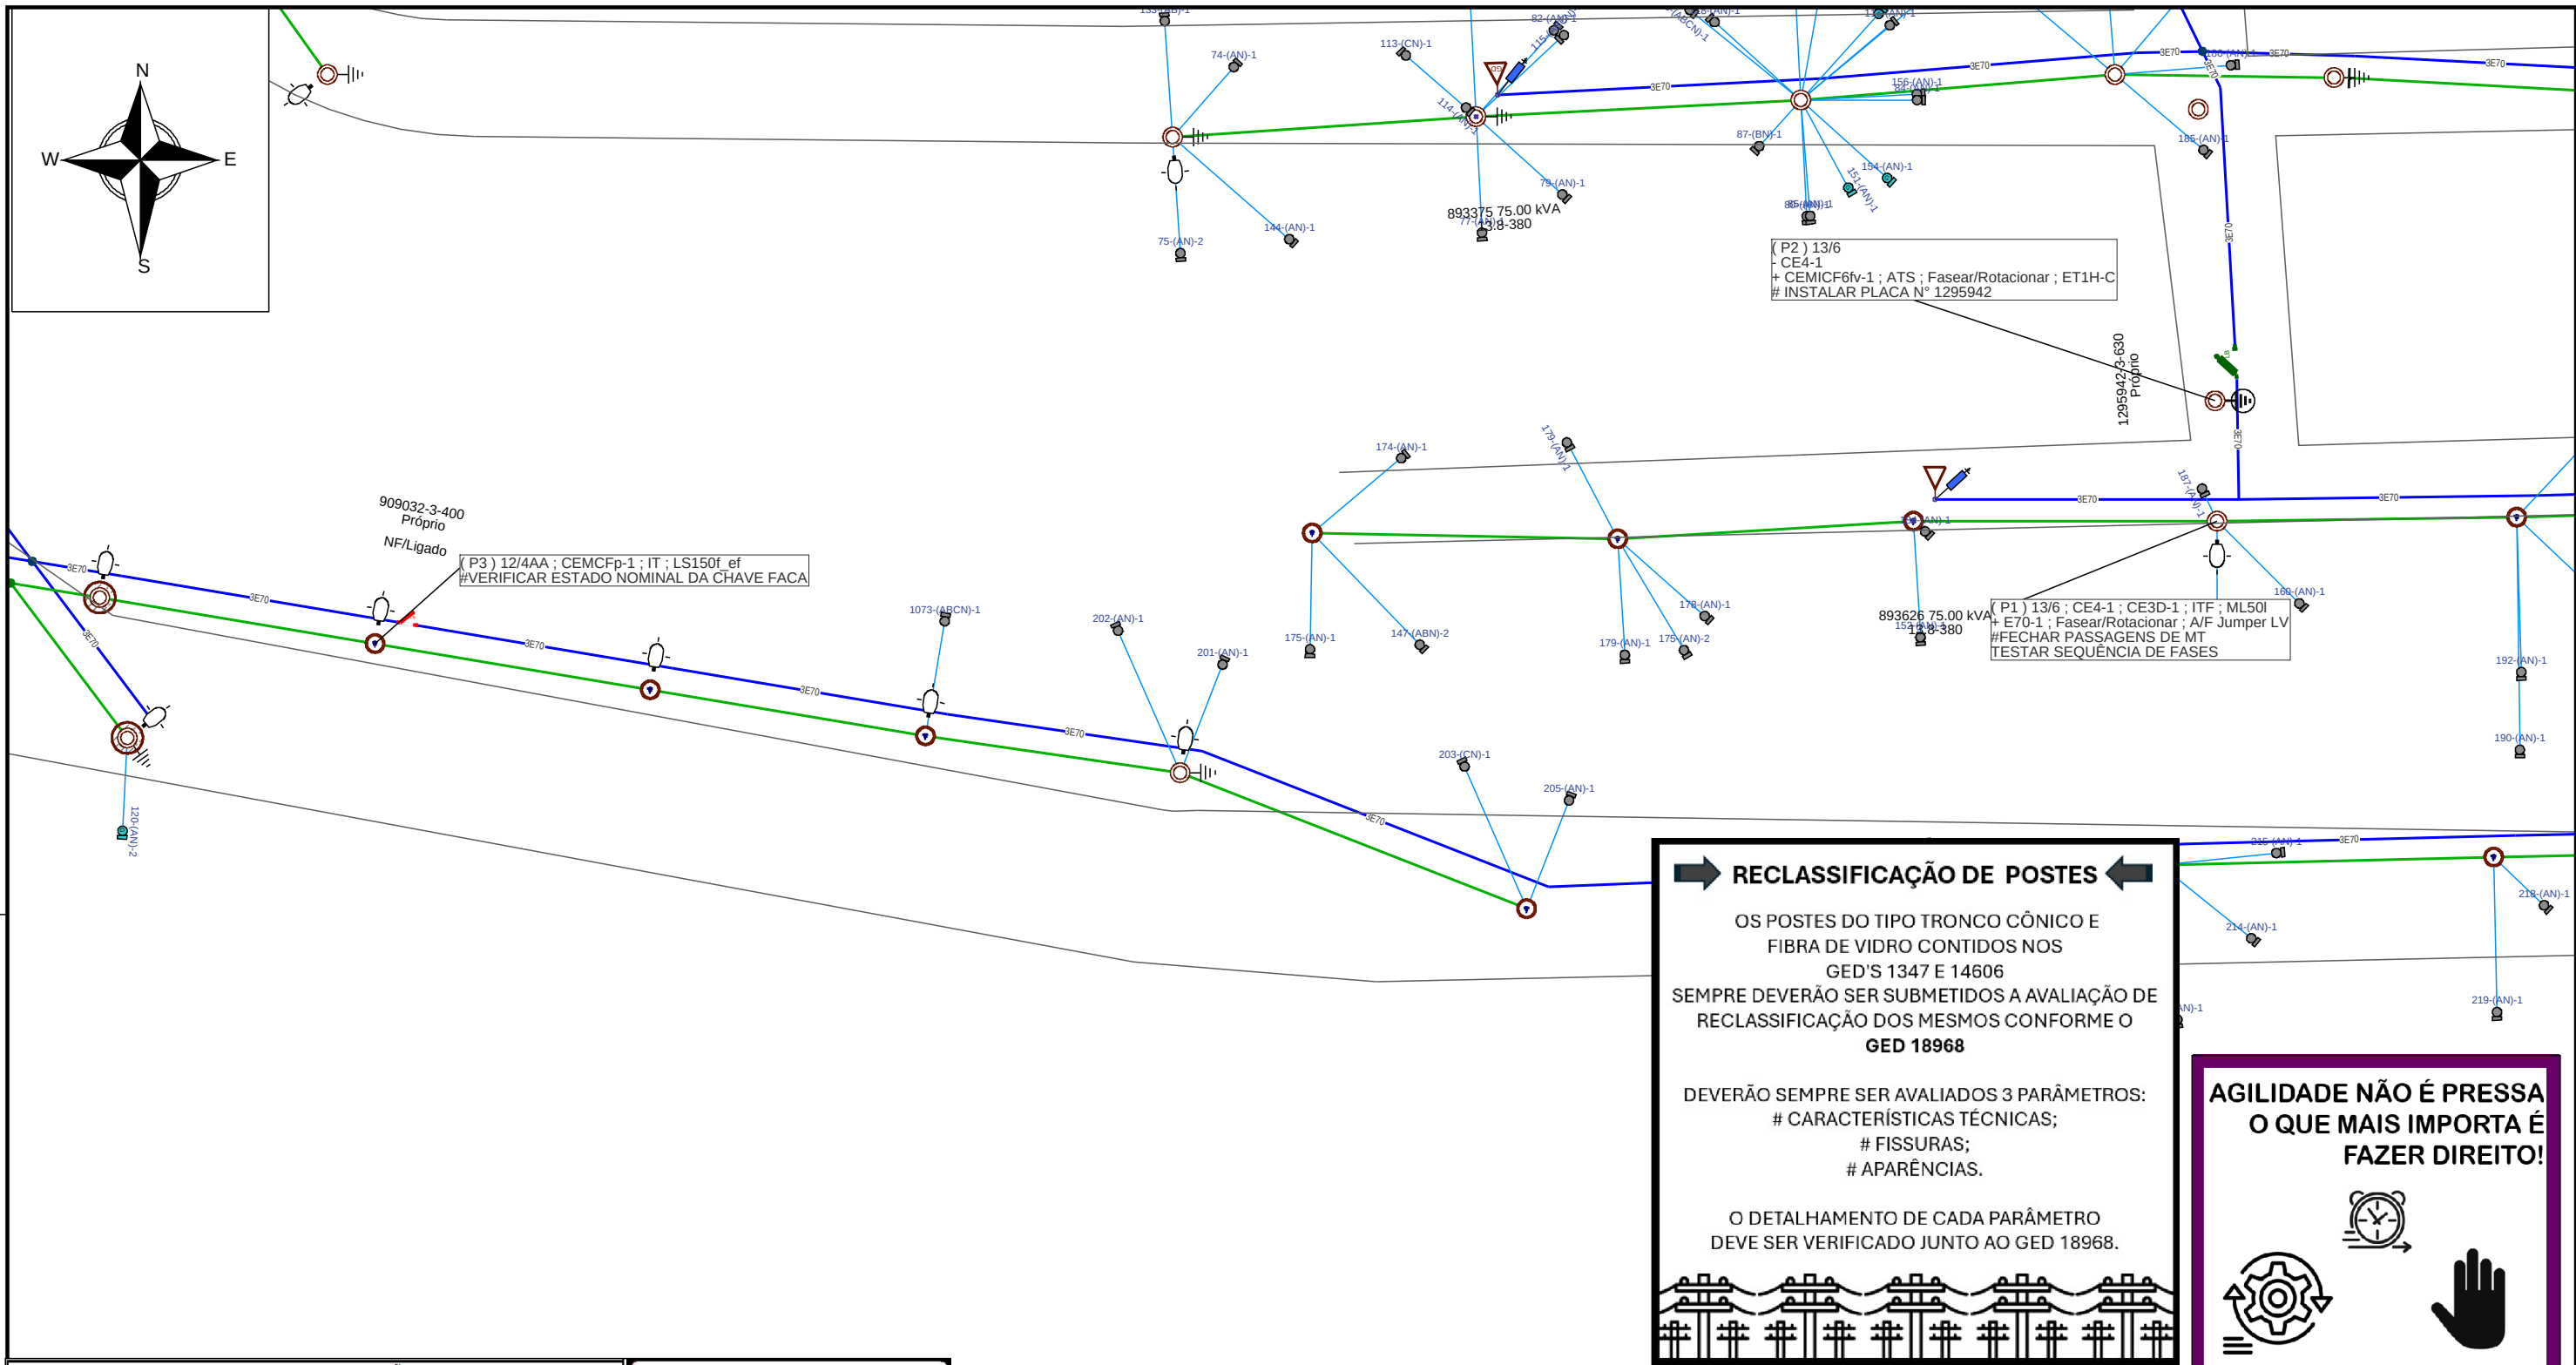

RECLASSIFICAÇÃO DE POSTES

OS POSTES DO TIPO TRONCO CÔNICO E FIBRA DE VIDRO CONTIDOS NOS GED'S 1347 E 14606 SEMPRE DEVERÃO SER SUBMETIDOS A AVALIAÇÃO DE RECLASSIFICAÇÃO DOS MESMOS CONFORME O **GED 18968**

DEVERÃO SEMPRE SER AVALIADOS 3 PARÂMETROS:

- # CARACTERÍSTICAS TÉCNICAS;
- # FISSURAS;
- # APARÊNCIAS.

O DETALHAMENTO DE CADA PARÂMETRO DEVE SER VERIFICADO JUNTO AO GED 18968.

**AGILIDADE NÃO É PRESSA
O QUE MAIS IMPORTA É
FAZER DIREITO!**

PLANO DE EXECUÇÃO					
PLANEJAR E PREPARAR OBRA, REALIZAR AS ATIVIDADES COM INTERVENÇÃO NA REDE DE MT, EM REGIME DE LINHA VIVA.					
Ação	Equipamento	Número	Clientes	Duração	CHI
					0
					0
					0
					0
					0
Linha Viva?		Sim	CHI TOTAL		0
☐ Poste novo a ser instalado (quando indicado em planta)					

FeedBack Para Fábrica de Projetos

DIEGO ROBERTO CHAVES FACHINETTO
Gerência de Processos de Obras e Manutenção | DROP
Técnico de Análise e Projetos
CFT: 015.390.420-81

Gerência de Obras e Manutenção
Município: Caxias do Sul

Cliente: RGE SUL DISTRIBUIDORA DE ENERGIA S.A

Obra: REGULARIZAÇÃO DE CLANDESTINOS

Endereço: R A LOT VENETO, BR RS

Responsável Técnico:

Eng. Ederson Paulo Vogel
CREA: RS135794 ART: 10911826

Escala: 1:850

Classe de isolamento: 15kV

Projetista: DIEGO ROBERTO

Data: 03/12/2025

AL: CXA12

Projeto: 000007937525

Nota: 000007158123

Folha 1

Levantador: ALESSANDRO SEVERO