

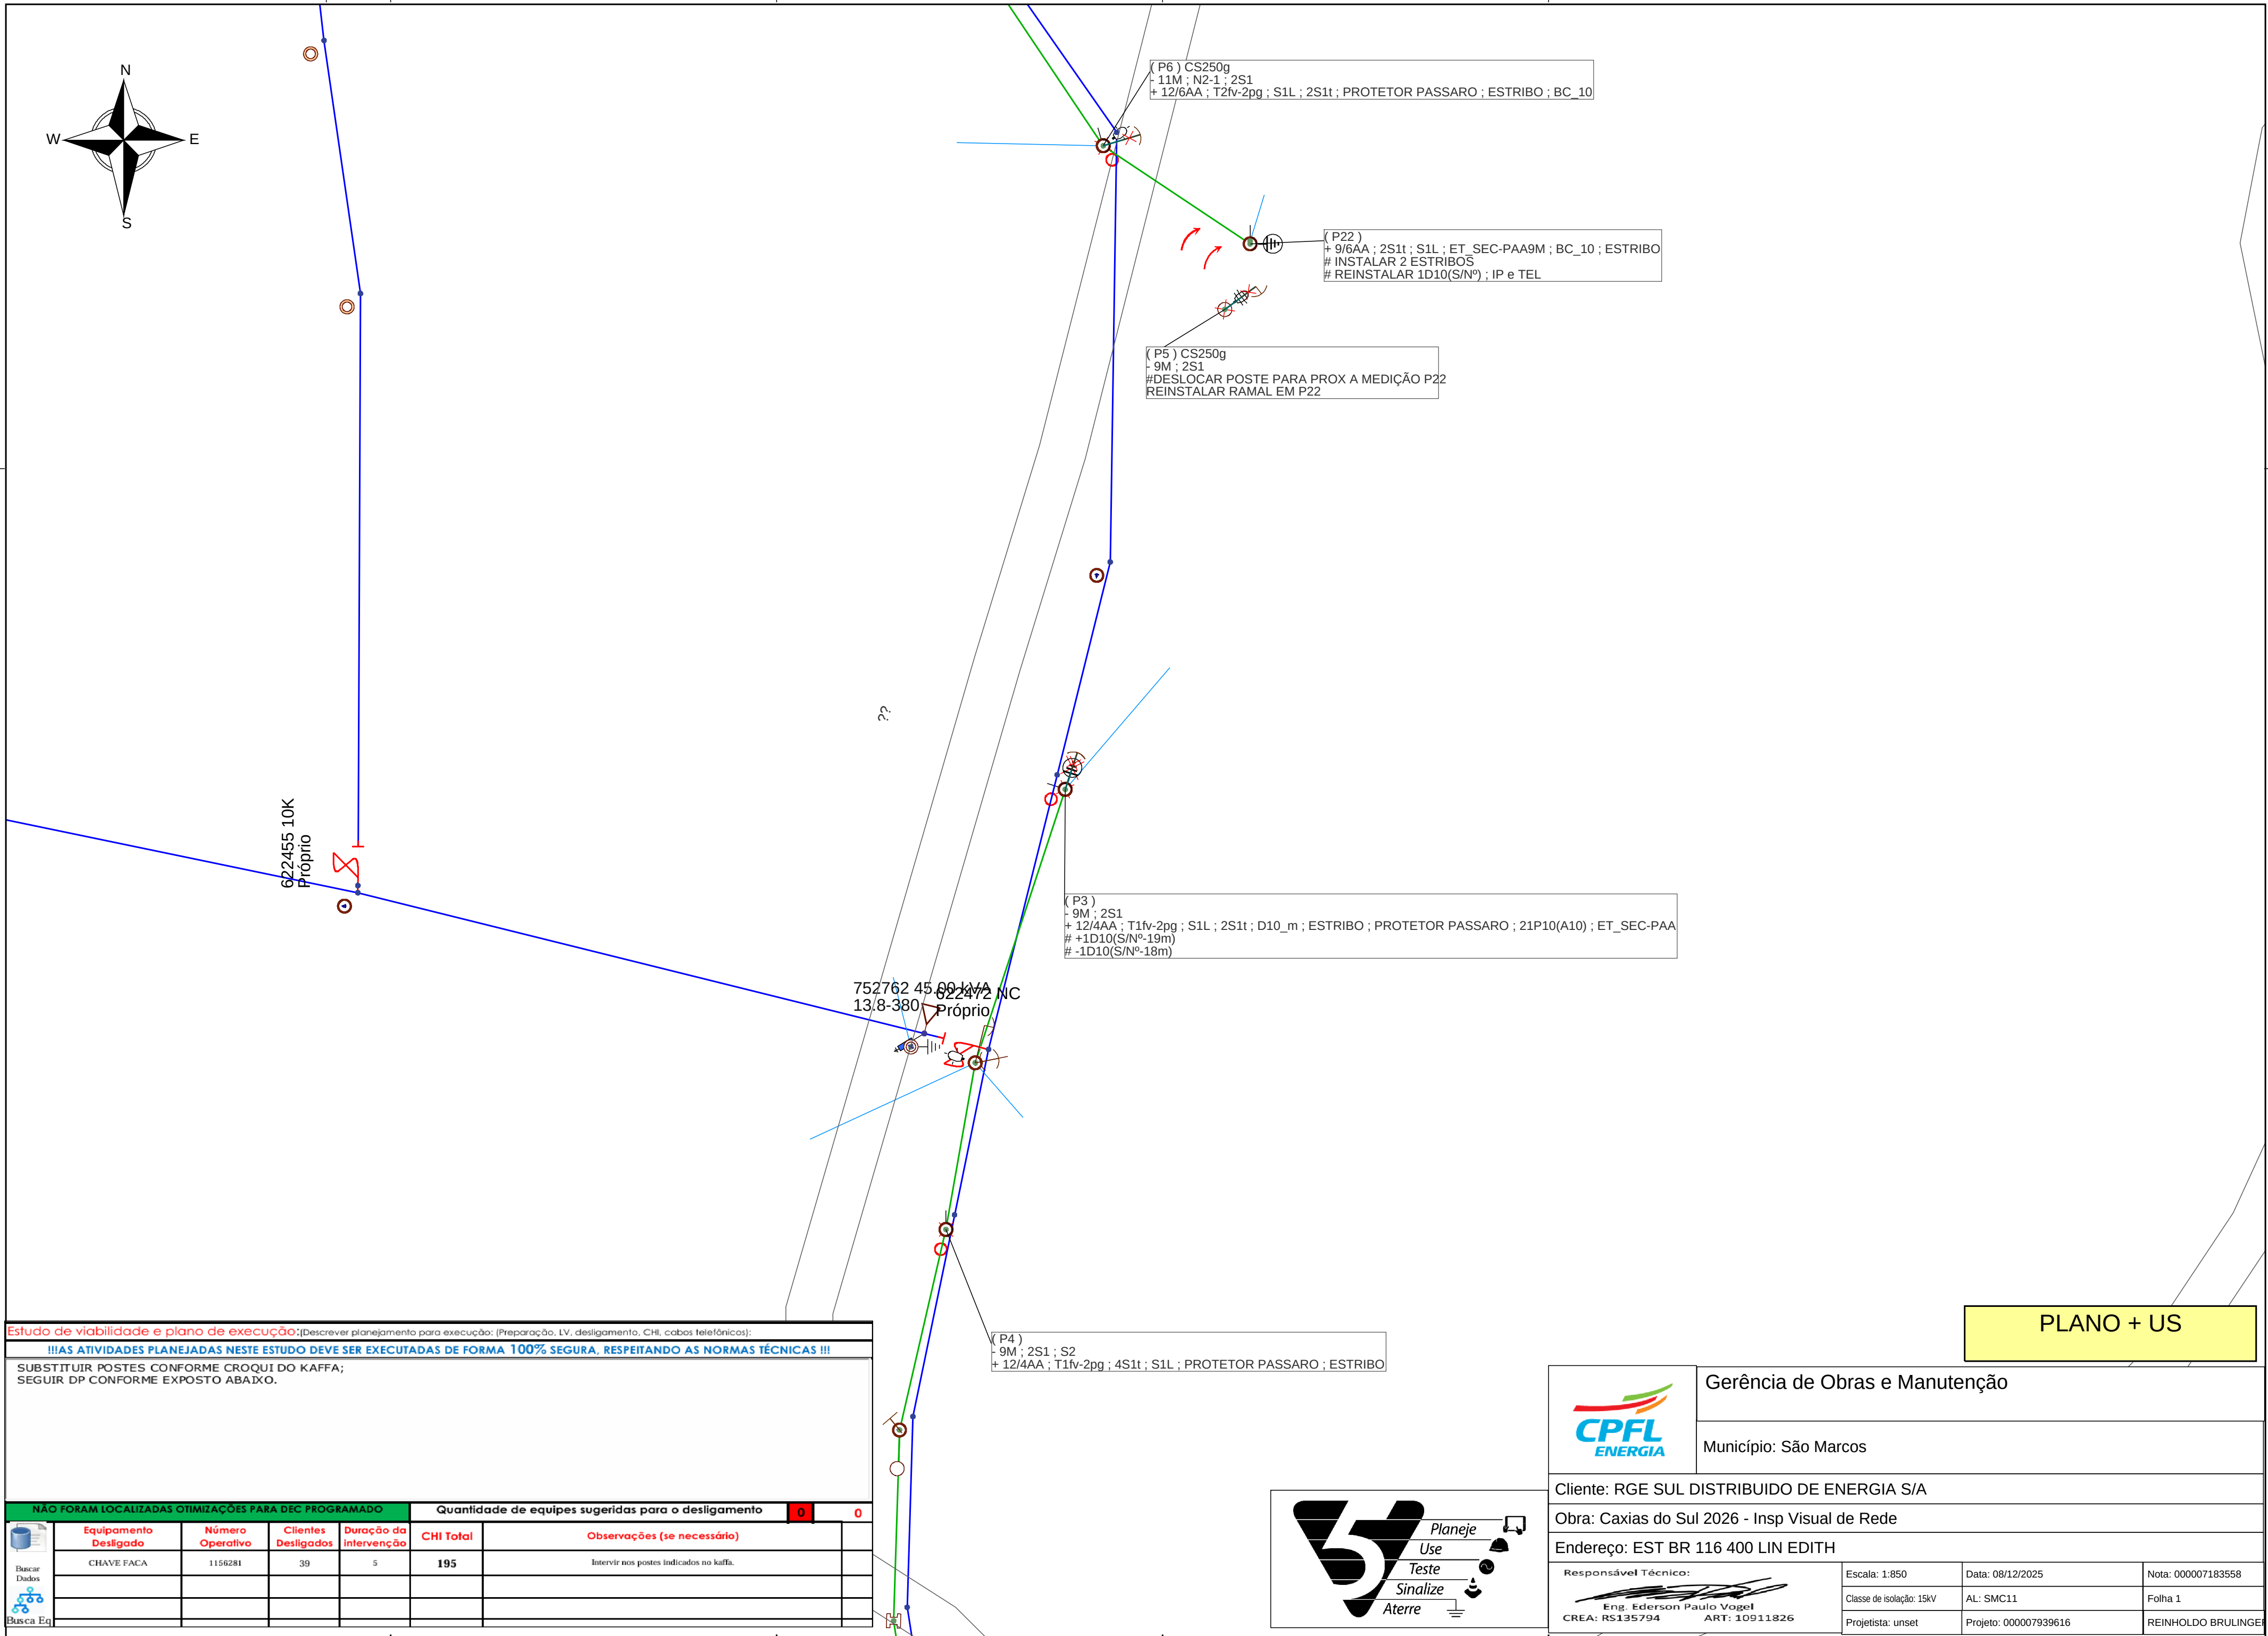


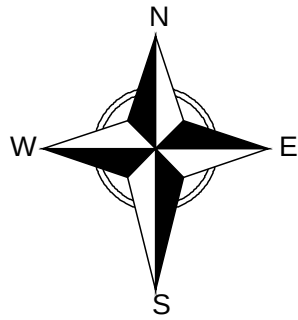

Estudo de viabilidade e plano de execução: (Descrever planejamento para execução: (Preparação, LV, desligamento, CHI, cabos telefônicos):						
!!!AS ATIVIDADES PLANEJADAS NESTE ESTUDO DEVE SER EXECUTADAS DE FORMA 100% SEGURA, RESPEITANDO AS NORMAS TÉCNICAS !!!						
SUBSTITUIR POSTES CONFORME CROQUI DO KAFFA; SEGUIR DP CONFORME EXPOSTO ABAIXO.						
NÃO FORAM LOCALIZADAS OTIMIZAÇÕES PARA DEC PROGRAMADO				Quantidade de equipes sugeridas para o desligamento		
 Buscar Dados	Equipamento Desligado	Número Operativa	Clientes Desligados	Duração da Intervenção	CHI Total	Observações (se necessário)
	CHAVE FACA	1156281	39	5	195	Intervir nos postes indicados no kaiffa.
Busca Eq						

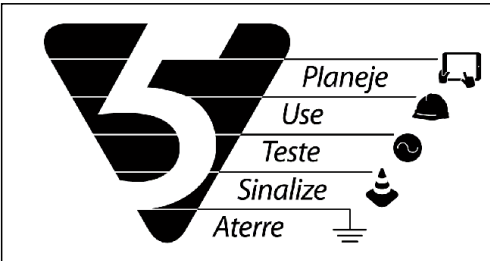

	Gerência de Obras e Manutenção		
	Município: São Marcos		
Cliente: RGE SUL DISTRIBUIDO DE ENERGIA S/A			
Obra: Caxias do Sul 2026 - Insp Visual de Rede			
Endereço: EST BR 116 400 LIN EDITH			
Responsável Técnico:  Eng. Ederson Paulo Vogel CREA: RS135794 ART: 10911826	Escala: 1:850	Data: 08/12/2025	Nota: 000007183558
	Classe de isolamento: 15kV	AL: SMC11	Folha 1
	Projetista: unset	Projeto: 000007939616	REINHOLDO BRULINGER