



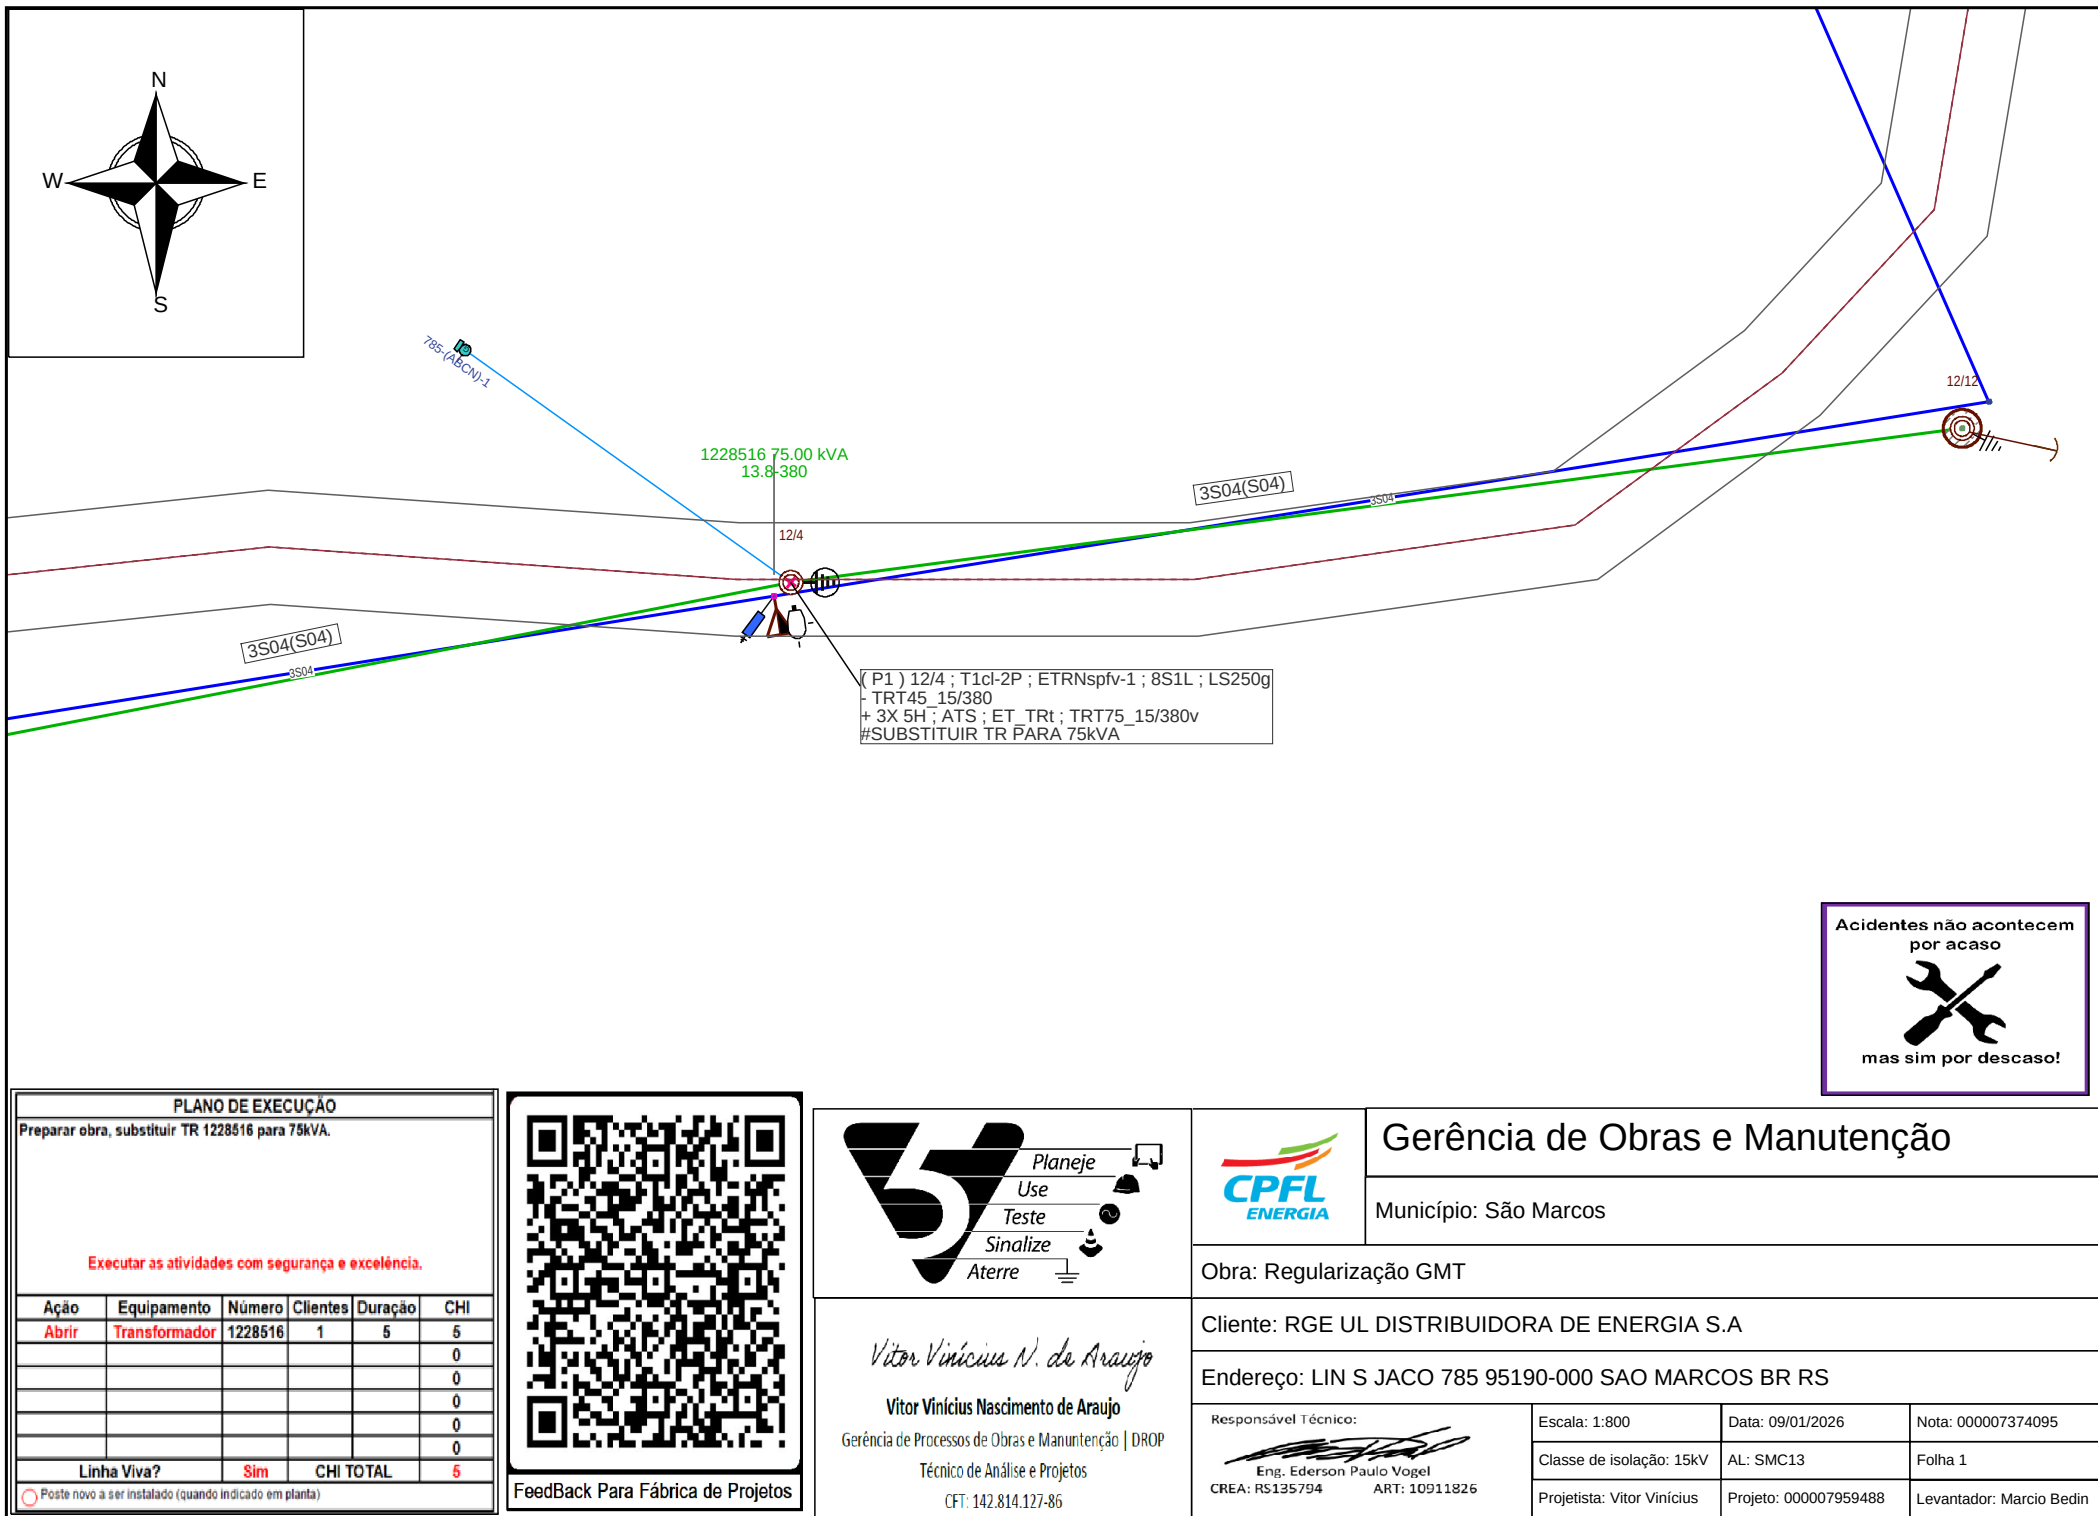

PLANO DE EXECUÇÃO					
Preparar obra, substituir TR 1228516 para 75kVA.					
Executar as atividades com segurança e excelência.					
Ação	Equipamento	Número	Clientes	Duração	CHI
Abrir	Transformador	1228516	1	5	5
					0
					0
					0
					0
					0
Linha Viva?		Sim	CHI TOTAL		5
☐ Poste novo a ser instalado (quando indicado em planta)					

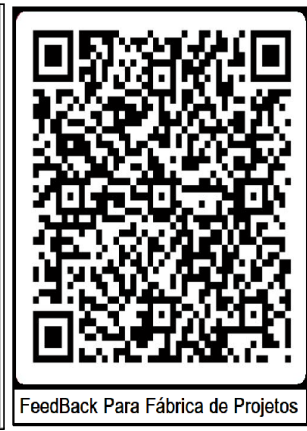

Planeje
Use
Teste
Sinalize
Aterre

Gerência de Obras e Manutenção

Município: São Marcos

Obra: Regularização GMT

Cliente: RGE UL DISTRIBUIDORA DE ENERGIA S.A

Endereço: LIN S JACO 785 95190-000 SAO MARCOS BR RS

Responsável Técnico:	Escala: 1:800	Data: 09/01/2026	Nota: 000007374095
Eng. Ederson Paulo Vogel CREA: RS135794 ART: 10911826	Classe de isolamento: 15kV	AL: SMC13	Folha 1
	Projetista: Vitor Vinicius	Projeto: 000007959488	Levantador: Marcio Bedin

Vitor Vinicius N. de Araujo

Vitor Vinicius Nascimento de Araujo

Gerência de Processos de Obras e Manutenção | DROP

Técnico de Análise e Projetos

CPF: 142.814.127-86