


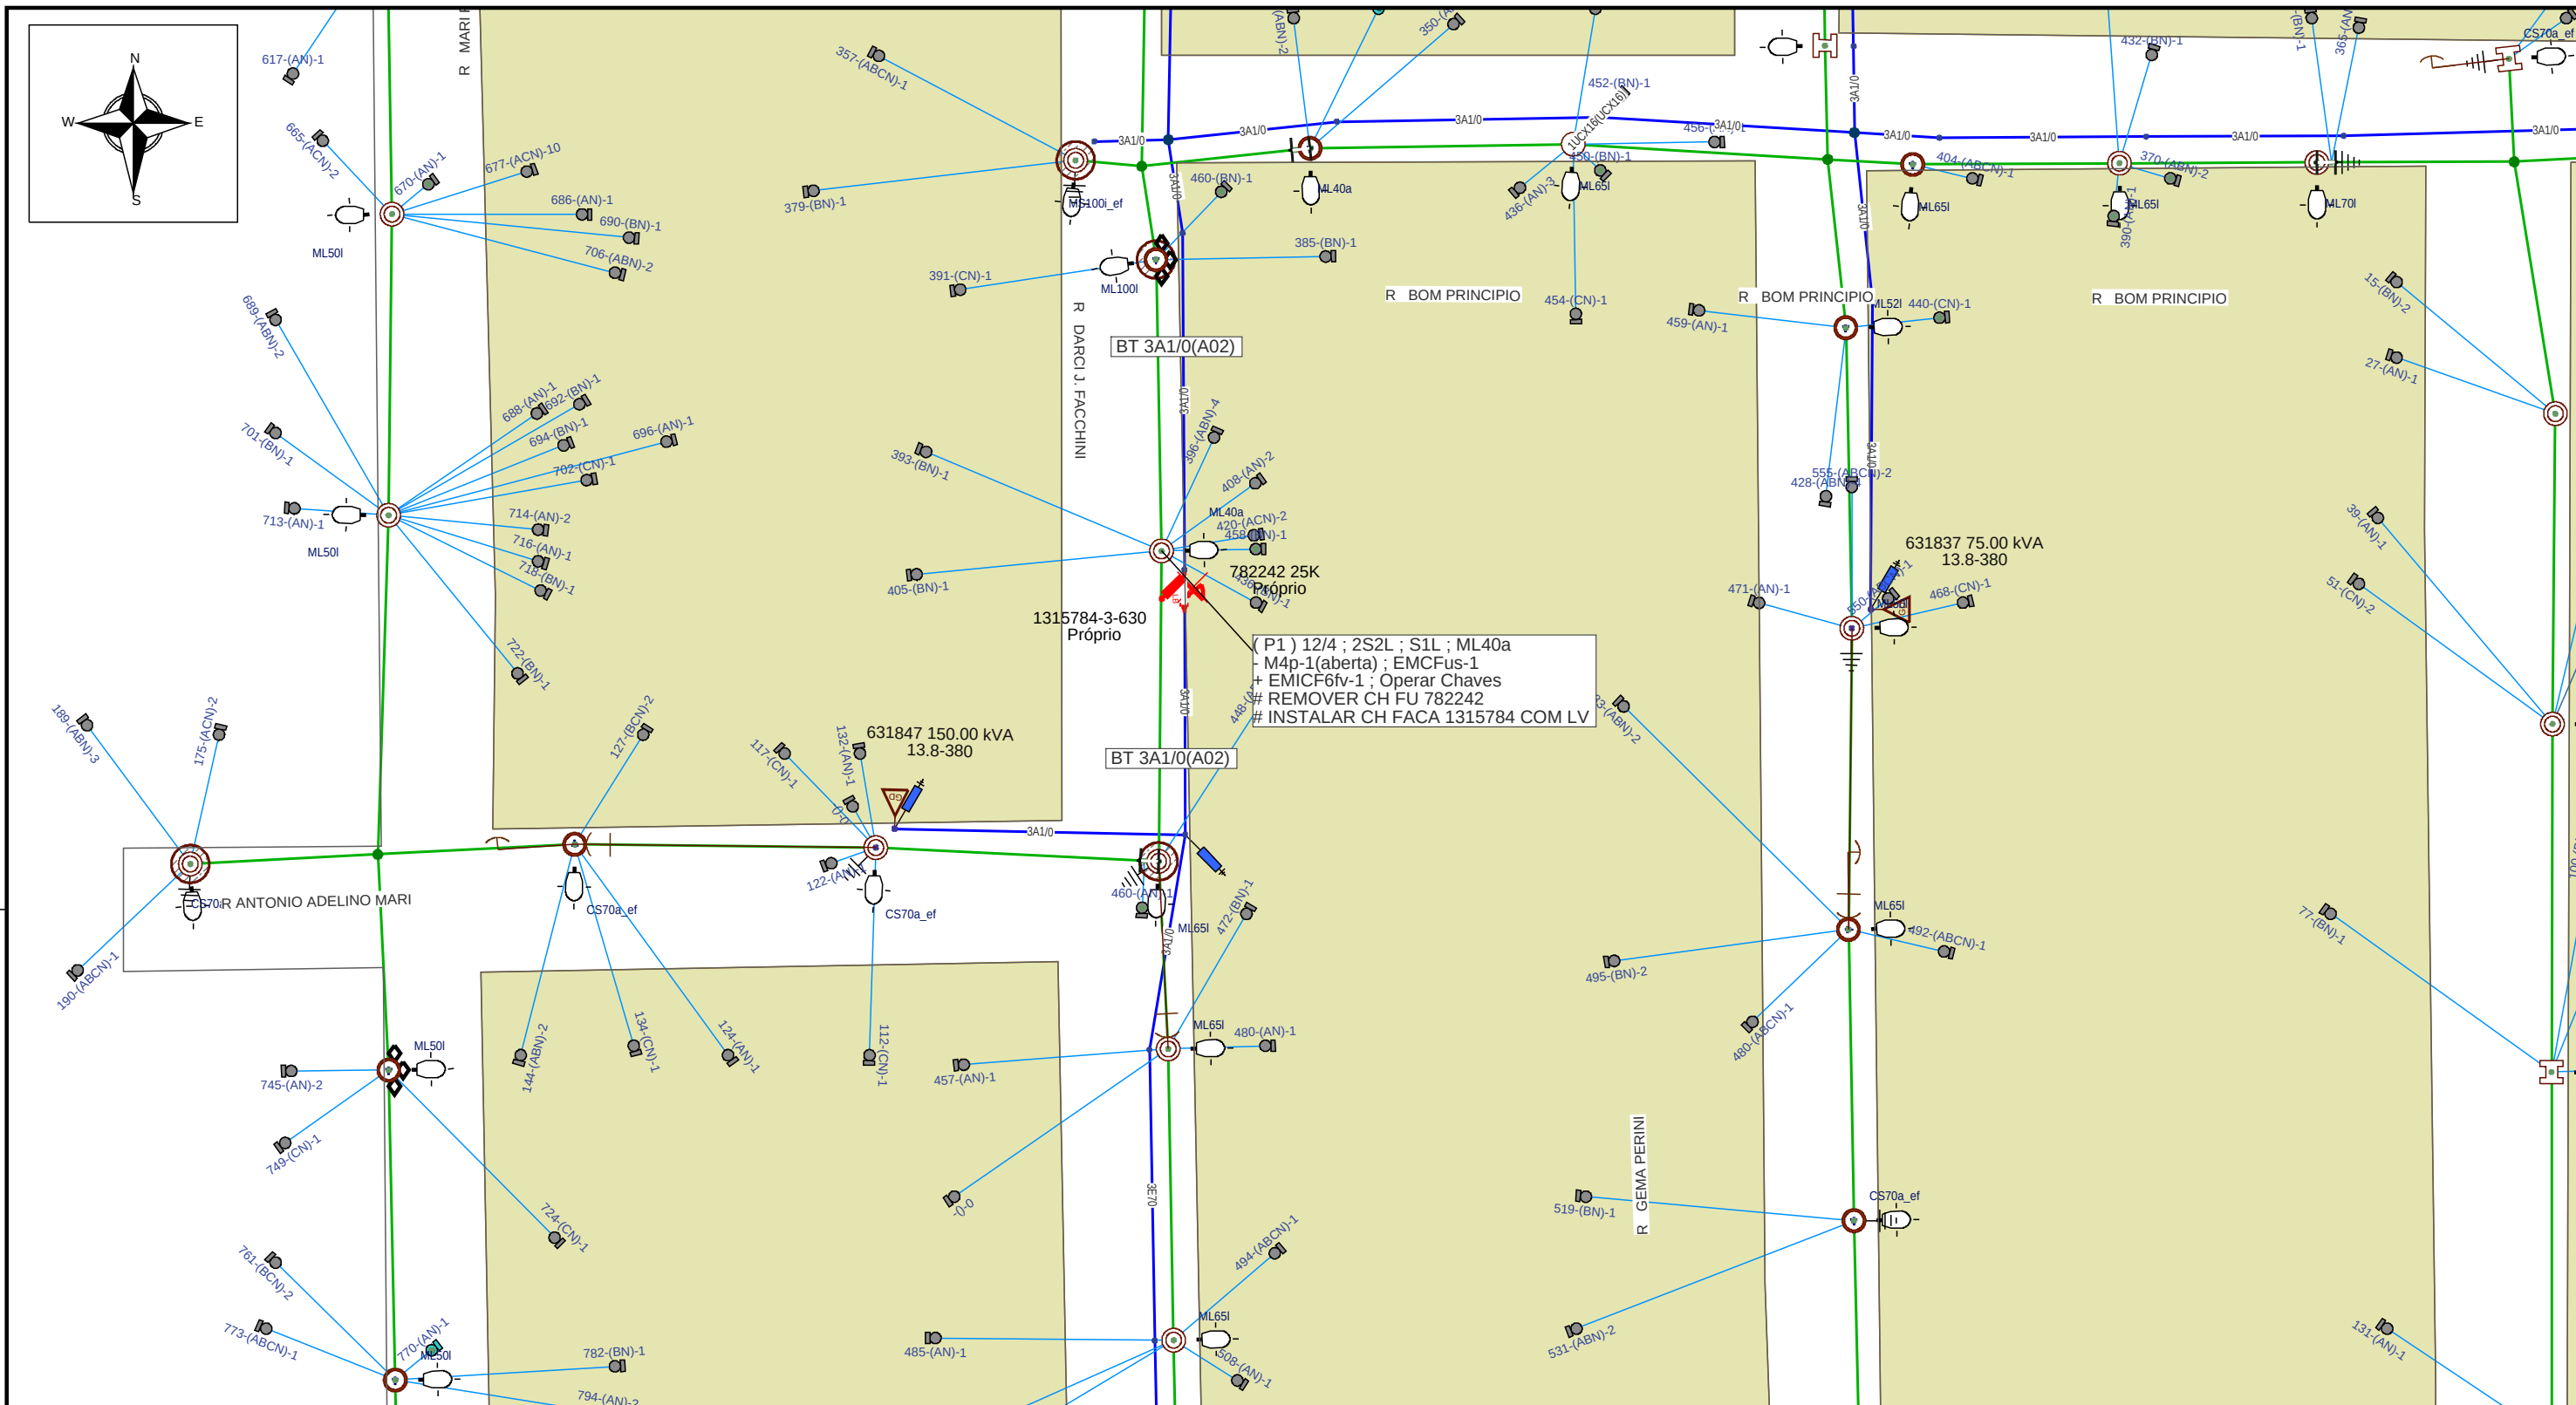

PLANO DE EXECUÇÃO

Executar atividades com segurança, respeitando normas e orientações
Substituir no P1 CH FU 782242 por CH FACA 1315784, com LV
Instalar e atualizar placas de número operativo, conforme projeto
Recolher resíduos após o término das obras

Qualquer alteração, solicitar via Desing I


Ação	Equipamento	Número	Clientes	Duração	CHI
Abriu	Transformador	940634	93	4	372
					0
					0
					0
					0
					0

Linha Viva? **Sim** CHI TOTAL **372**

Poste novo a ser instalado (quando indicado em planta)



FeedBack Para Fábrica de Projetos

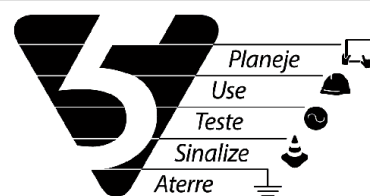

Diego Souza Ribeiro

DIEGO SOUZA RIBEIRO
Gerência de Processos de Obras e Manutenção | DROP
Técnico de Análise e Projetos

CFT: 021.824.880-65



Gerência de Obras e Manutenção

Município: CAXIAS DO SUL

Cliente: RGE SUL DISTRIBUIDORA DE ENERGIA S.A

Obra: 089-2026_AP_CONF_INT_RER-CGA_AL CXH44

Endereço: R DARCI JOAO FACCHINI 396 - CAXIAS DO SUL BR RS

Responsável Técnico:

Eng. Ederson Paulo Vogel
CREA: RS135794 ART: 10911826

Escala: 1:700

Classe de isolamento:
15kV

Projetista: DIEGO
RIBEIRO

Data: 23/01/2026

AL: CXH44

Projeto: 000007966789

Nota:
000007399726

Folha 1

Levantador: RICARDO
Q. DE ALBUQUERQUE