


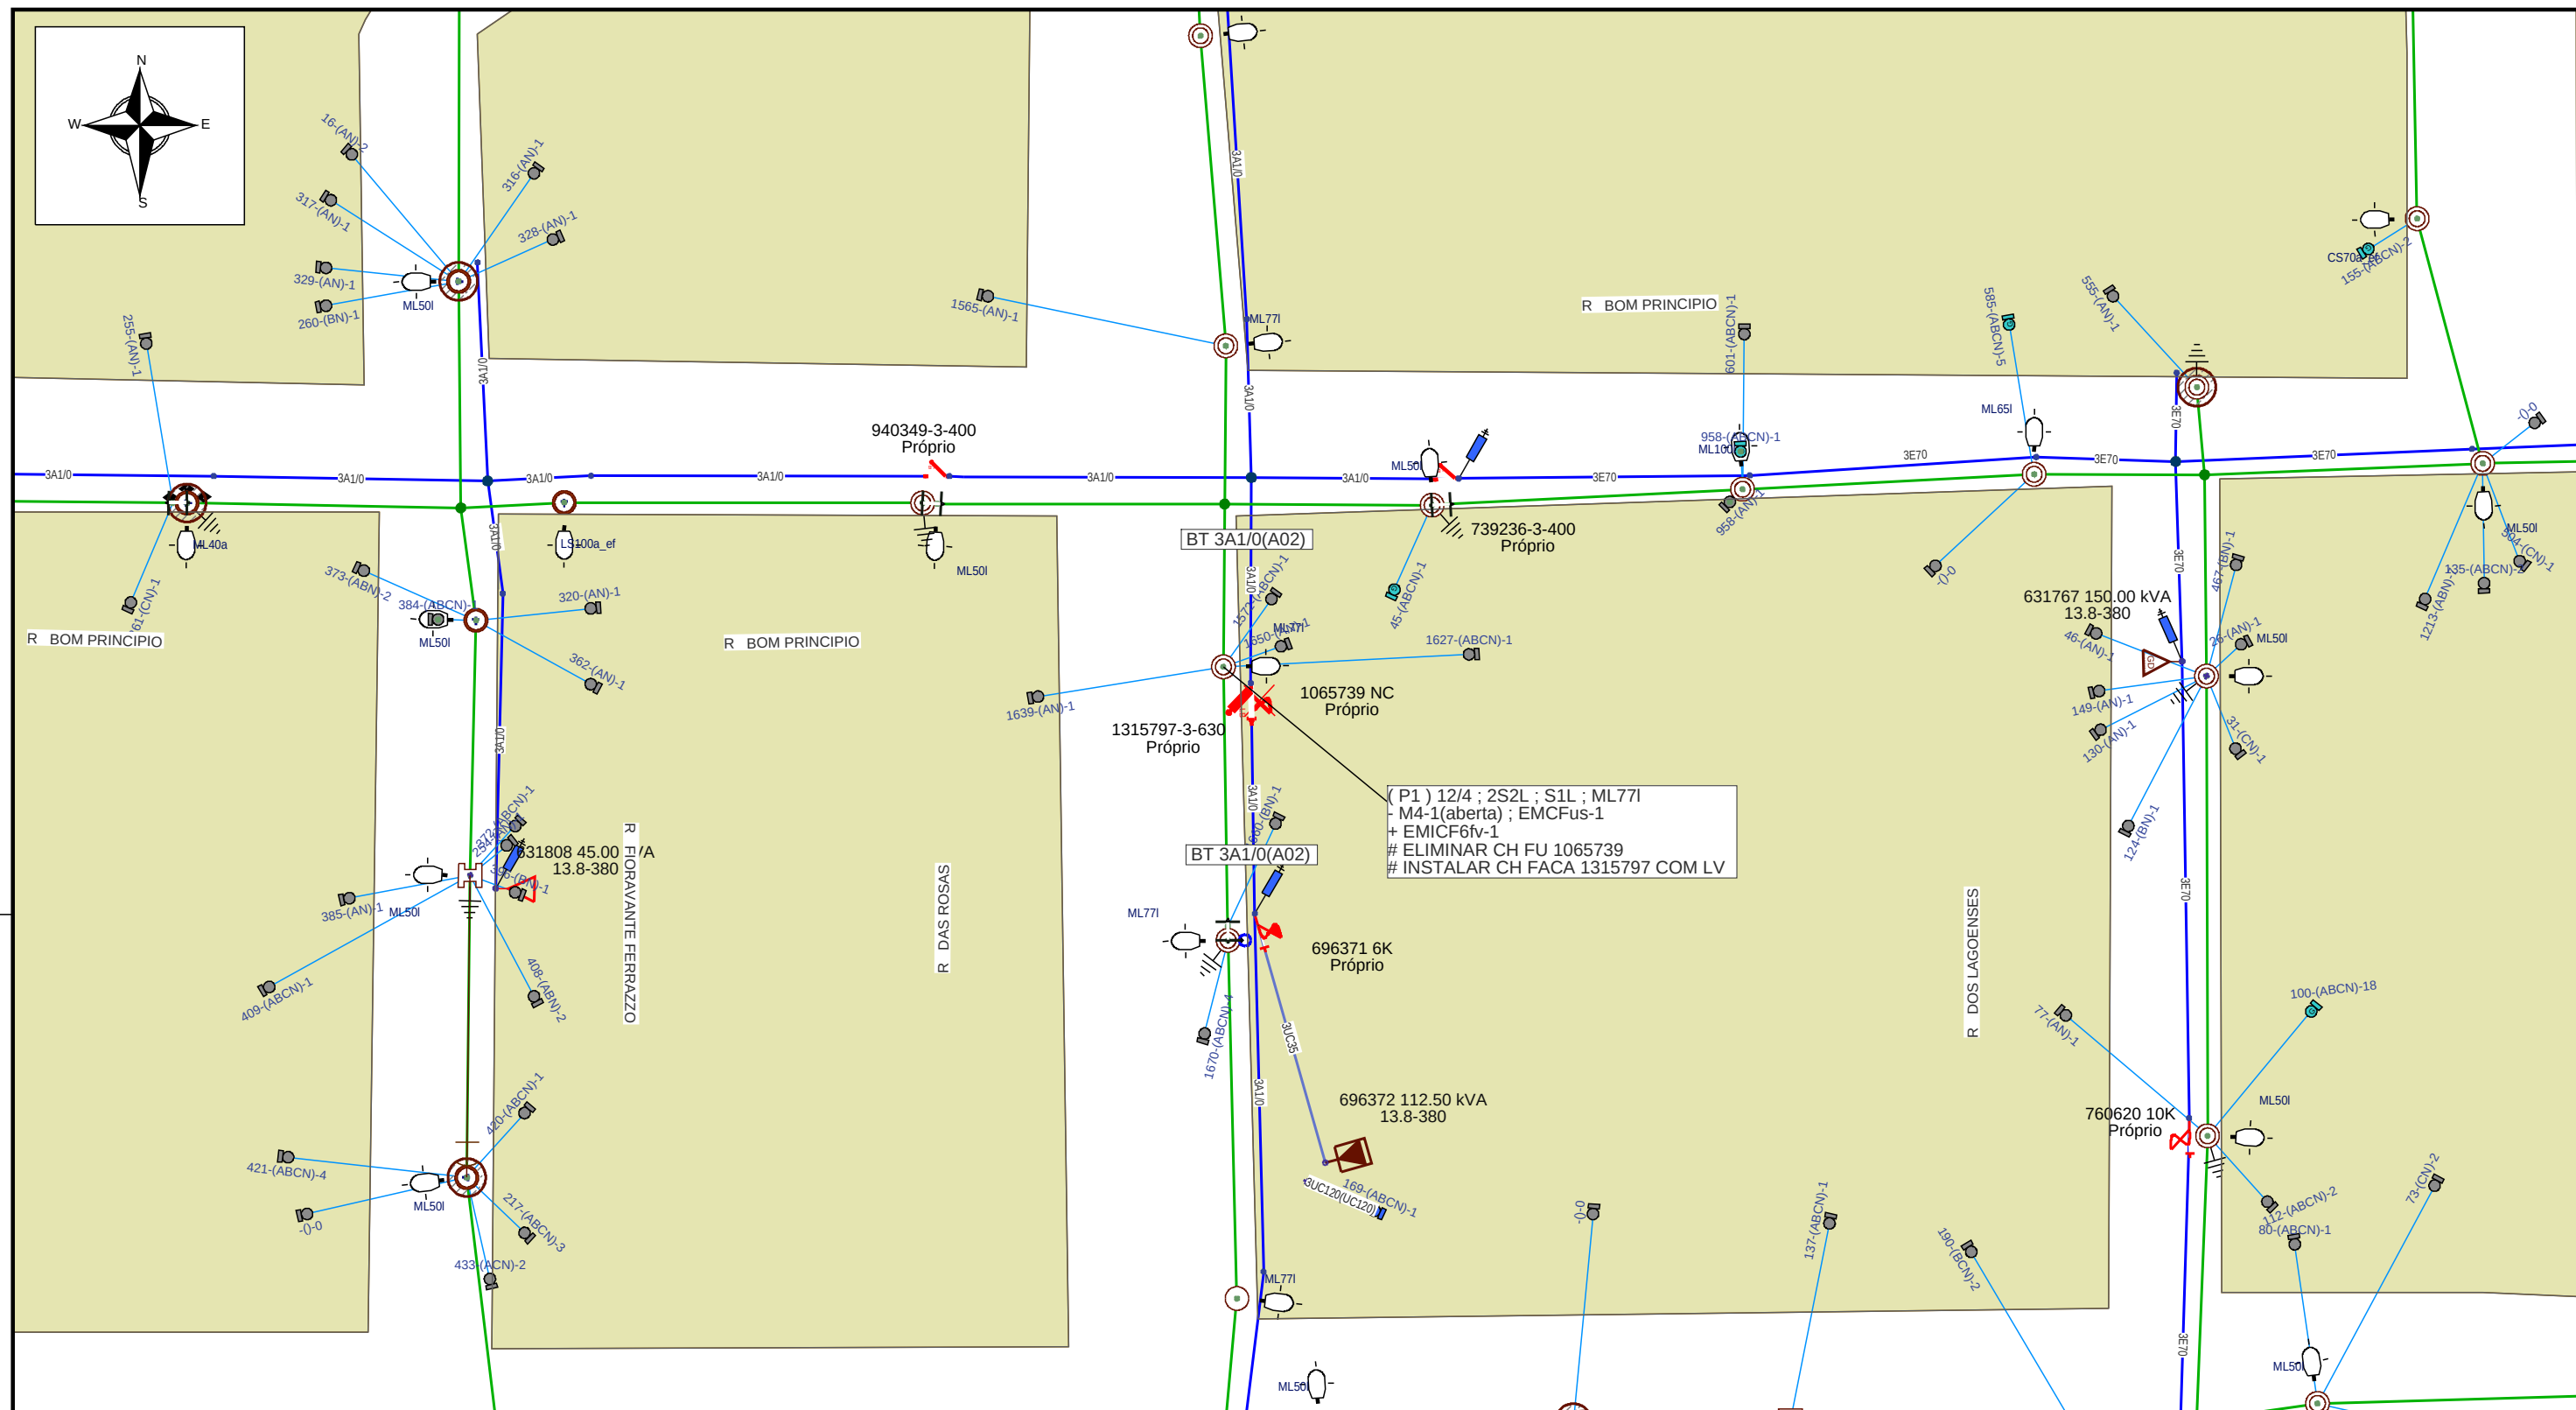

PLANO DE EXECUÇÃO

Executar atividades com segurança, respeitando normas e orientações

Substituir no P1 CH FU 1065739 por CH FACA 1315797 com LV
Instalar e atualizar placas de número operativo, conforme projeto
Realizar podas/abates/aceiros conforme projeto

Qualquer alteração, solicitar via Desing I


Ação	Equipamento	Número	Clientes	Duração	CHI
Abriu	Transformador	944801	28	4	112
					0
					0
					0
					0
					0
Linha Viva?	Sim	CHI TOTAL	112		

Poste novo a ser instalado (quando indicado em planta)

R. DAS FLORES



FeedBack Para Fábrica de Projetos

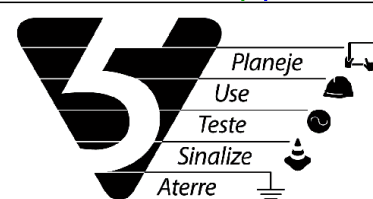

Diego Souza Ribeiro

DIEGO SOUZA RIBEIRO

Gerência de Processos de Obras e Manutenção | DROP

Técnico de Análise e Projetos

CFT: 021.824.880-65



Gerência de Obras e Manutenção

Município: CAXIAS DO SUL

Cliente: RGE SUL DISTRIBUIDORA DE ENERGIA S.A

Obra: 089-2026_AP_CONF_INT_RER-CGA_AL CXH44

Endereço: R DAS ROSAS 1627 - CAXIAS DO SUL BR RS

Responsável Técnico:

Eng. Ederson Paulo Vogel
CREA: RS135794 ART: 10911826

Escala: 1:700

Classe de isolamento:
15kV

Projetista: DIEGO
RIBEIRO

Data: 23/01/2026

AL: CXH44

Projeto: 000007966791

Nota:
000007399792

Folha 1

Levantador: ADELAR
M.F GRAFE