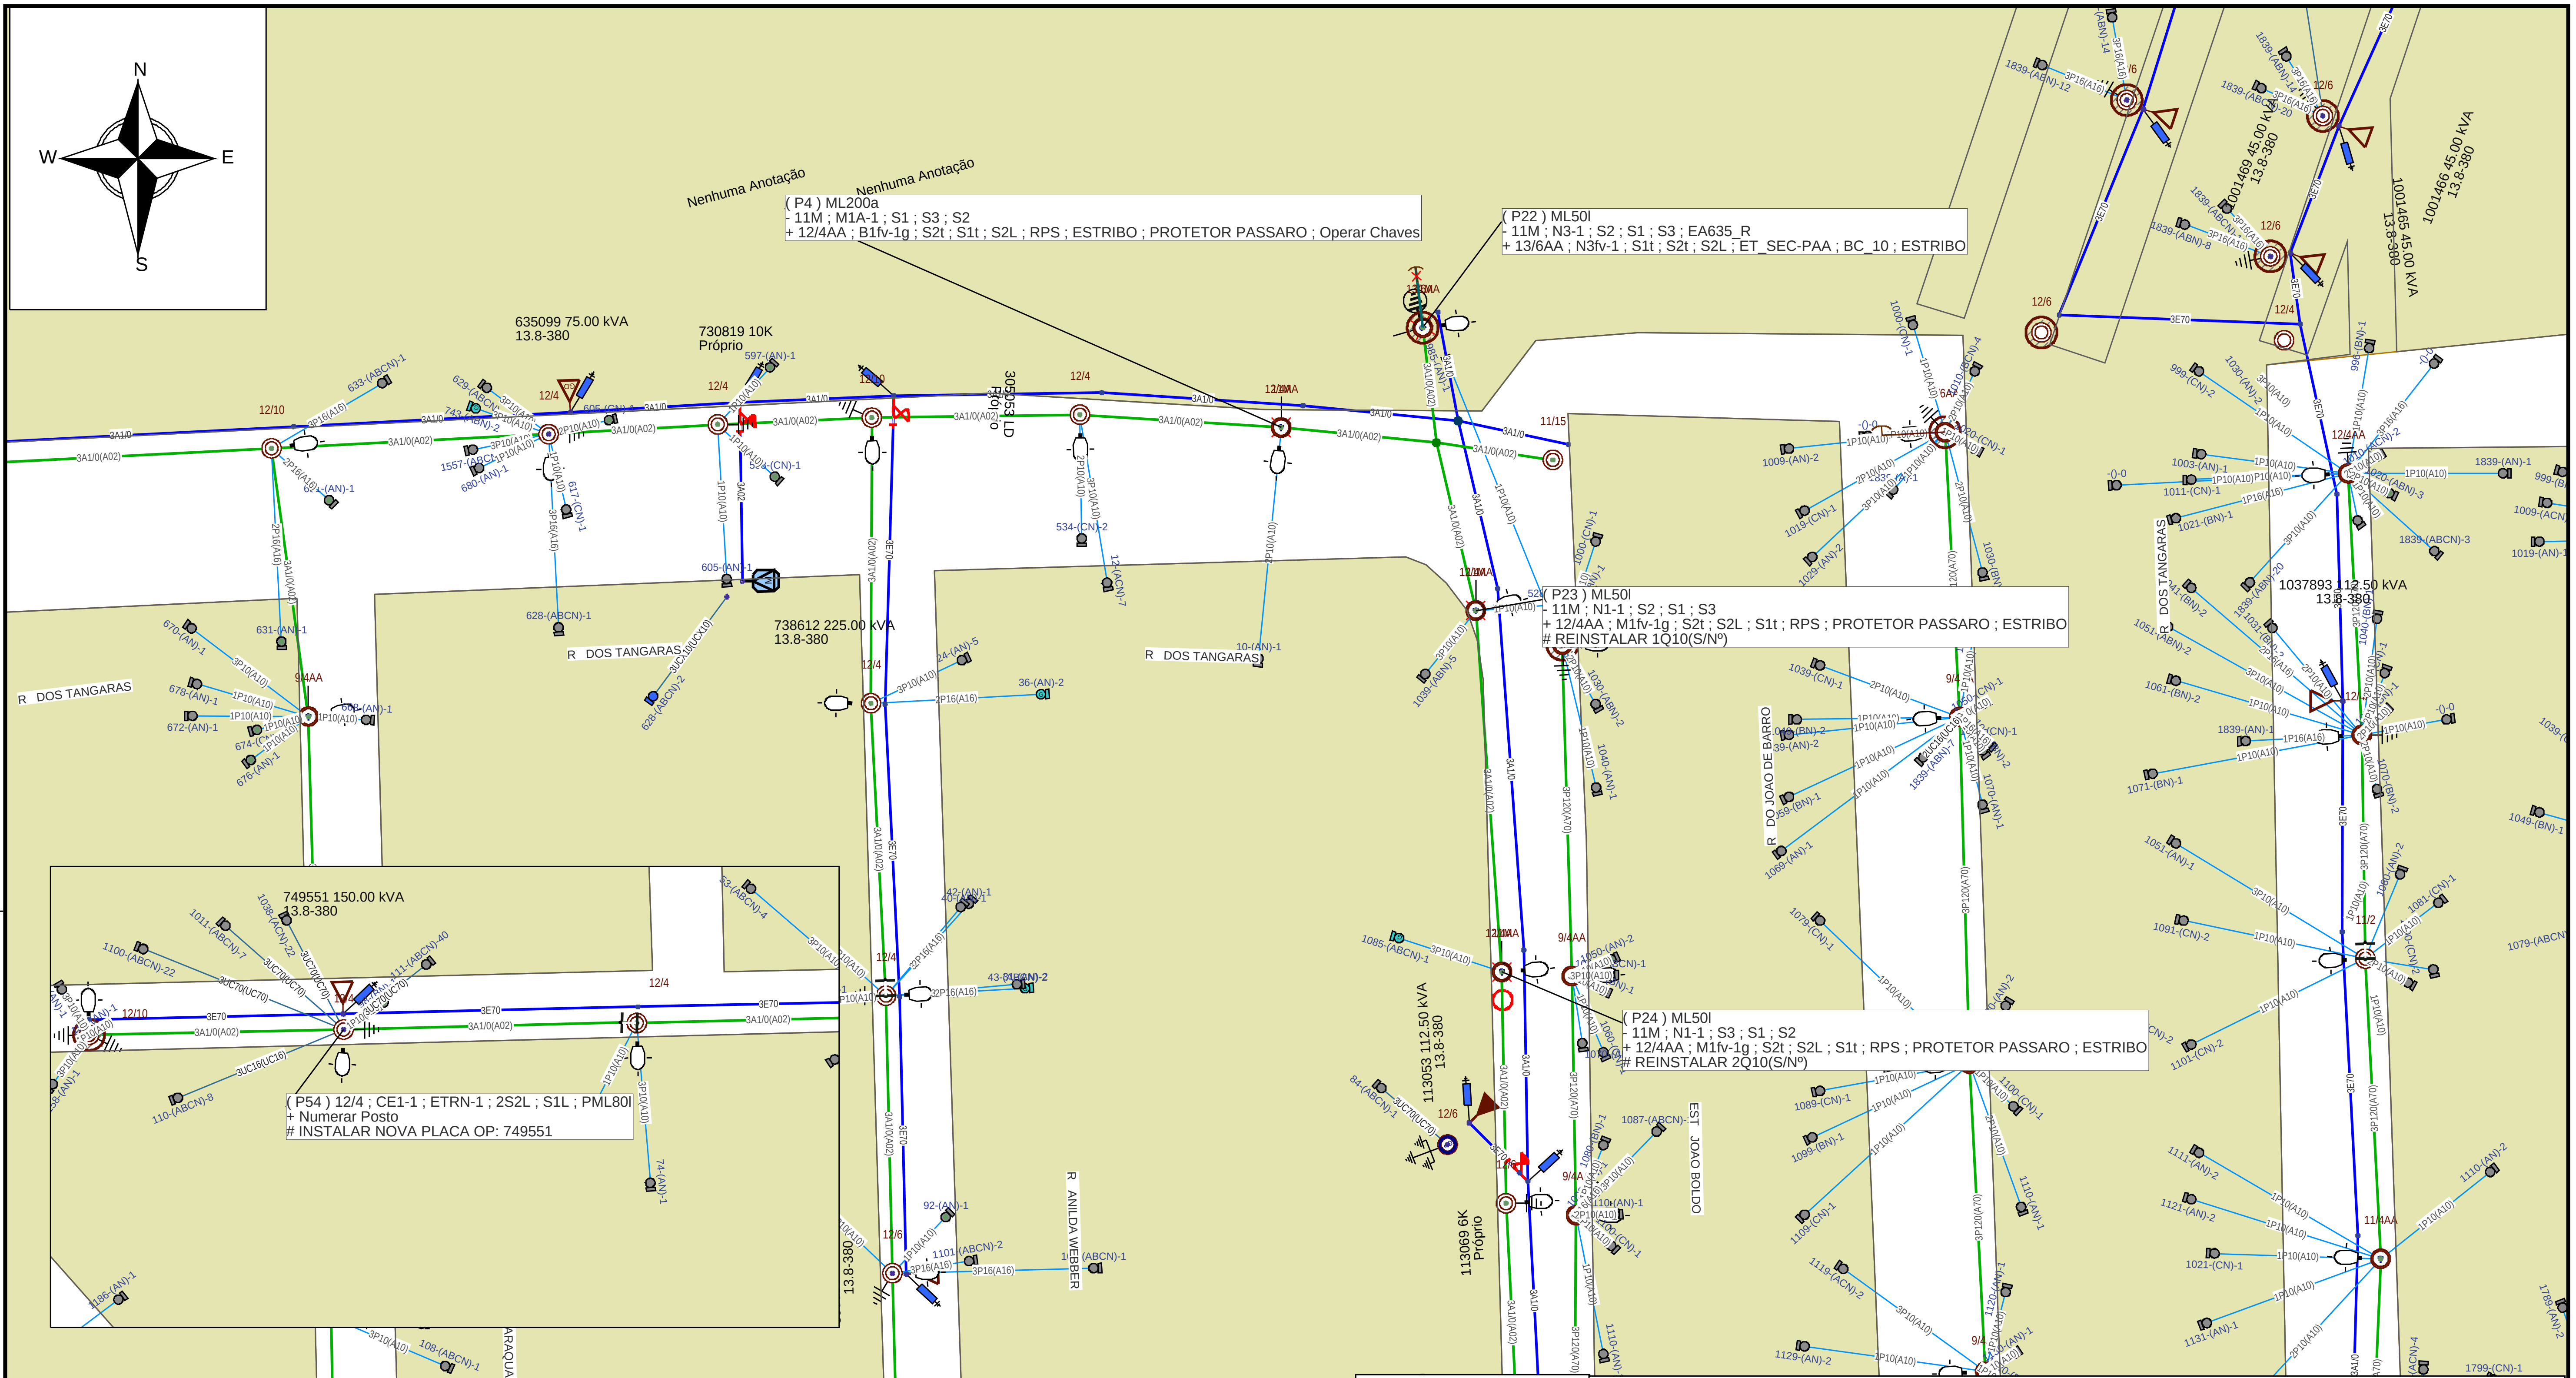

Intervir na rede confome grade de estudos abaixo para substituir as estruturas apontadas na planta kaffa;

O DEC EM ESTUDO PODE SER OTIMIZADO EM ATÉ 27,2 CHI					Quantidade de equipes sugeridas para o desligamento	##	###
Equipamento Desligado	Número Operativo	Clientes Desligados	Duração da intervenção	CHI Total	Observações (se necessário)		
TRANSFORMADOR	635099	73	4	292			
ESTUDO DE CHI			Total	292			

Buscar Dados
Busca Eq Pai
Criar Árvore
Pesquisa DB
Assistende de Manobra (Alfa)

PLANO + US

Planeje
Use
Teste
Sinalize
Aterre

CPFL ENERGIA

Gerência de Obras e Manutenção

Município: Caxias do Sul

Cliente: RGE SUL DISTRIBUIDORA DE ENERGIA S/A

Obra: Caxias do Sul 2026 - Insp Visual de Rede

Endereço: TR VICTOR EMANUEL 10 - TVS V EMANUEL - CAXIAS DO SUL

Responsável Técnico: Eng. Ederson Paulo Vogel CREA: RS135794 ART: 10911826	Escala: 1:850	Data: 23/02/2026	Nota: 000007437009
	Classe de isolação: 15kV	AL: KCE16	Folha 1
	Projetista: Dani Mendonça	Projeto: 000007985810	Levantador: Ricardo Quevedo