
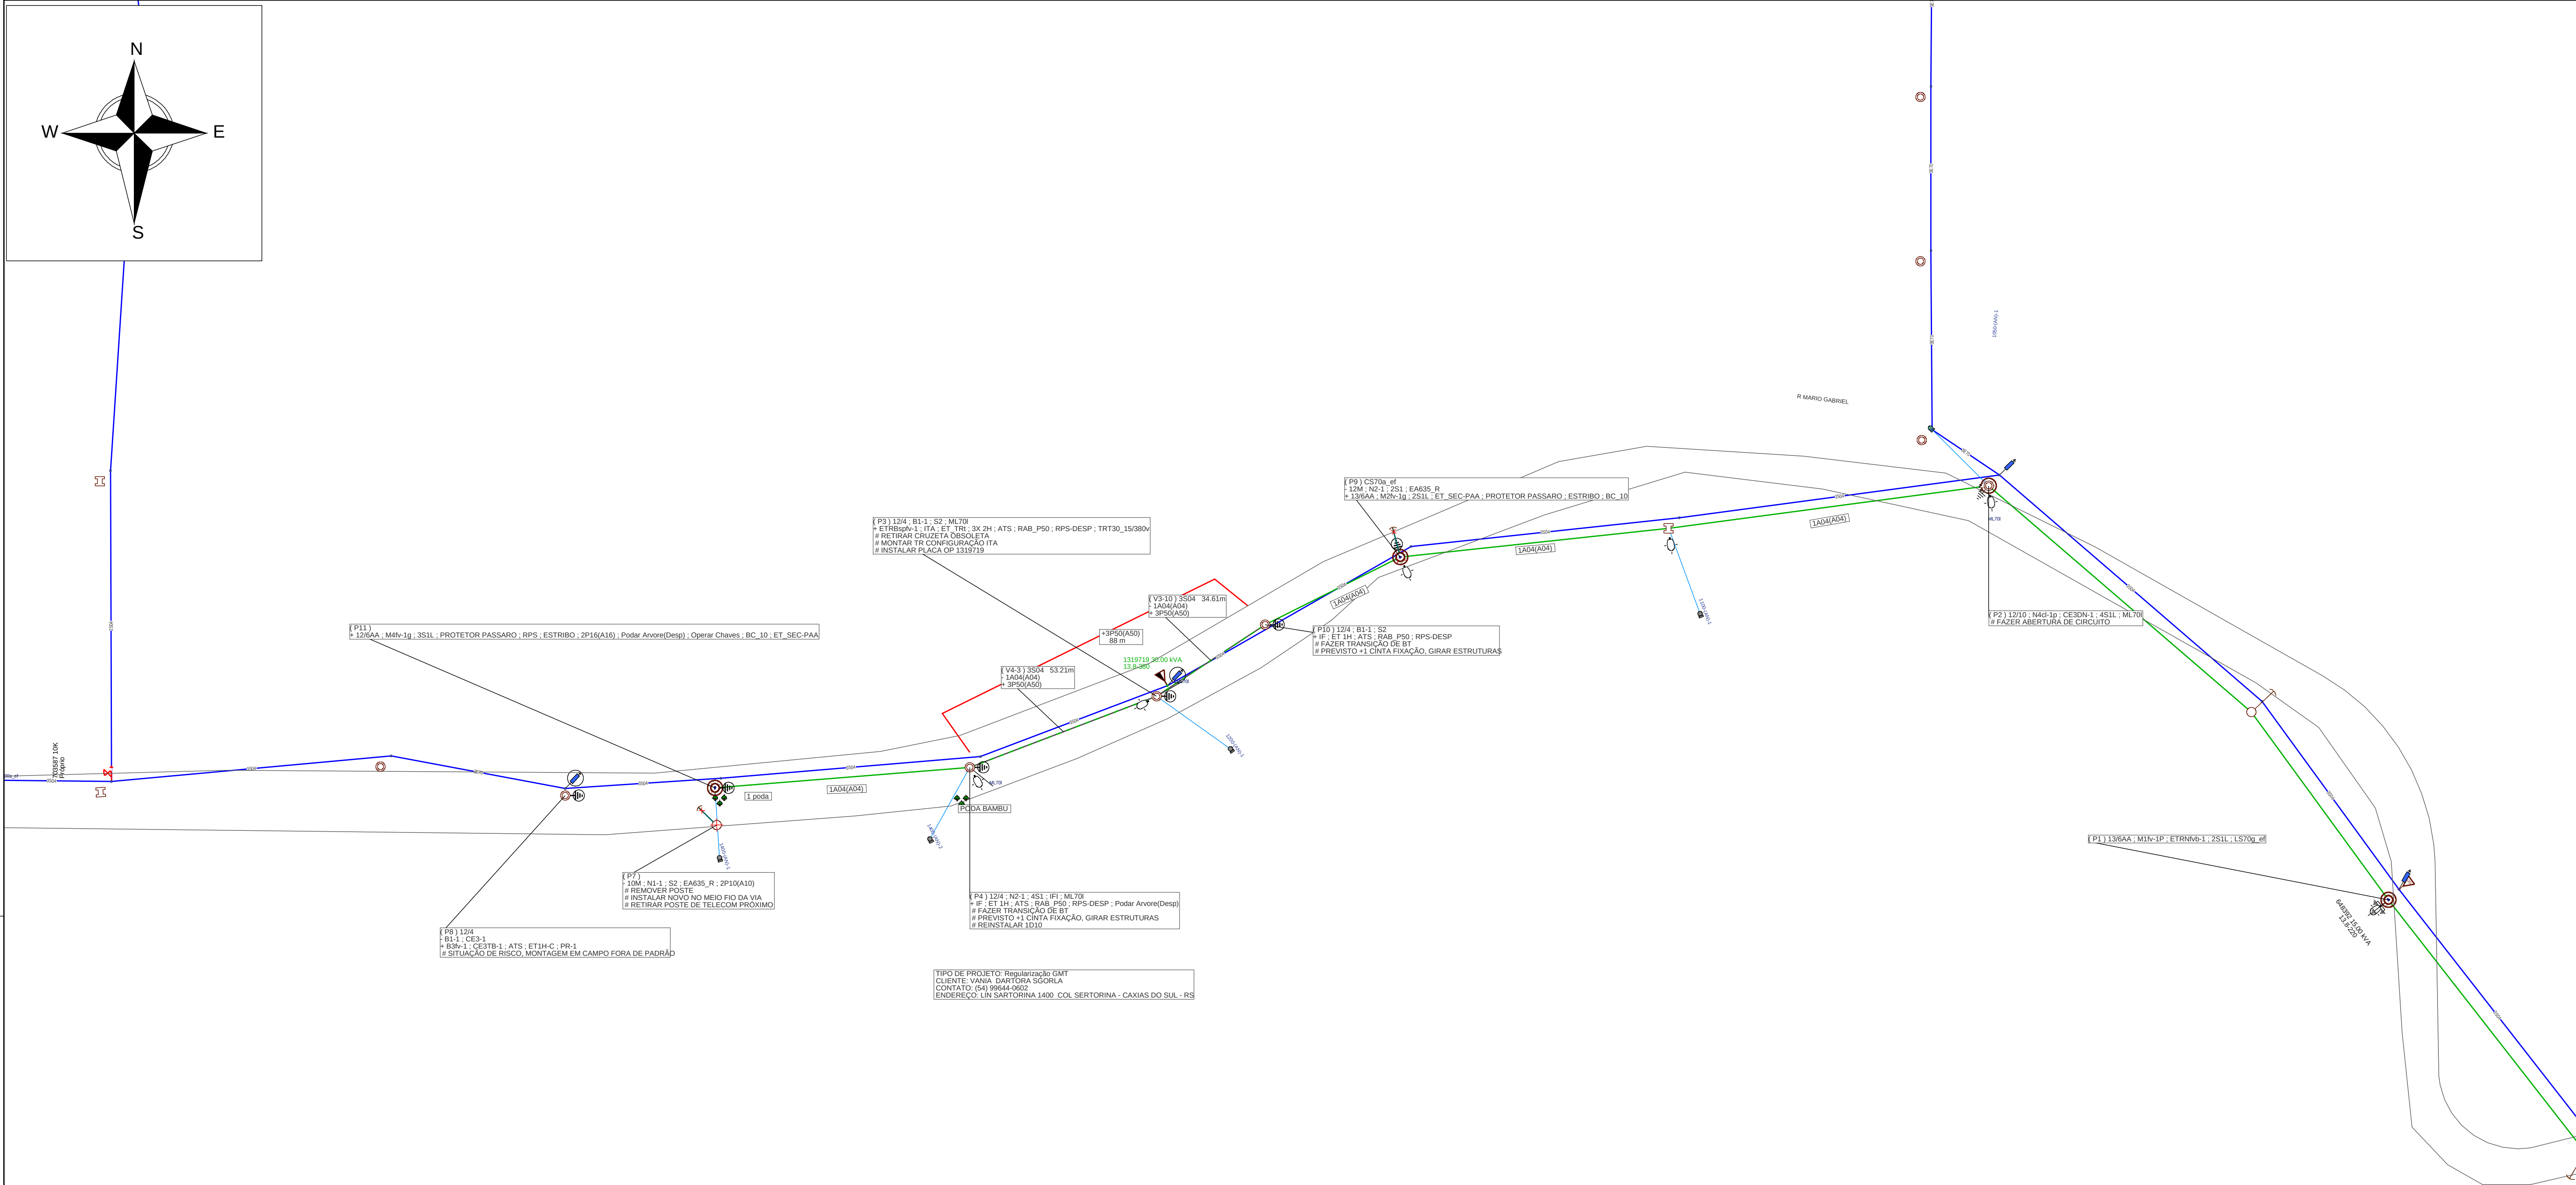


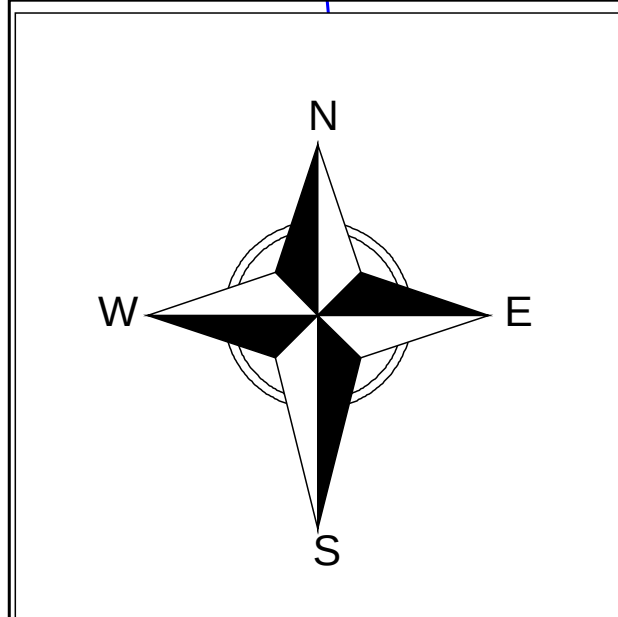

FeedBack Para Fábrica de Projetos

NA PREPARAÇÃO ABRIR CAVAS + IMPLANTAR POSTES NOVOS + PASSAR REDE PARA POSTE NOVO + ABRIR CHFUS 1050134 Se possível, na mesma programação podem ser executadas as seguintes notas 6620704, 300000954135, 300001058520,						
O DEC EM ESTUDO PODE SER OTIMIZADO EM ATÉ 187 CHI					Quantidade de equipes sugeridas para o desligamento	
					0	0
Equipamento	Número	Cientes	Duração da	CHI Total	Observações (se necessário)	
Desligado	Operativo	Desligados	intervenção			
CHAVE FACA	1050134	29	4	116		
Buscar Dados						
Busca Eq						
Par						
Criar Arvore						
Pesquisar						
Assinatura de Manobra (A3m)						
ESTUDO DE CHI			Total	116		

RECLASSIFICAÇÃO DE POSTES

OS POSTES DO TIPO TRONCO CÔNICO E FIBRA DE VIDRO CONTIDOS NOS GED'S 1347 E 14606 SEMPRE DEVERÃO SER SUBMETIDOS A AVALIAÇÃO DE RECLASSIFICAÇÃO DOS MESMOS CONFORME O GED 18968

DEVERÃO SEMPRE SER AVALIADOS 3 PARÂMETROS:

- # CARACTERÍSTICAS TÉCNICAS;
- # FISSURAS;
- # APARÊNCIAS.

O DETALHAMENTO DE CADA PARÂMETRO DEVE SER VERIFICADO JUNTO AO GED 18968.

Renan Maccari
Gerência de Obras e Manutenção Metropolitana
Técnico de Projetos
CFT: 8397107606-8

Planeje

Use

Teste

Sinalize

Aterre

CPFL ENERGIA

Gerência de Serviços de Rede: SERRA

Município: Caxias do Sul

Cliente: VANIA DARTORA SGORLA

Obra: Regularização GMT

Endereço: LIN SARTORINA 1400 95000-001 CAXIAS DO SUL BR RS

Responsável Técnico:
Eng. Ederson Paulo Vogel
CREA: RS135794

Escala: 1:850
Classe de Isolção: 18kV
Projeto: 000008036745

Data: 11/05/2026
AL: CXH34
Projeto: 000008036745

Nota: 00000754818
Folha 1
Levantador: Adelar Miguel