


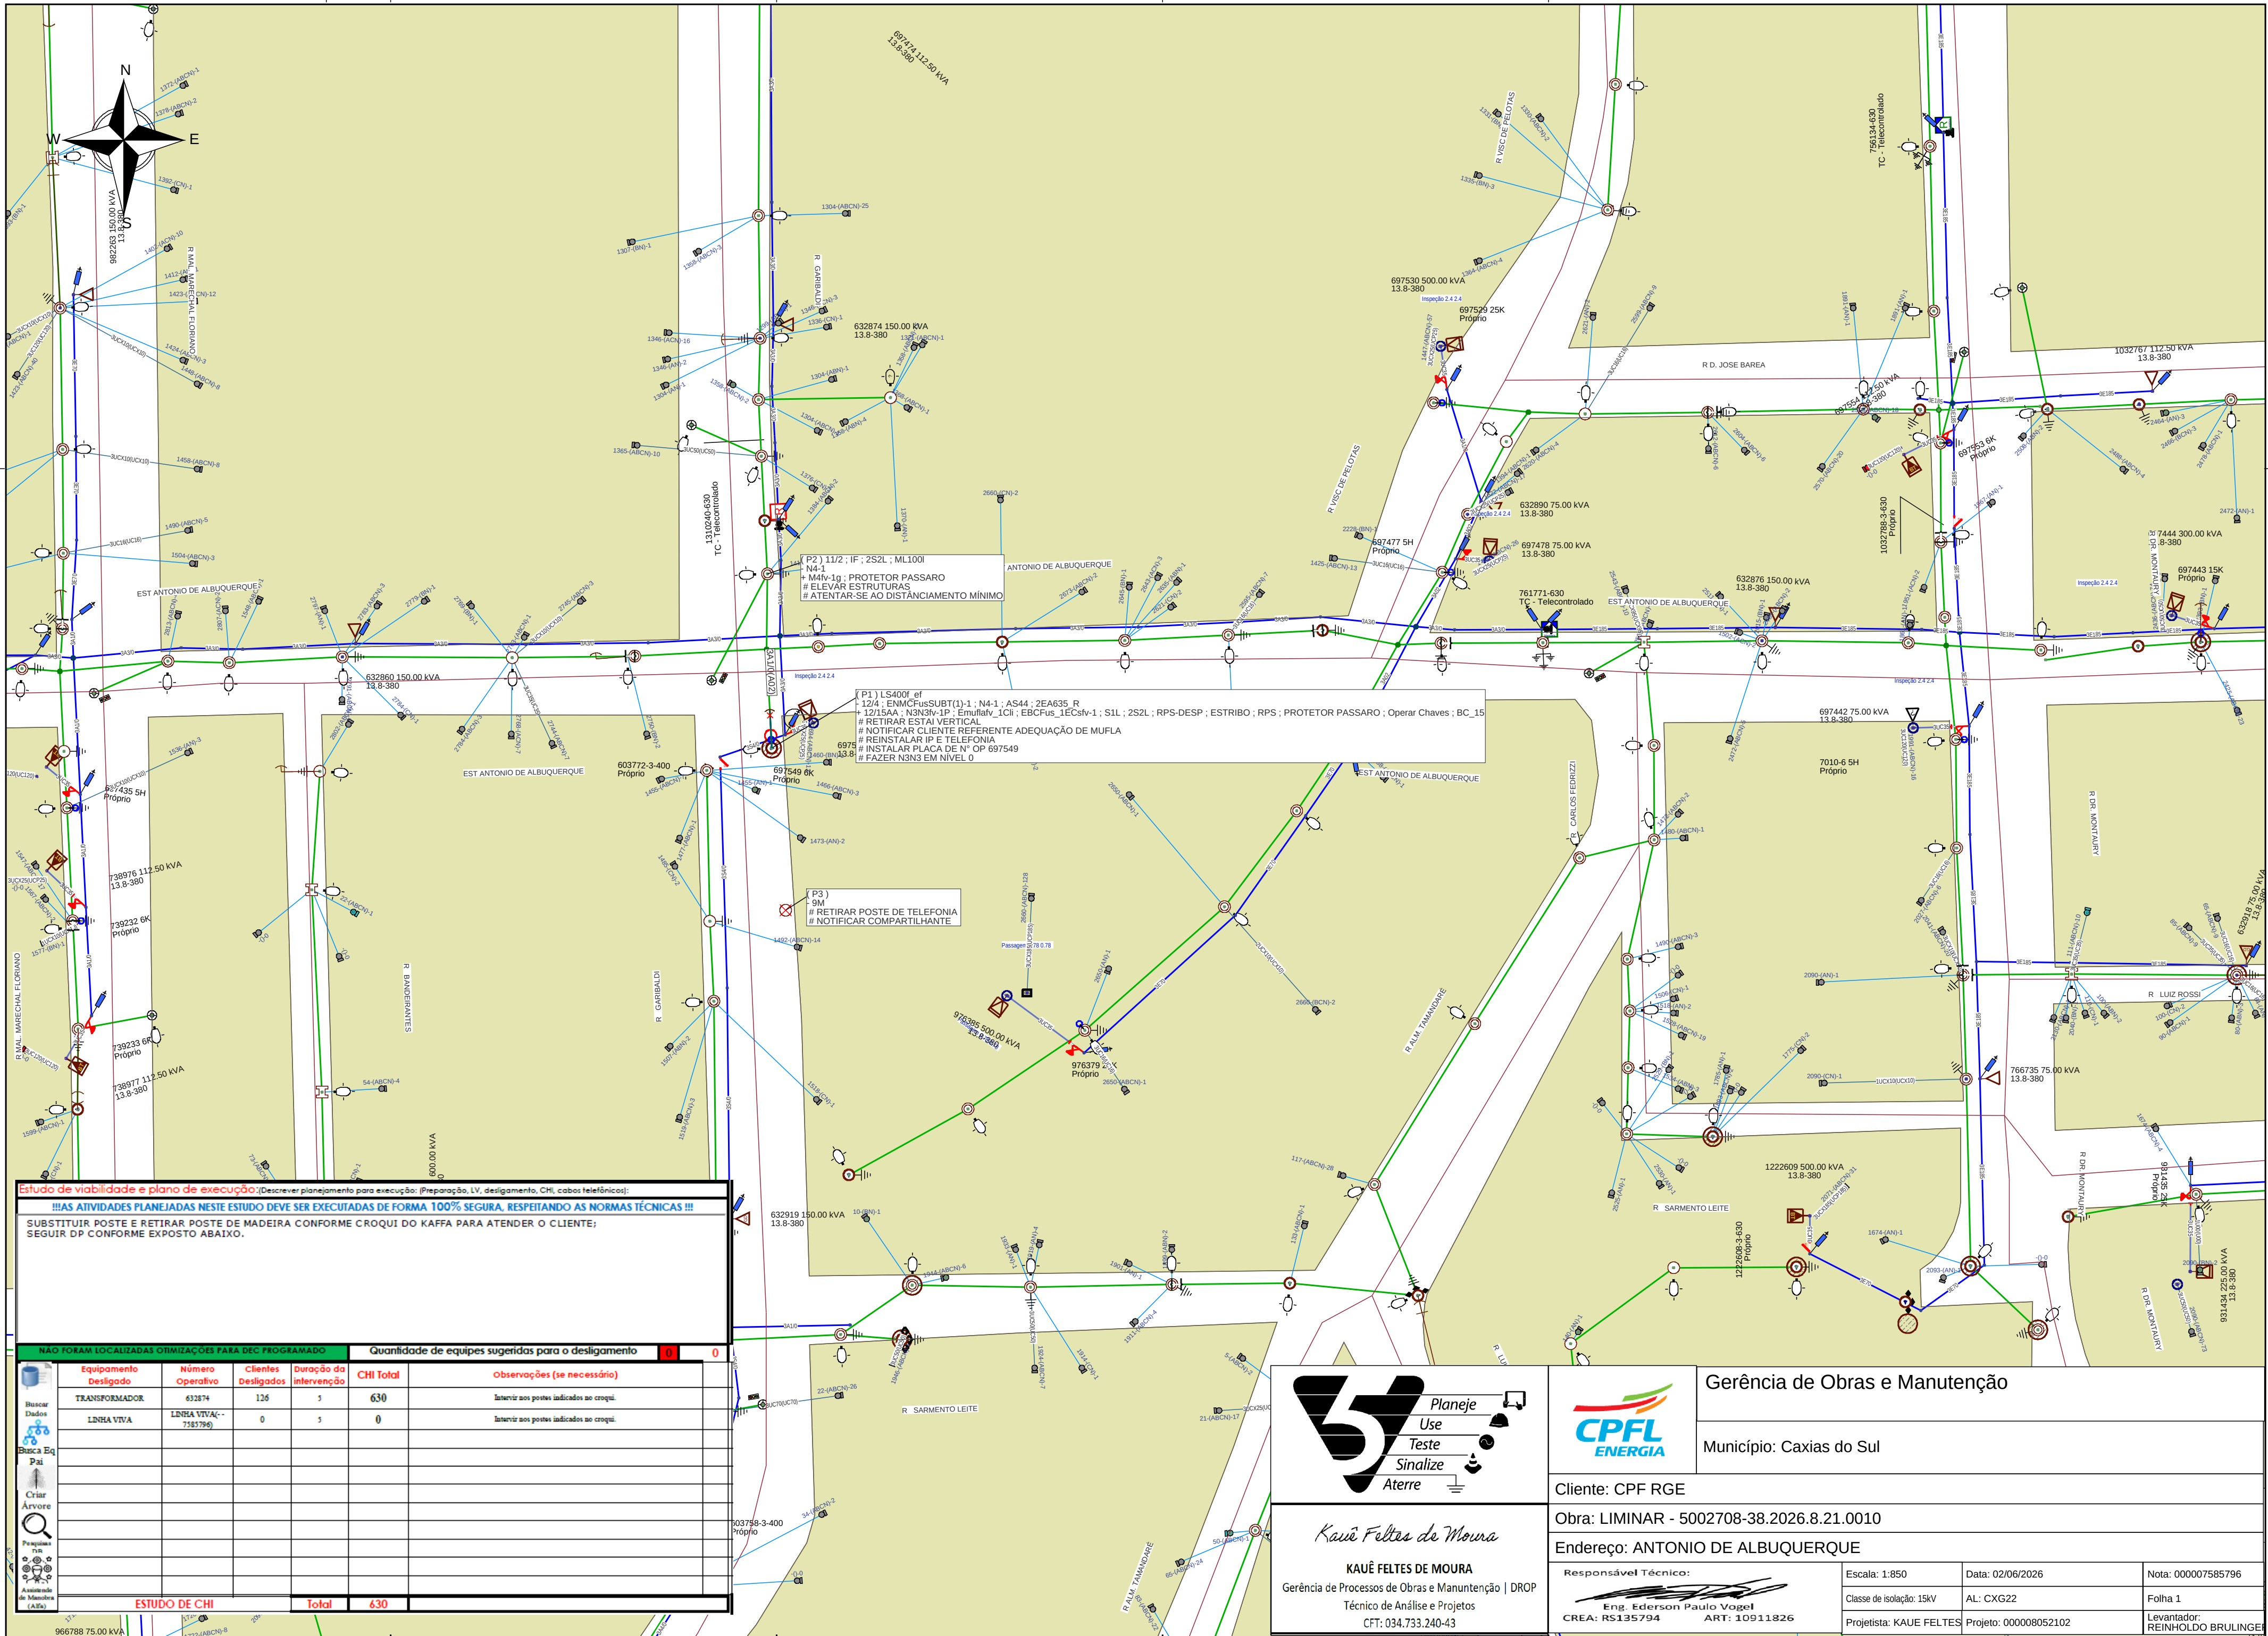

Estudo de viabilidade e plano de execução: (Descrever planejamento para execução: (Preparação, LV, desligamento, CHI, cabos telefônicos):

!!!AS ATIVIDADES PLANEJADAS NESTE ESTUDO DEVE SER EXECUTADAS DE FORMA 100% SEGURA, RESPEITANDO AS NORMAS TÉCNICAS !!!

SUBSTITUIR POSTE E RETIRAR POSTE DE MADEIRA CONFORME CROQUI DO KAFFA PARA ATENDER O CLIENTE;
SEGUIR DP CONFORME EXPOSTO ABAIXO.

NÃO FORAM LOCALIZADAS OTIMIZAÇÕES PARA DEC PROGRAMADO					Quantidade de equipes sugeridas para o desligamento	
					0	0
 Buscar Dados  Buscar Eq Pat  Criar Árvore  Pesquisas  Análise de Manobra (AEM)	Equipamento Desligado	Número Operativo	Clientes Desligados	Duração da intervenção	CHI Total	Observações (se necessário)
	TRANSFORMADOR	632874	126	5	630	Intervir nos postes indicados no croqui.
	LINHA VIVA	LINHA VIVA (-7585796)	0	5	0	Intervir nos postes indicados no croqui.
ESTUDO DE CHI					Total	630

Planeje

Use

Teste

Sinalize

Aterre

Kauê Feltes de Moura

Gerência de Processos de Obras e Manutenção | DROP

Técnico de Análise e Projetos

CFT: 034.733.240-43

Gerência de Obras e Manutenção

Município: Caxias do Sul

Cliente: CPF RGE

Obra: LIMINAR - 5002708-38.2026.8.21.0010

Endereço: ANTONIO DE ALBUQUERQUE

Responsável Técnico:

Eng. Ederson Paulo Vogel

CREA: RS135794 ART: 10911826

Escala: 1:850

Classe de isolamento: 15KV

Data: 02/06/2026

AL: CXG22

Projeto: 000008052102

Nota: 000007585796

Folha 1

Levantador: REINHOLDO BRULINGER