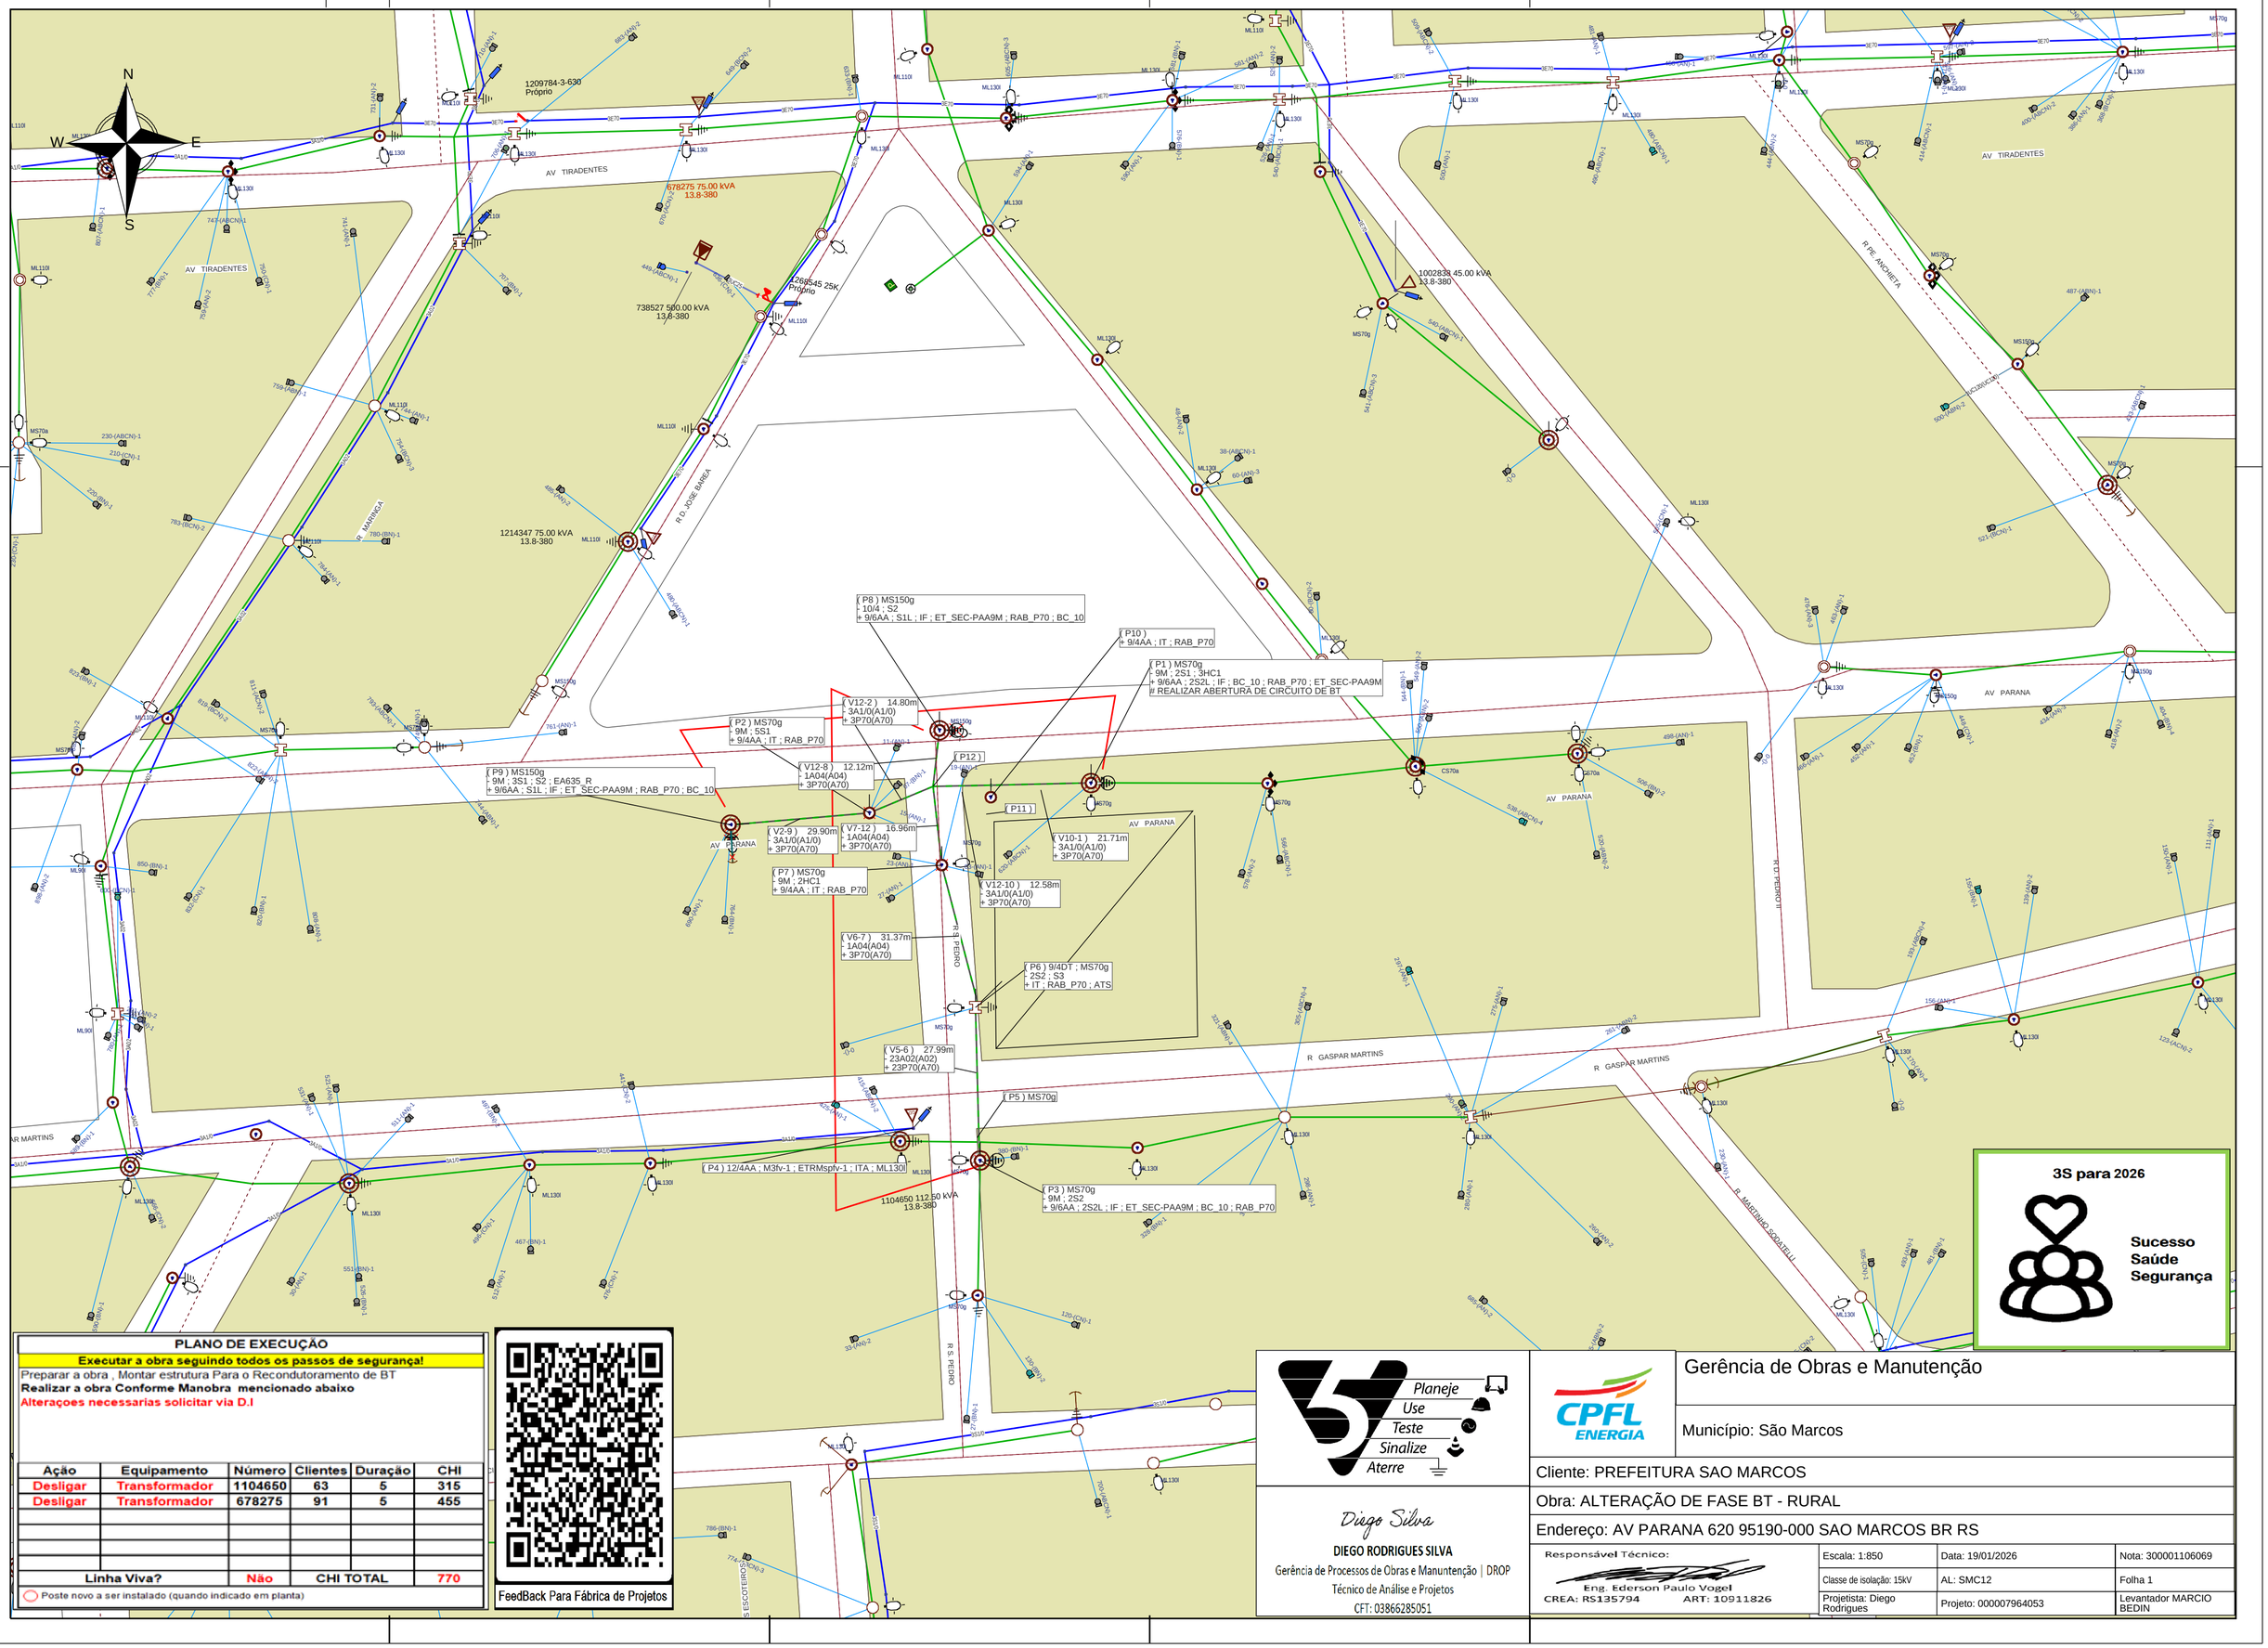


PLANO DE EXECUÇÃO

Executar a obra seguindo todos os passos de segurança!

Preparar a obra , Montar estrutura Para o Recondutoramento de BT

Realizar a obra Conforme Manobra mencionado abaixo

Alteraçoes necessarias solicitar via D.I

Ação	Equipamento	Número	Clientes	Duração	CHI
Desligar	Transformador	1104650	63	5	315
Desligar	Transformador	678275	91	5	455
Linha Viva?		Não	CHI TOTAL		770

◯ Poste novo a ser instalado (quando indicado em planta)

FeedBack Para Fábrica de Projetos

3S para 2026

Sucesso
Saúde
Segurança

Planeje
Use
Teste
Sinalize
Aterre

Diogo Silva

DIEGO RODRIGUES SILVA
Gerência de Processos de Obras e Manuntenção | DROP
Técnico de Análise e Projetos
CFT: 03866285051

CPFL ENERGIA

Gerência de Obras e Manutenção

Município: São Marcos

Cliente: PREFEITURA SAO MARCOS

Obra: ALTERAÇÃO DE FASE BT - RURAL

Endereço: AV PARANA 620 95190-000 SAO MARCOS BR RS

Responsável Técnico:
Eng. Ederson Paulo Vogel
CREA: RS135794 ART: 10911826

Escala: 1:850	Data: 19/01/2026	Nota: 300001106069
Classe de isolação: 15kV	AL: SMC12	Folha 1
Projetista: Diego Rodrigues	Projeto: 000007964053	Levantador MARCIO BEDIN