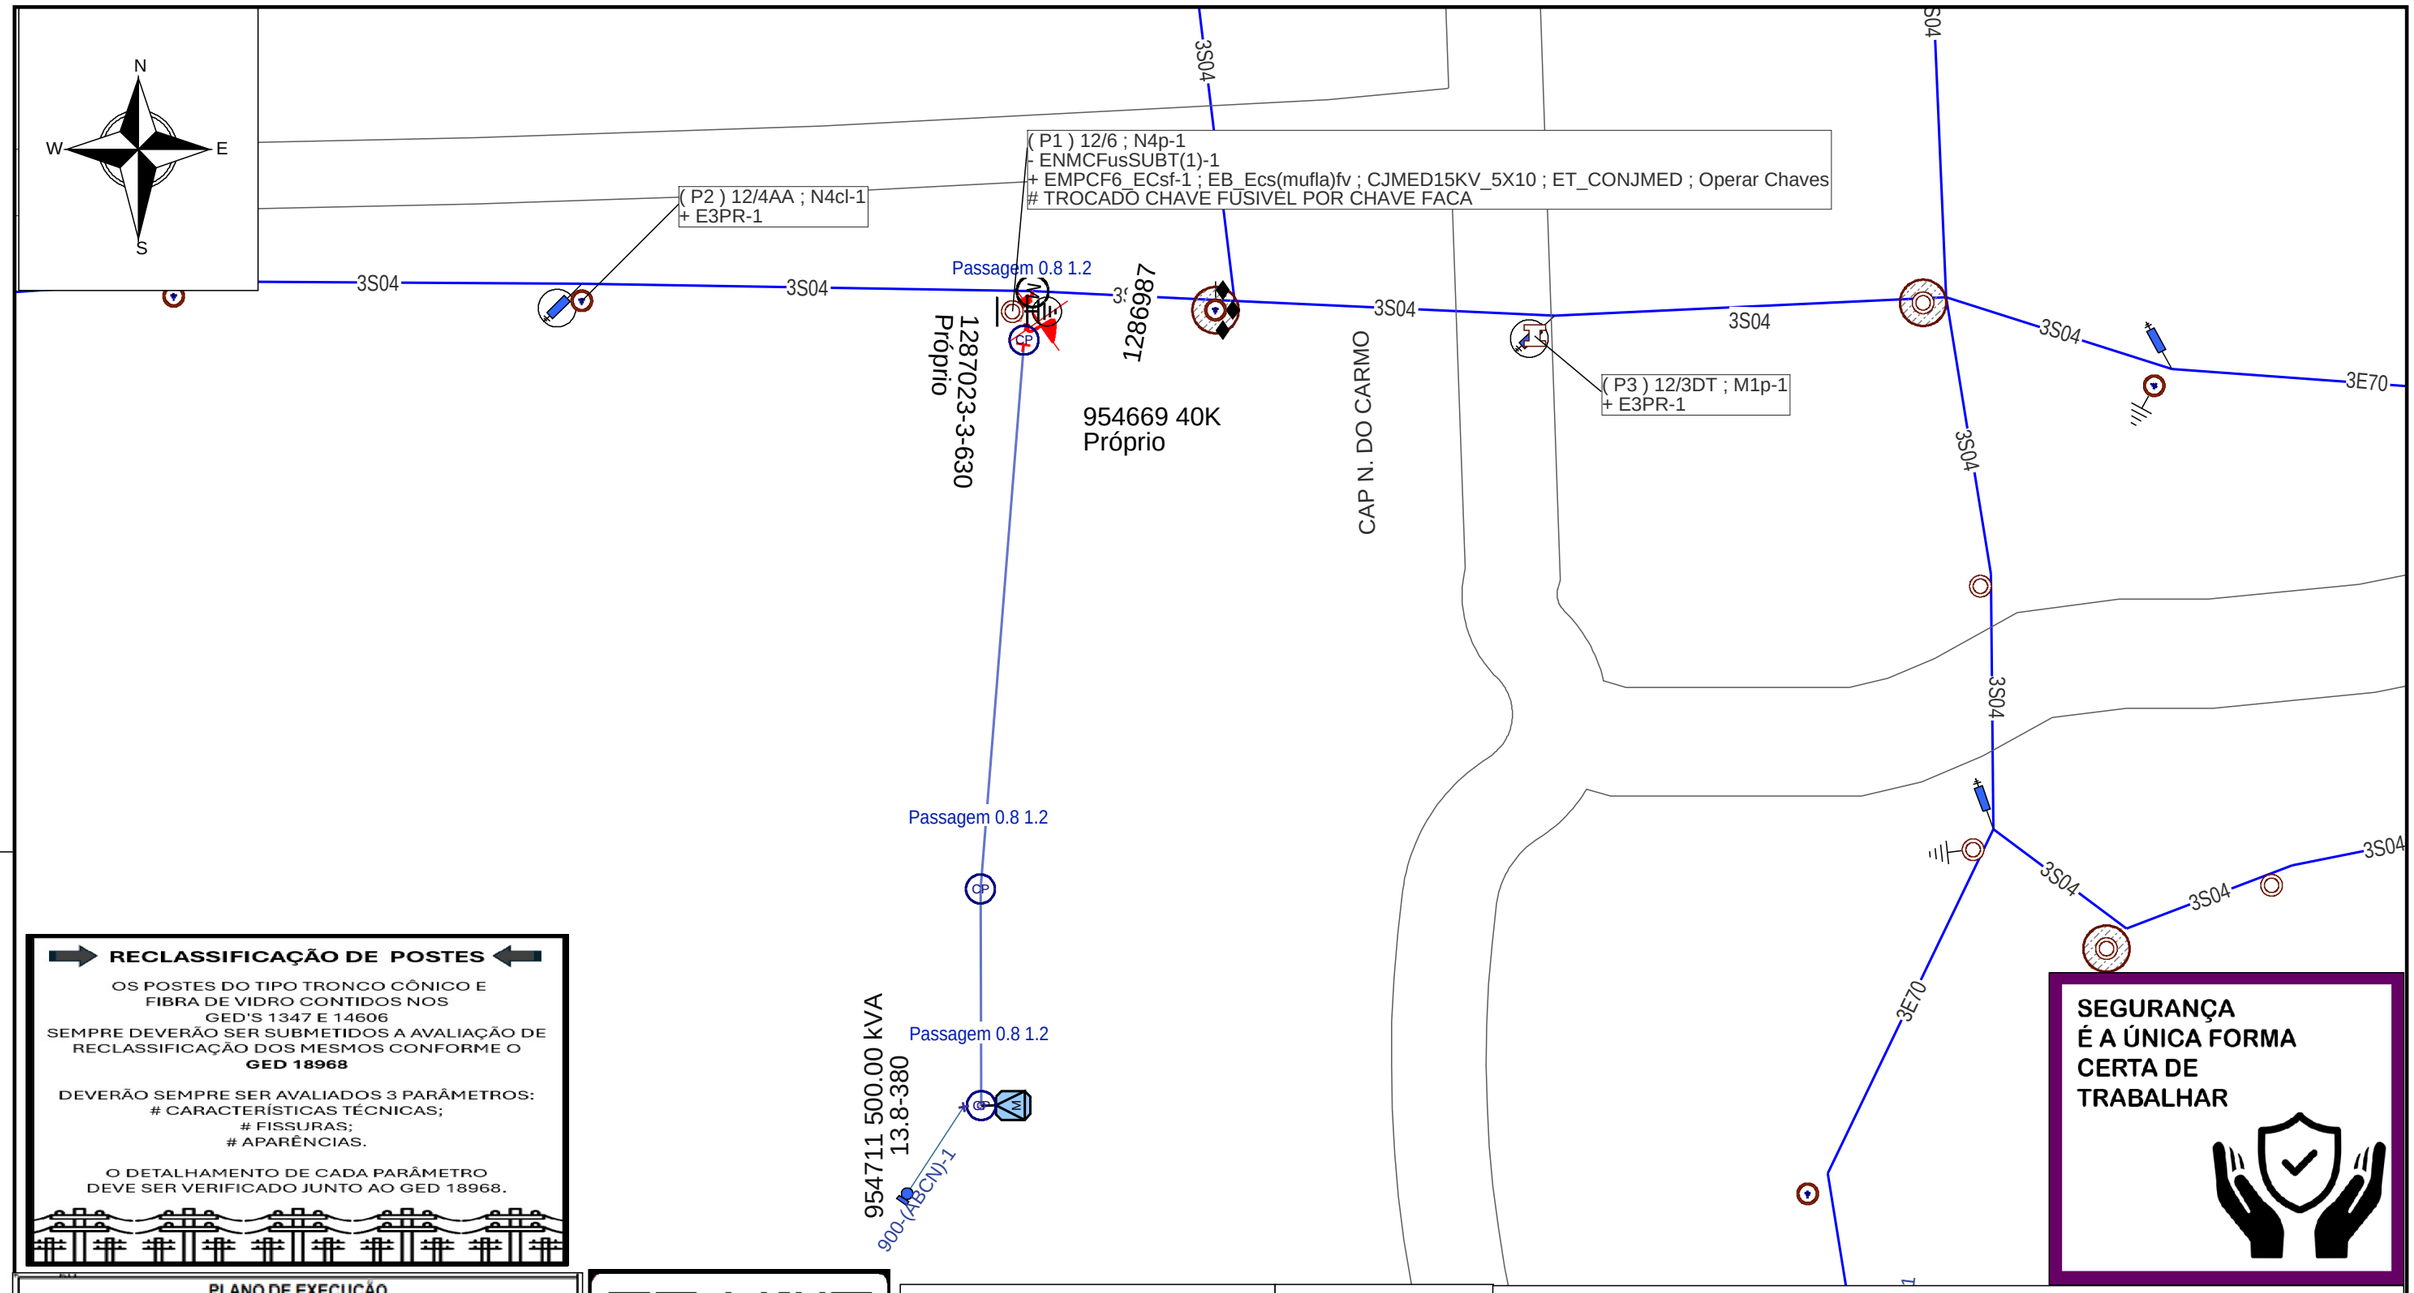


RECLASSIFICAÇÃO DE POSTES

OS POSTES DO TIPO TRONCO CÔNICO E FIBRA DE VIDRO CONTIDOS NOS GED'S 1347 E 14606 SEMPRE DEVERÃO SER SUBMETIDOS A AVALIAÇÃO DE RECLASSIFICAÇÃO DOS MESMOS CONFORME O **GED 18968**

DEVERÃO SEMPRE SER AVALIADOS 3 PARÂMETROS:
CARACTERÍSTICAS TÉCNICAS;
FISSURAS;
APARÊNCIAS.

O DETALHAMENTO DE CADA PARÂMETRO DEVE SER VERIFICADO JUNTO AO GED 18968.

PLANO DE EXECUÇÃO

ABRIR CAVAS, PREPARAR OS PONTOS DA OBRA.
REALIZAR ATIVIDADES COM LINHA VIVA .

REALIZAR TODAS AS ATIVIDADES SEGUINDO AS NORMAS DE SEGURANÇA.
ESSE PROJETO SÓ PODE SER ALTERADO POR SOLICITAÇÃO DE DI.

Ação	Equipamento	Número	Clientes	Duração	CHI
Abrir	Chave Fusivel	954669	1	4	4
Linha Viva?		Sim	CHI TOTAL		4

◯ Poste novo a ser instalado (quando indicado em planta)

FeedBack Para Fábrica de Projetos

Planeje
Use
Teste
Sinalize
Aterre

Gabriel Vergani
Gerência de Processos de Obras e Manutenção | DROP
Técnico de Análise e Projetos
CFT: 040.224.970-41

CPFL ENERGIA

Gerência de Obras e Manutenção

Município: Flores da Cunha

Cliente: RGE SUL DISTRIBUIDORA DE ENERGIA S/A

Obra: AP_PME_RER 2023-568-AL-FCU25

Endereço: TVS RONDELLI 900 93000-000 FLORES DA CUNHA BR

Responsável Técnico:
Eng. Ederson Paulo Vogel
CREA: RS135794 ART: 10911826

Escala: 1:850	Data: 30/12/2022	Nota: 000005083678
Classe de isolação: 15kV	AL: FCU25	Folha 1
Projetista: Gabriel Vergani	Projeto: 000006930832	Levantador: Cledir Moretti