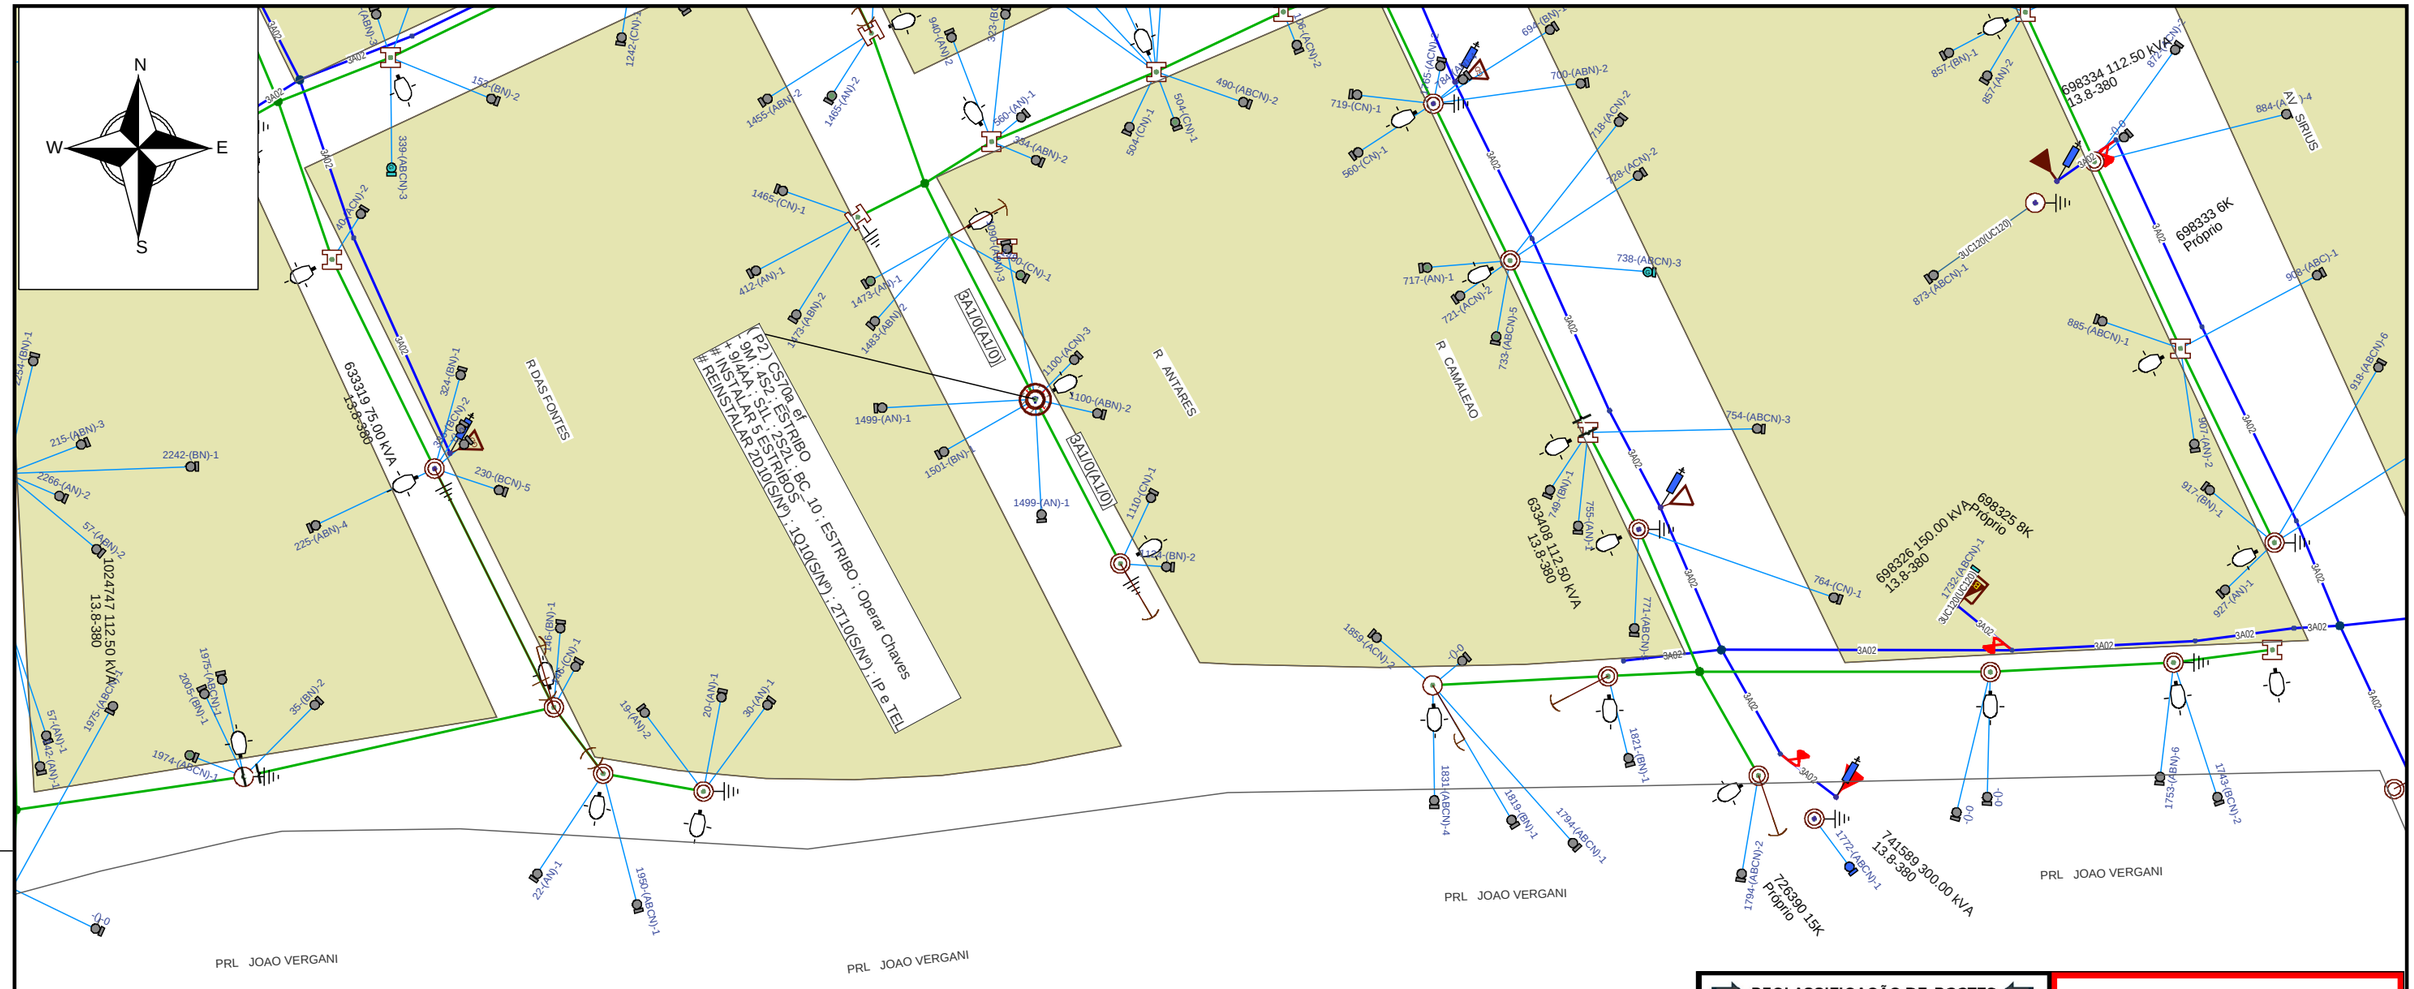


RECLASSIFICAÇÃO DE POSTES

OS POSTES DO TIPO TRONCO CÔNICO E FIBRA DE VIDRO CONTIDOS NOS GED'S 1347 E 14606 SEMPRE DEVERÃO SER SUBMETIDOS A AVALIAÇÃO DE RECLASSIFICAÇÃO DOS MESMOS CONFORME O **GED 18968**

DEVERÃO SEMPRE SER AVALIADOS 3 PARÂMETROS:
CARACTERÍSTICAS TÉCNICAS;
FISSURAS;
APARÊNCIAS.

O DETALHAMENTO DE CADA PARÂMETRO DEVE SER VERIFICADO JUNTO AO GED 18968.

DESCUIDO É RISCO,

SEGURANÇA É VIDA.

PLANO DE EXECUÇÃO

EXECUTAR A OBRA SEGUINDO TODOS OS PROTOCOLOS DE SEGURANÇA E CONFORME PROJETO INCLUINDO A TROCA DE POSTES EXISTENTES MOVIMENTAÇÃO DO VAO PRIMARIO E INSTALAÇAO DE NOVOS POSTES

Ação	Equipamento	Número	Clientes	Duração	CHI
Abrir	Chave Fusível	596703	2	5	10
Linha Viva?		Não	CHI TOTAL		10

◯ Poste novo a ser instalado (quando indicado em planta)

FeedBack Para Fábrica de Projetos

Planeje
Use
Teste
Sinalize
Aterre

Breno Ardenghy

Breno Ardenghy Da Silva
Gerência de Processos de Obras e Manuntenção | DROP
Técnico de Análise e Projetos
CFT: 03188101074

CPFL ENERGIA

Gerência de Obras e Manutenção

Município: Caxias do Sul

Cliente: RGE SUL DISTRIBUIDORA DE ENERGIA S.A

Obra: Substituição de Poste - 633332

Endereço: R ANTARES 1499 CRUZEIRO CAXIAS DO SUL

Responsável Técnico:
Eng. Ederson Paulo Vogel
CREA: RS135794 ART: 10911826

Escala: 1:800	Data: 21/02/2025	Nota: 000006686230
Classe de isolação: 15kV	AL: CXG12	Folha 1
Projetista: BRENO ARDENGHY	Projeto: 000007729623	Levantador: RICARDO Q. DE ALBUQUERQUE