


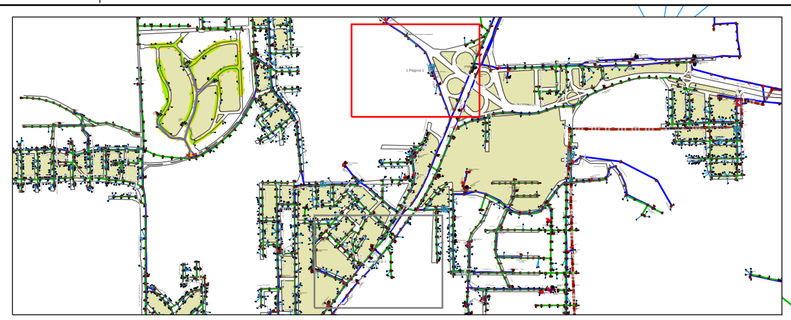

693585 8K
Próprio

693586 150.00 kVA
13.8-380

ROD RST 453

1309220-3-630
Próprio NUMERO ANTIGO 603917 FOI REMOVIDO

P6

P5

(P6)
- 11M ; N1-1
+ 12/4lfv ; M1fv-1g ; PROTETOR PASSARO

(P5)
- 11M ; N4-1
+ 12/4lfv ; N4fv-1g ; PROTETOR PASSARO ; BC_08

634042 75.00 kVA
13.8-380

ROD RST 453

763976-630
TC - Telecontrolado

ROD BR 116

754968-3-400
Próprio

ROD BR 116

634057 75.00 kVA

Geração Distribuída
62.31 kW

739246 112.50 kVA
13.8-380

(P4)
- 11M ; T1-1
+ 12/4AA ; M1fv-1g ; PROTETOR PASSARO

P4

736290 6K
Próprio

601184 75.00 kVA
13.8-380

BR 116

PLANO + US

Estudo de viabilidade e plano de execução: (Descrever planejamento para execução: (Preparação, LV, desligamento, CHI, cabos telefônicos):

!!!AS ATIVIDADES PLANEJADAS NESTE ESTUDO DEVE SER EXECUTADAS DE FORMA 100% SEGURA, RESPEITANDO AS NORMAS TÉCNICAS !!!

SUBSTITUIR POSTES CONFORME CROQUI DO KAFFA;
SEGUIR DP CONFORME EXPOSTO ABAIXO;

NÃO FORAM LOCALIZADAS OTIMIZAÇÕES PARA DEC PROGRAMADO

Quantidade de equipes sugeridas para o desligamento 0 0

Buscar Dados

Equipamento Desligado	Número Operativo	Clientes Desligados	Duração da intervenção	CHI Total	Observações (se necessário)	
MANOBRA	MANOBRA (- 6824322)	37	5	185	Manobra entre FC 603918, FC 732516 e RL 758143.	

5T Planeje Use Teste Sinalize Aterre

CPFL ENERGIA

Gerência de Obras e Manutenção

Município: Caxias do Sul


Cliente: RGE SUL DISTRIBUIDORA DE ENERGIA

Obra: Caxias do Sul 2025 - Insp Visual de Rede

Endereço: EST RST 453 ROTA DO SOL 25888

Responsável Técnico:
Eng. Ederson Paulo Vogel
CREA: RS135794 ART: 10911826

Escala: 1:1000	Data: 28/04/2025	Nota: 000006824322
Classe de isolação: 15kV	AL: CXD25	Folha 1
Projetista: GUILHERME DIAS	Projeto: 000007778798	RICARDO QUEVEDO

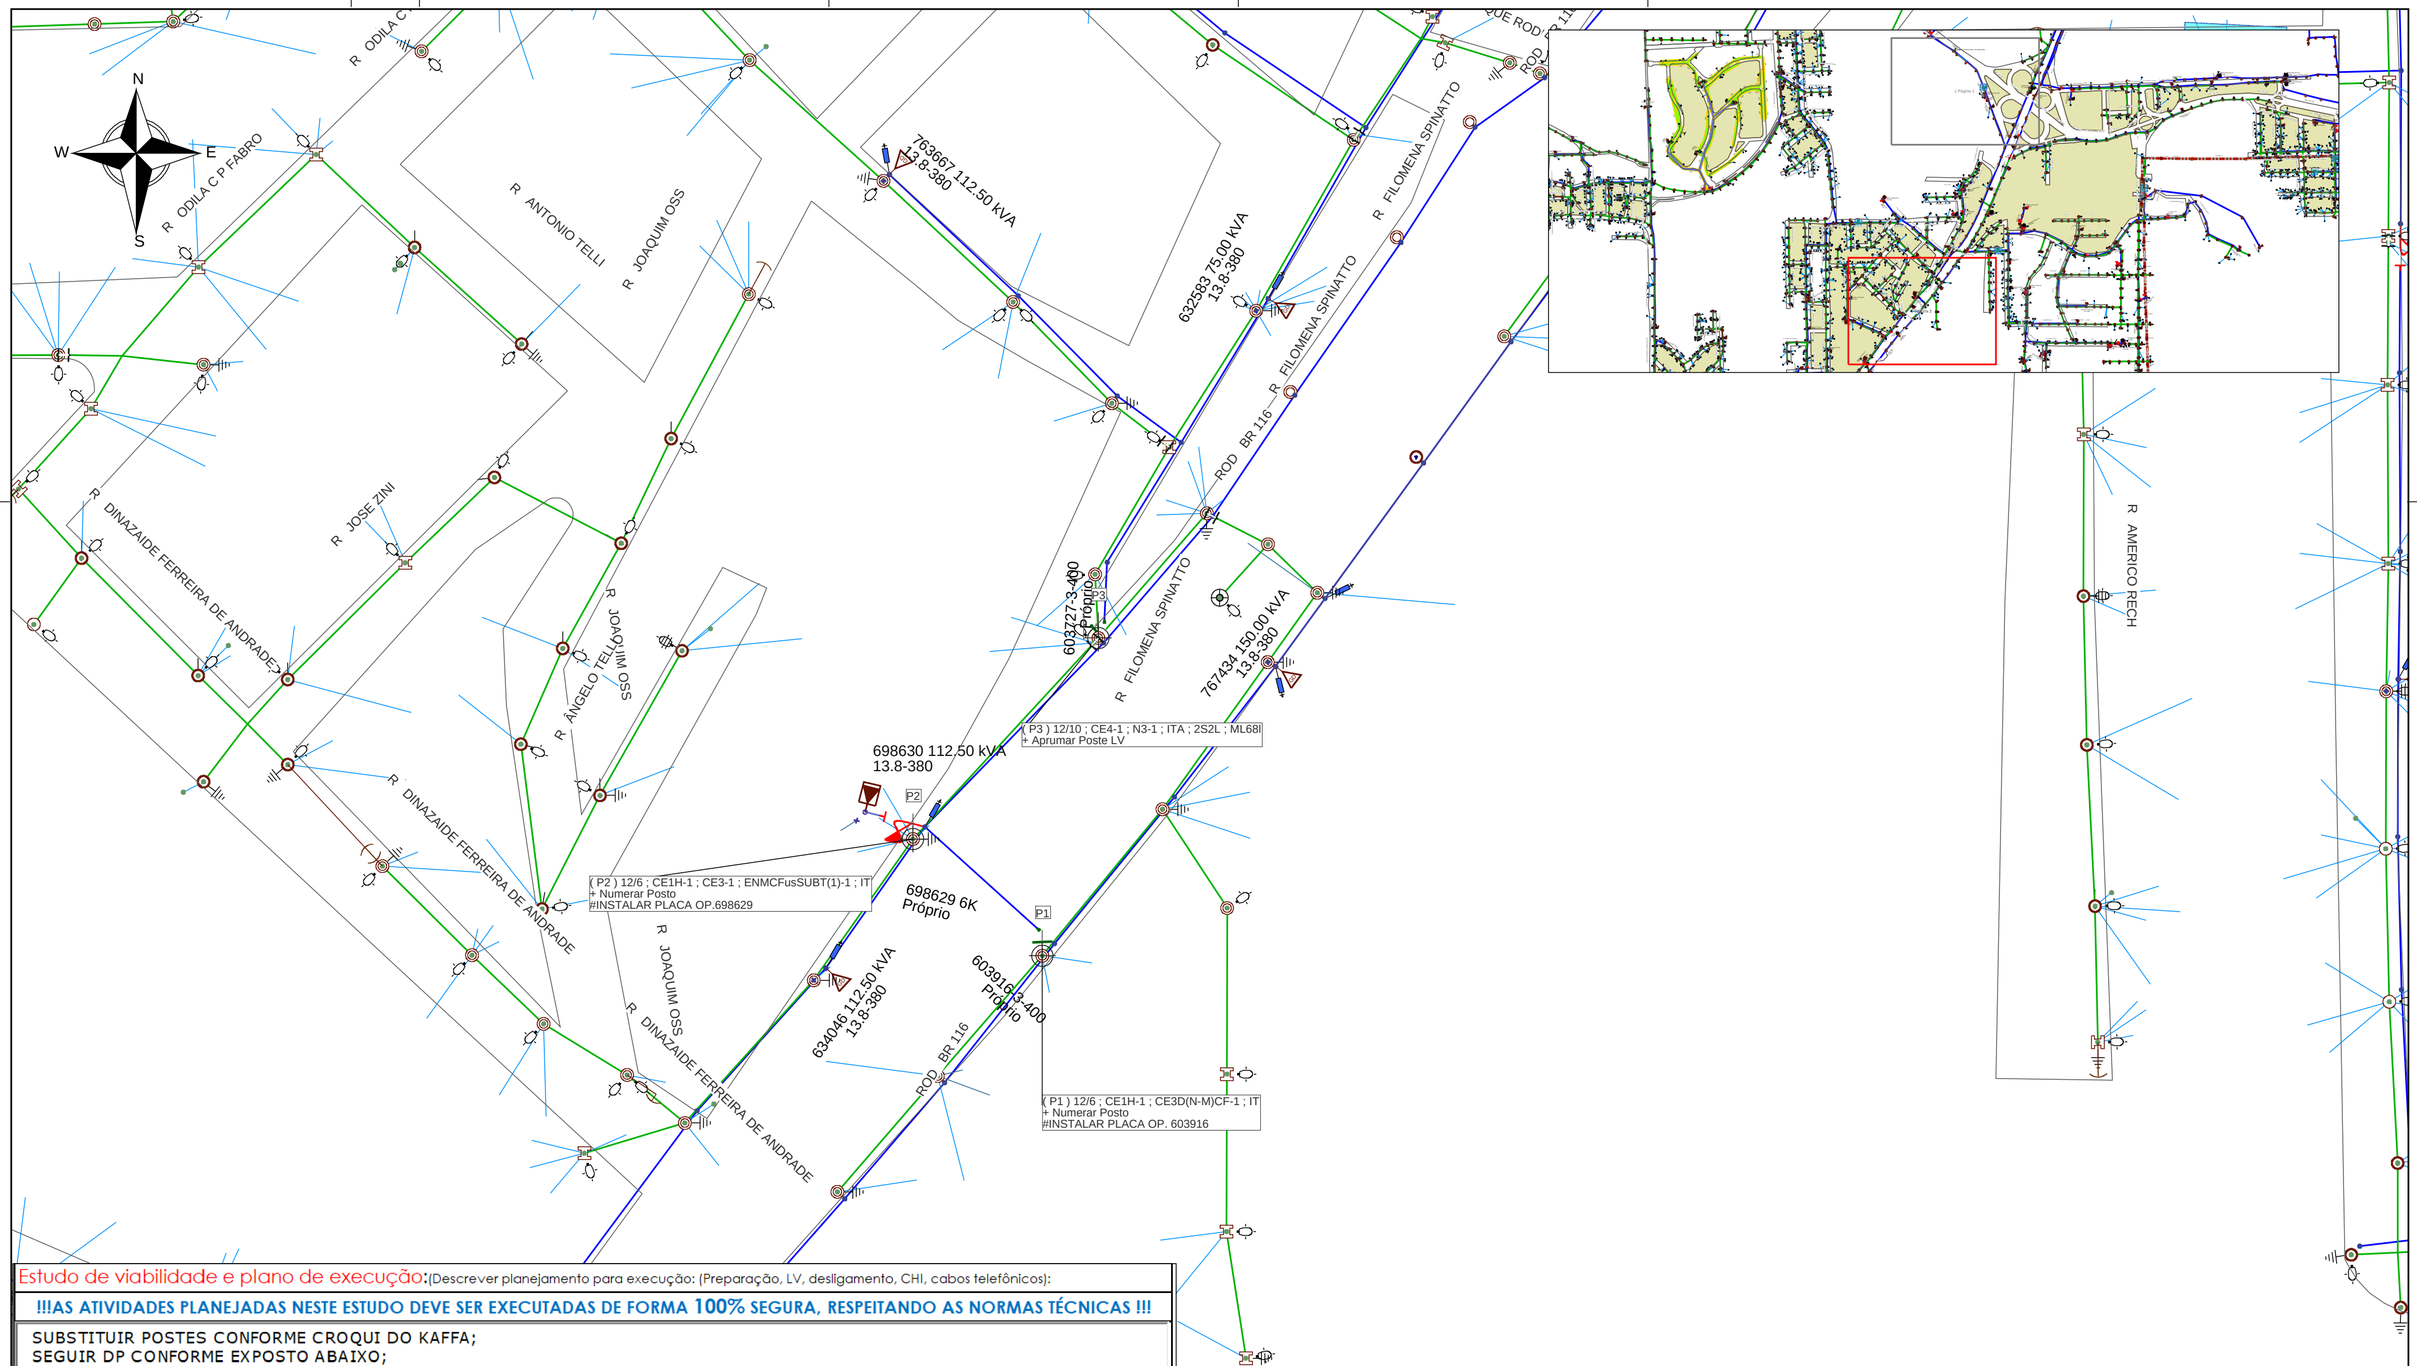

Estudo de viabilidade e plano de execução:(Descrever planejamento para execução: (Preparação, LV, desligamento, CHI, cabos telefônicos):

!!!AS ATIVIDADES PLANEJADAS NESTE ESTUDO DEVE SER EXECUTADAS DE FORMA 100% SEGURA, RESPEITANDO AS NORMAS TÉCNICAS !!!

SUBSTITUIR POSTES CONFORME CROQUI DO KAFFA;
SEGUIR DP CONFORME EXPOSTO ABAIXO;

NÃO FORAM LOCALIZADAS OTIMIZAÇÕES PARA DEC PROGRAMADO | Quantidade de equipes sugeridas para o desligamento | 0 | 0

Buscar Dados

Equipamento Desligado	Número Operativo	Clientes Desligados	Duração da intervenção	CHI Total	Observações (se necessário)
MANOBRA	MANOBRA (- 6824322)	37	5	185	Manobra entre FC 603918, FC 732516 e RL 758143.

Planeje Use Teste Sinalize Aterre

PLANO + US

CPFL ENERGIA

Gerência de Obras e Manutenção

Município: Caxias do Sul

Cliente: RGE SUL DISTRIBUIDORA DE ENERGIA

Obra: Caxias do Sul 2025 - Insp Visual de Rede

Endereço: EST RST 453 ROTA DO SOL 25888

Responsável Técnico:
Eng. Ederson Paulo Vogel
CREA: RS135794 ART: 10911826

Escala: 1:1000	Data: 28/04/2025	Nota: 000006824322
Classe de isolação: 15kV	AL: CXD25	Folha 2
Projetista: GUILHERME DIAS	Projeto: 000007778798	RICARDO QUEVEDO