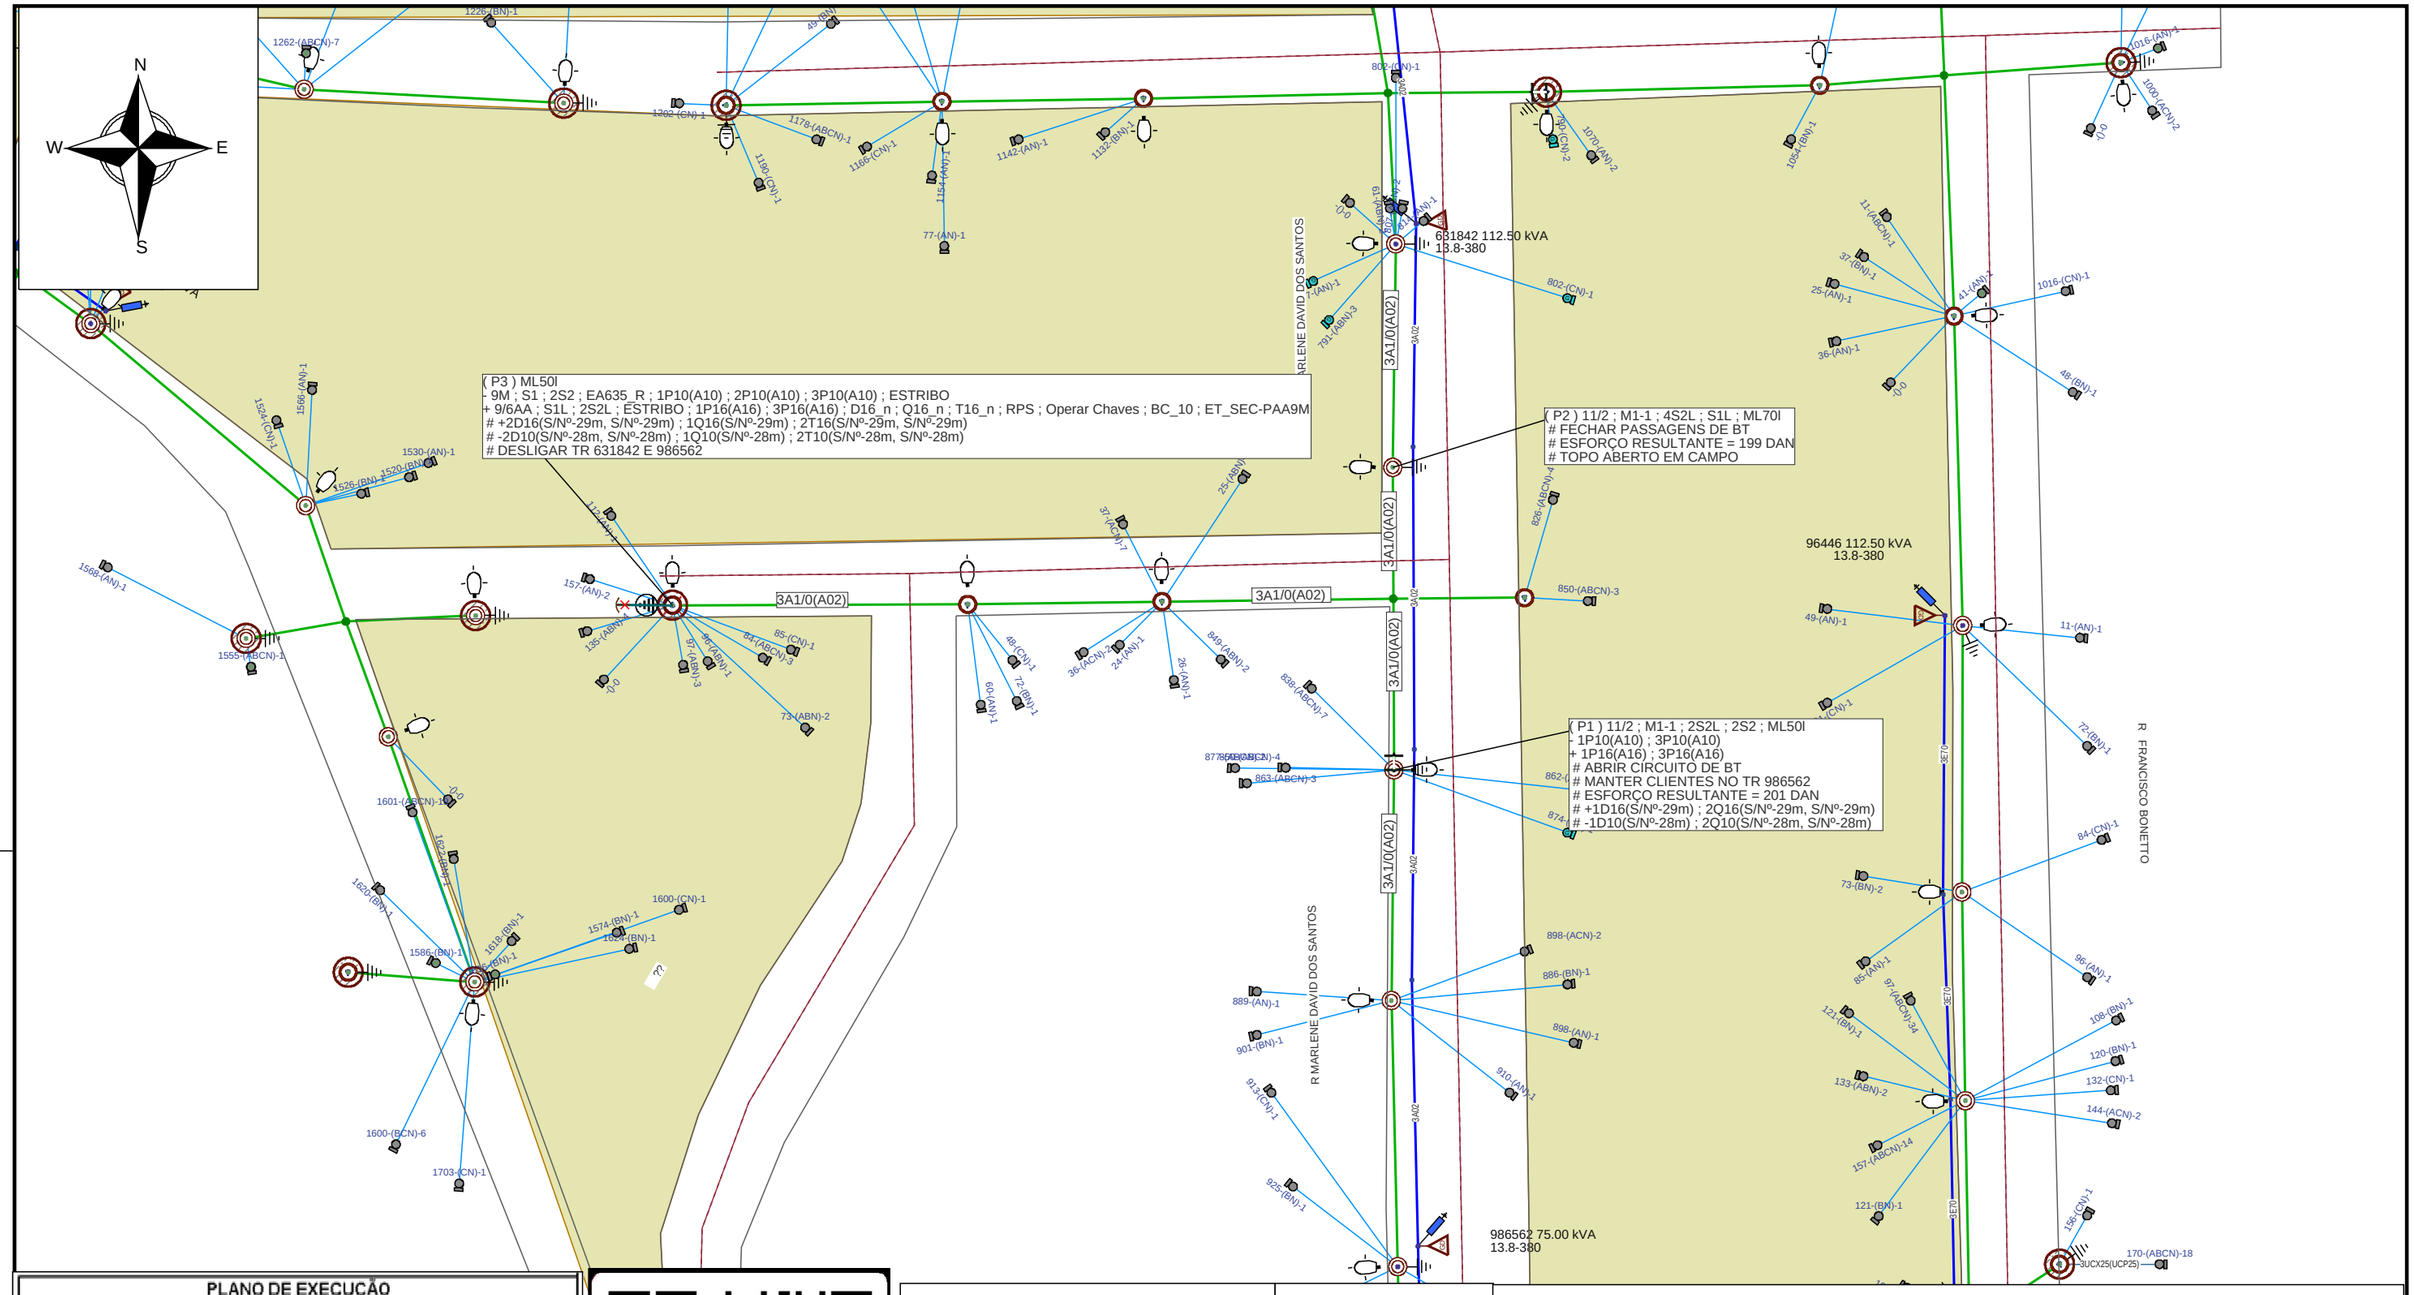


PLANO DE EXECUÇÃO

EXECUTAR ATIVIDADES RESPEITANDO AS NORMAS DE SEGURANÇA!

Manobrar equipamento abaixo para substituir os postes conforme projeto.
Executar as atividades conforme projeto, demais alterações solicitar via D.I.
Preparar cavas e postes para executar obra, após isso realizar o desligamento.
MO para manobra paga no P3. EXECUTAR OBRA EM LM.

Ação	Equipamento	Número	Clientes	Duração	CHI
Desligar	Transformador	631842	32	3	96
Desligar	Transformador	986562	92	3	276
Linha Viva?		Não	CHI TOTAL		372

◯ Poste novo a ser instalado (quando indicado em planta)

FeedBack Para Fábrica de Projetos

Planeje
Use
Teste
Sinalize
Aterre

Franco Conrado de Oliveira
Gerência de Processos de Obras e Manuntenção | DROP
Técnico de Análise e Projetos
CFT: 0472592505-5

CPFL ENERGIA

Gerência de Obras e Manutenção

Município: Caxias do Sul

Cliente: RGE SUL DISTRIBUIDORA DE ENERGIA S.A.

Obra: Plano Sobrecarga 2026

Endereço: AV SANDRO TONIETTO, 863, URBANO, CAXIAS DO SUL - RS

Responsável Técnico:
Eng. Ederson Paulo Vogel
CREA: RS135794 ART: 10911826

Escala: 1:850	Data: 02/02/2026	Nota: 000006955033
Classe de isolação: 15kV	AL: CXH45	Folha 1
Projetista: Franco Conrado	Projeto: 000007973251	Levantador: Ricardo Albuquerque