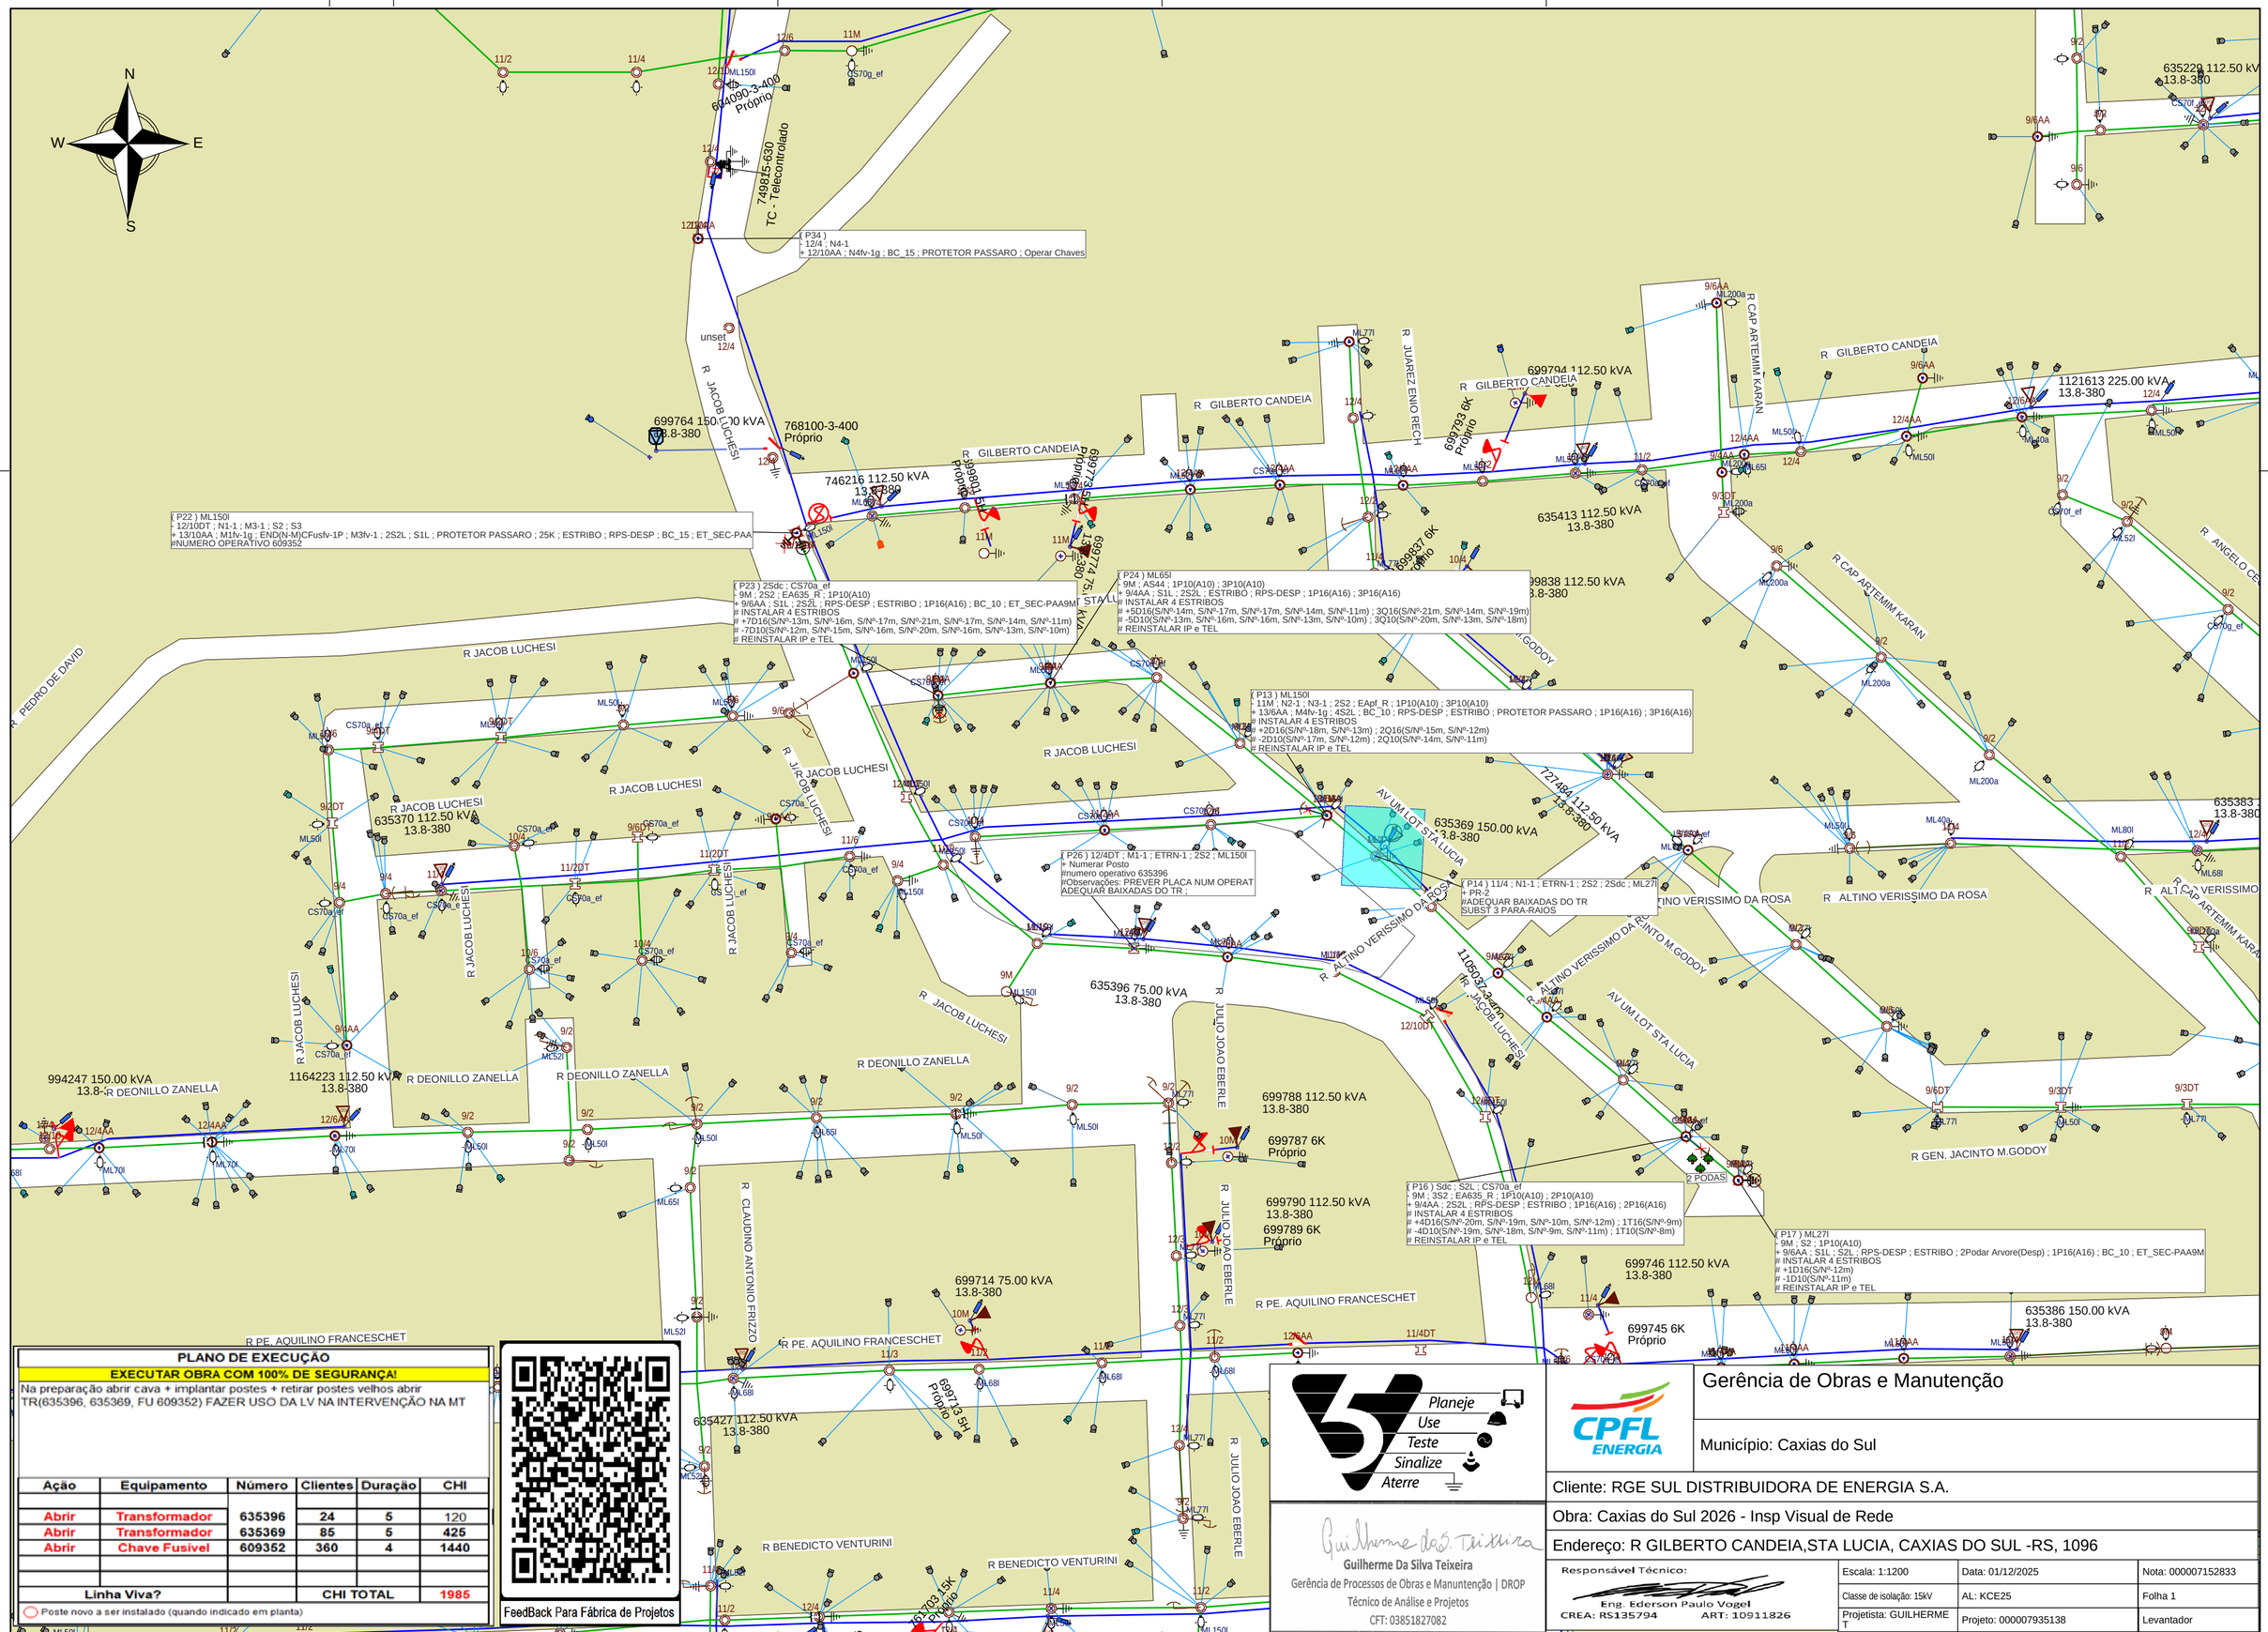


PLANO DE EXECUÇÃO					
EXECUTAR OBRA COM 100% DE SEGURANÇA!					
Na preparação abrir cava + implantar postes + retirar postes velhos abrir TR(635396, 635369, FU 609352) FAZER USO DA LV NA INTERVENÇÃO NA MT					
Ação	**Equipamento**	**Número**	**Clientes**	**Duração**	**CHI**
Abrir	Transformador	635396	24	5	120
Abrir	Transformador	635369	85	5	425
Abrir	Chave Fusivel	609352	360	4	1440
Linha Viva?			CHI TOTAL		1985

Poste novo a ser instalado (quando indicado em planta)

FeedBack Para Fábrica de Projetos

Planeje
Use
Teste
Sinalize
Aterre

Guilherme Da Silva Teixeira
Gerência de Processos de Obras e Manuntenção | DROP
Técnico de Análise e Projetos
CFT: 038518270 82

CPFL ENERGIA

Gerência de Obras e Manutenção

Município: Caxias do Sul

Cliente: RGE SUL DISTRIBUIDORA DE ENERGIA S.A.

Obra: Caxias do Sul 2026 - Insp Visual de Rede

Endereço: R GILBERTO CANDEIA,STA LUCIA, CAXIAS DO SUL -RS, 1096

Responsável Técnico:	Escala: 1:1200	Data: 01/12/2025	Nota: 000007152833
Eng. Ederson Paulo Vogel CREA: RS135794 ART: 10911826	Classe de isolação: 15kV	AL: KCE25	Folha 1
Projetista: GUILHERME T	Projeto: 000007935138		Levantador