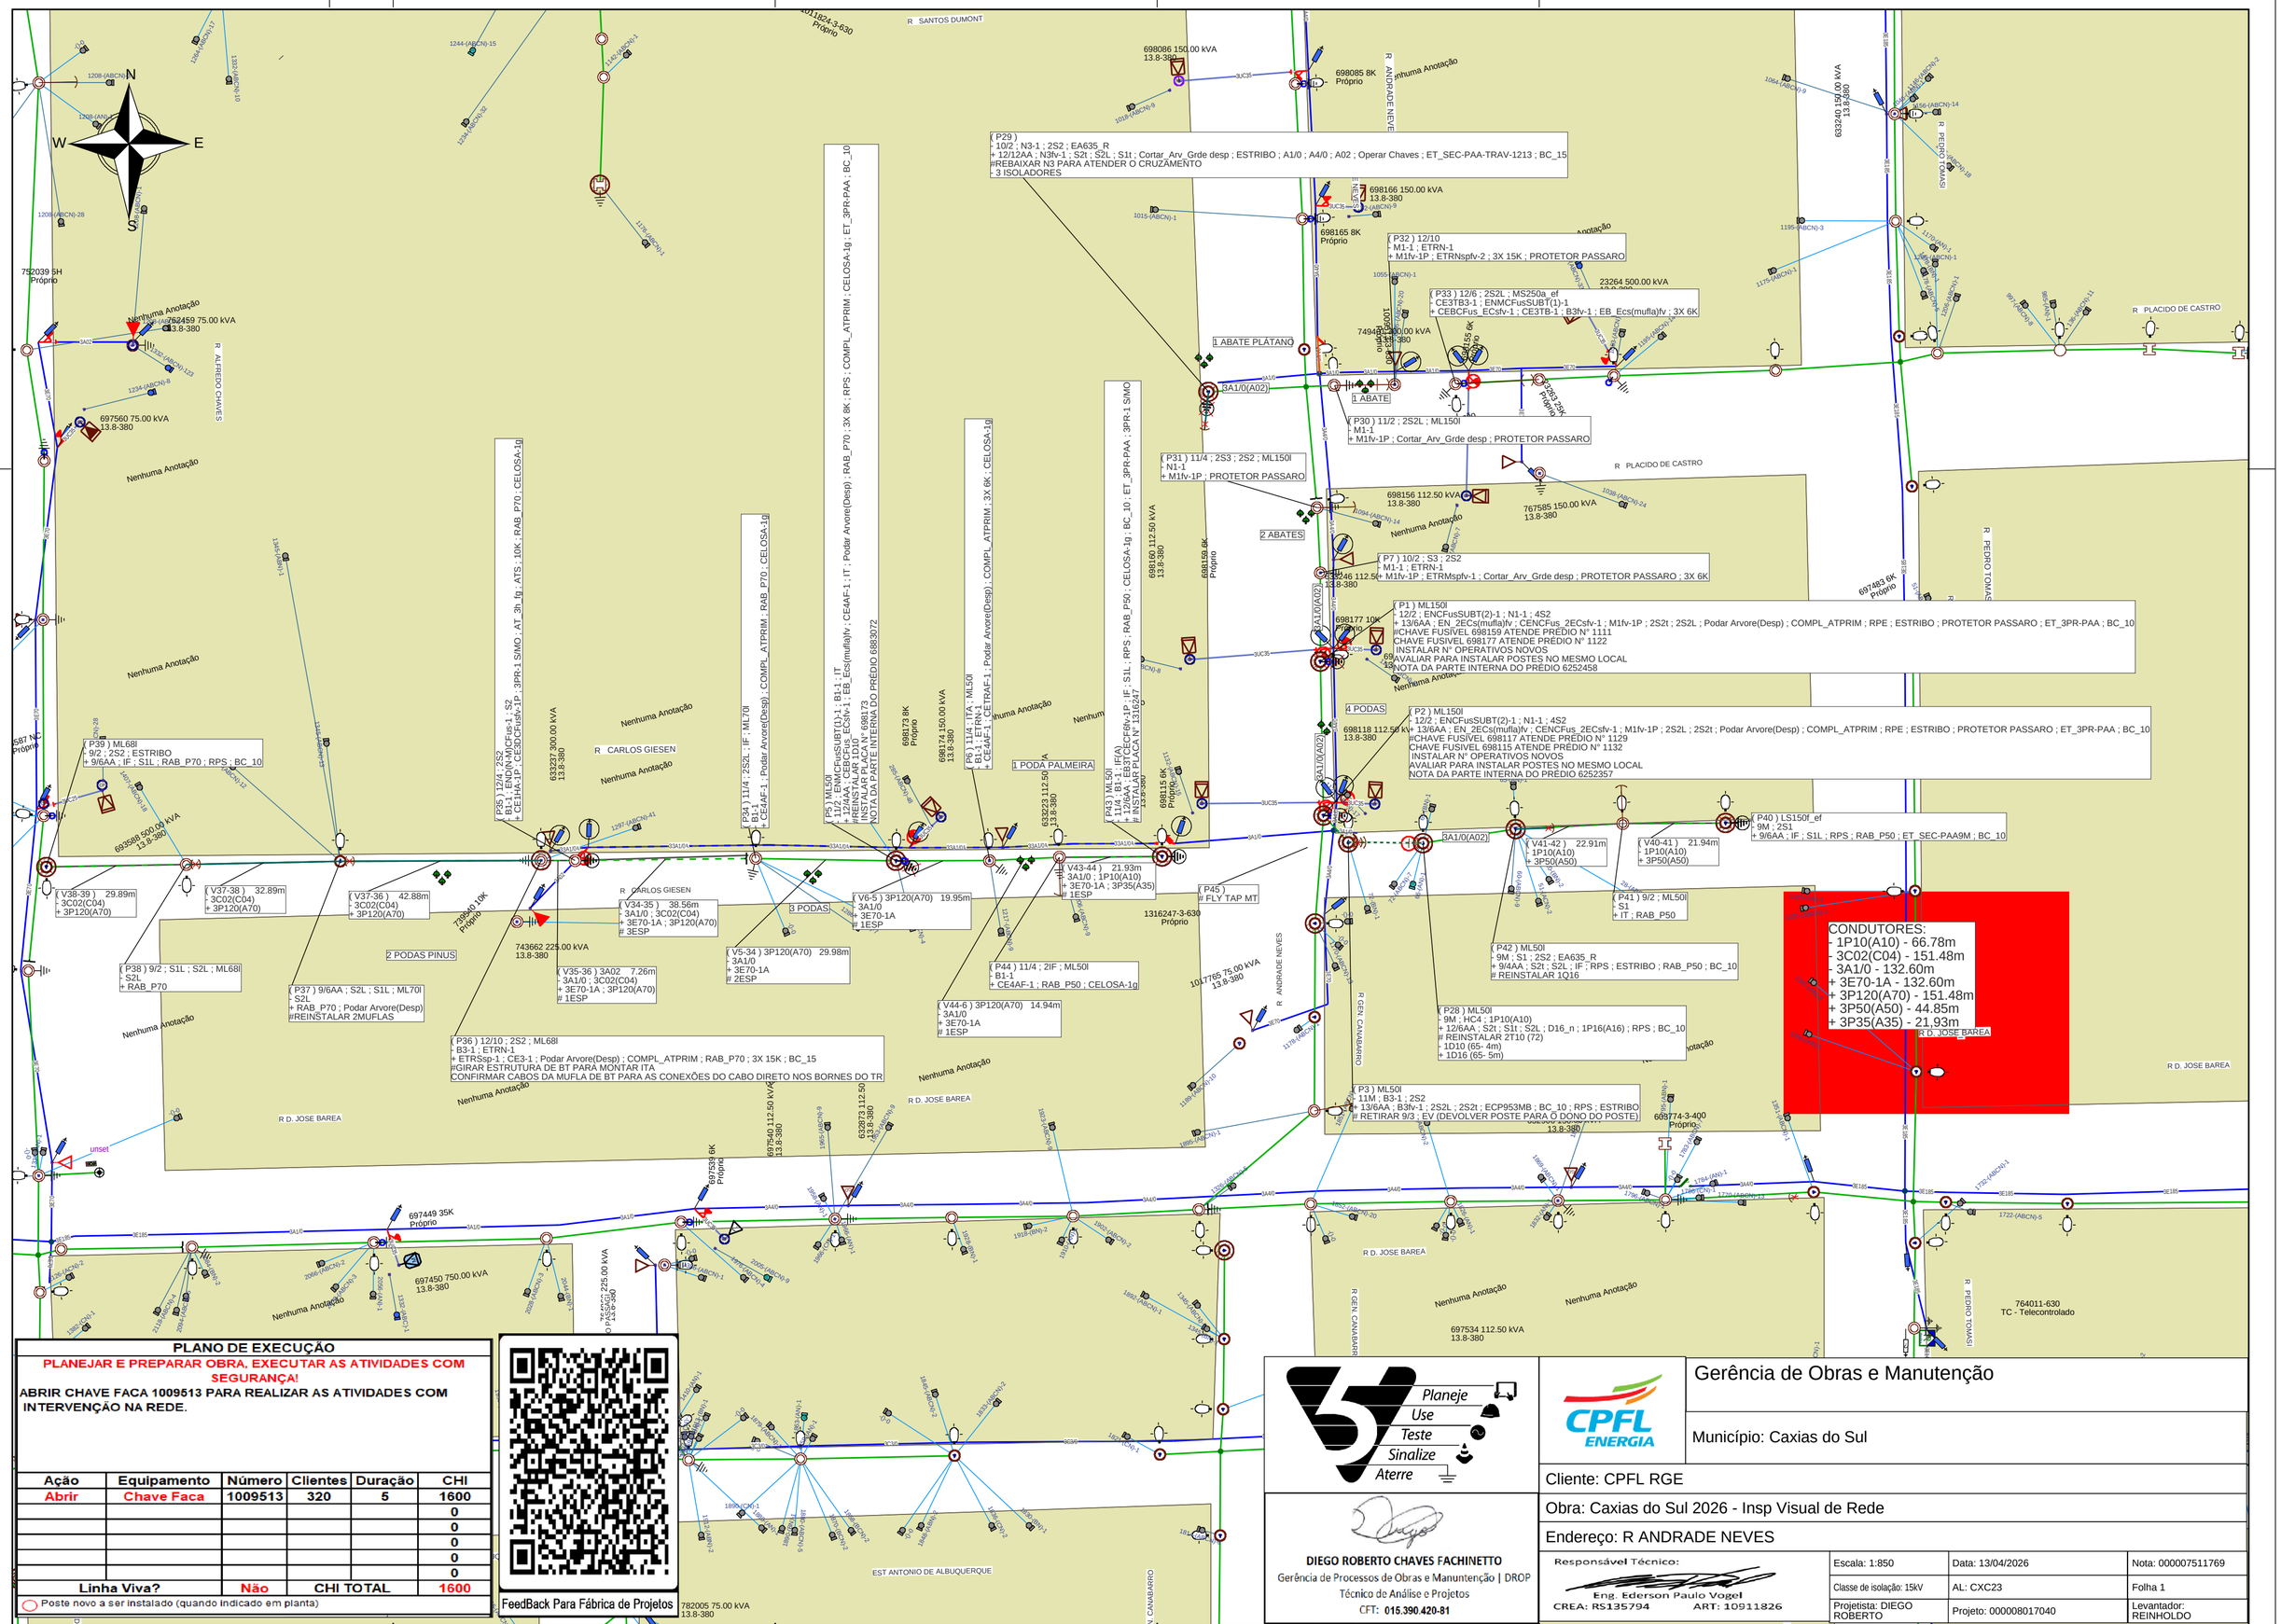


PLANO DE EXECUÇÃO

PLANEJAR E PREPARAR OBRA, EXECUTAR AS ATIVIDADES COM SEGURANÇA!

ABRIR CHAVE FACA 1009513 PARA REALIZAR AS ATIVIDADES COM INTERVENÇÃO NA REDE.

Ação	Equipamento	Número	Clientes	Duração	CHI
Abrir	Chave Faca	1009513	320	5	1600
					0
					0
					0
					0
					0
Linha Viva?		Não	CHI TOTAL		1600

Poste novo a ser instalado (quando indicado em planta)

FeedBack Para Fábrica de Projetos

Planeje
Use
Teste
Sinalize
Aterre

DIEGO ROBERTO CHAVES FACHINETTO
Gerência de Processos de Obras e Manuntenção | DROP
Técnico de Análise e Projetos
CFT: 015.390.420-81

CPFL ENERGIA

Gerência de Obras e Manutenção

Município: Caxias do Sul

Cliente: CPFL RGE

Obra: Caxias do Sul 2026 - Insp Visual de Rede

Endereço: R ANDRADE NEVES

Responsável Técnico:
Eng. Ederson Paulo Vogel
CREA: RS135794 ART: 10911826

Escala: 1:850	Data: 13/04/2026	Nota: 000007511769
Classe de isolação: 15kV	AL: CXC23	Folha 1
Projetista: DIEGO ROBERTO	Projeto: 000008017040	Levantador: REINHOLDO