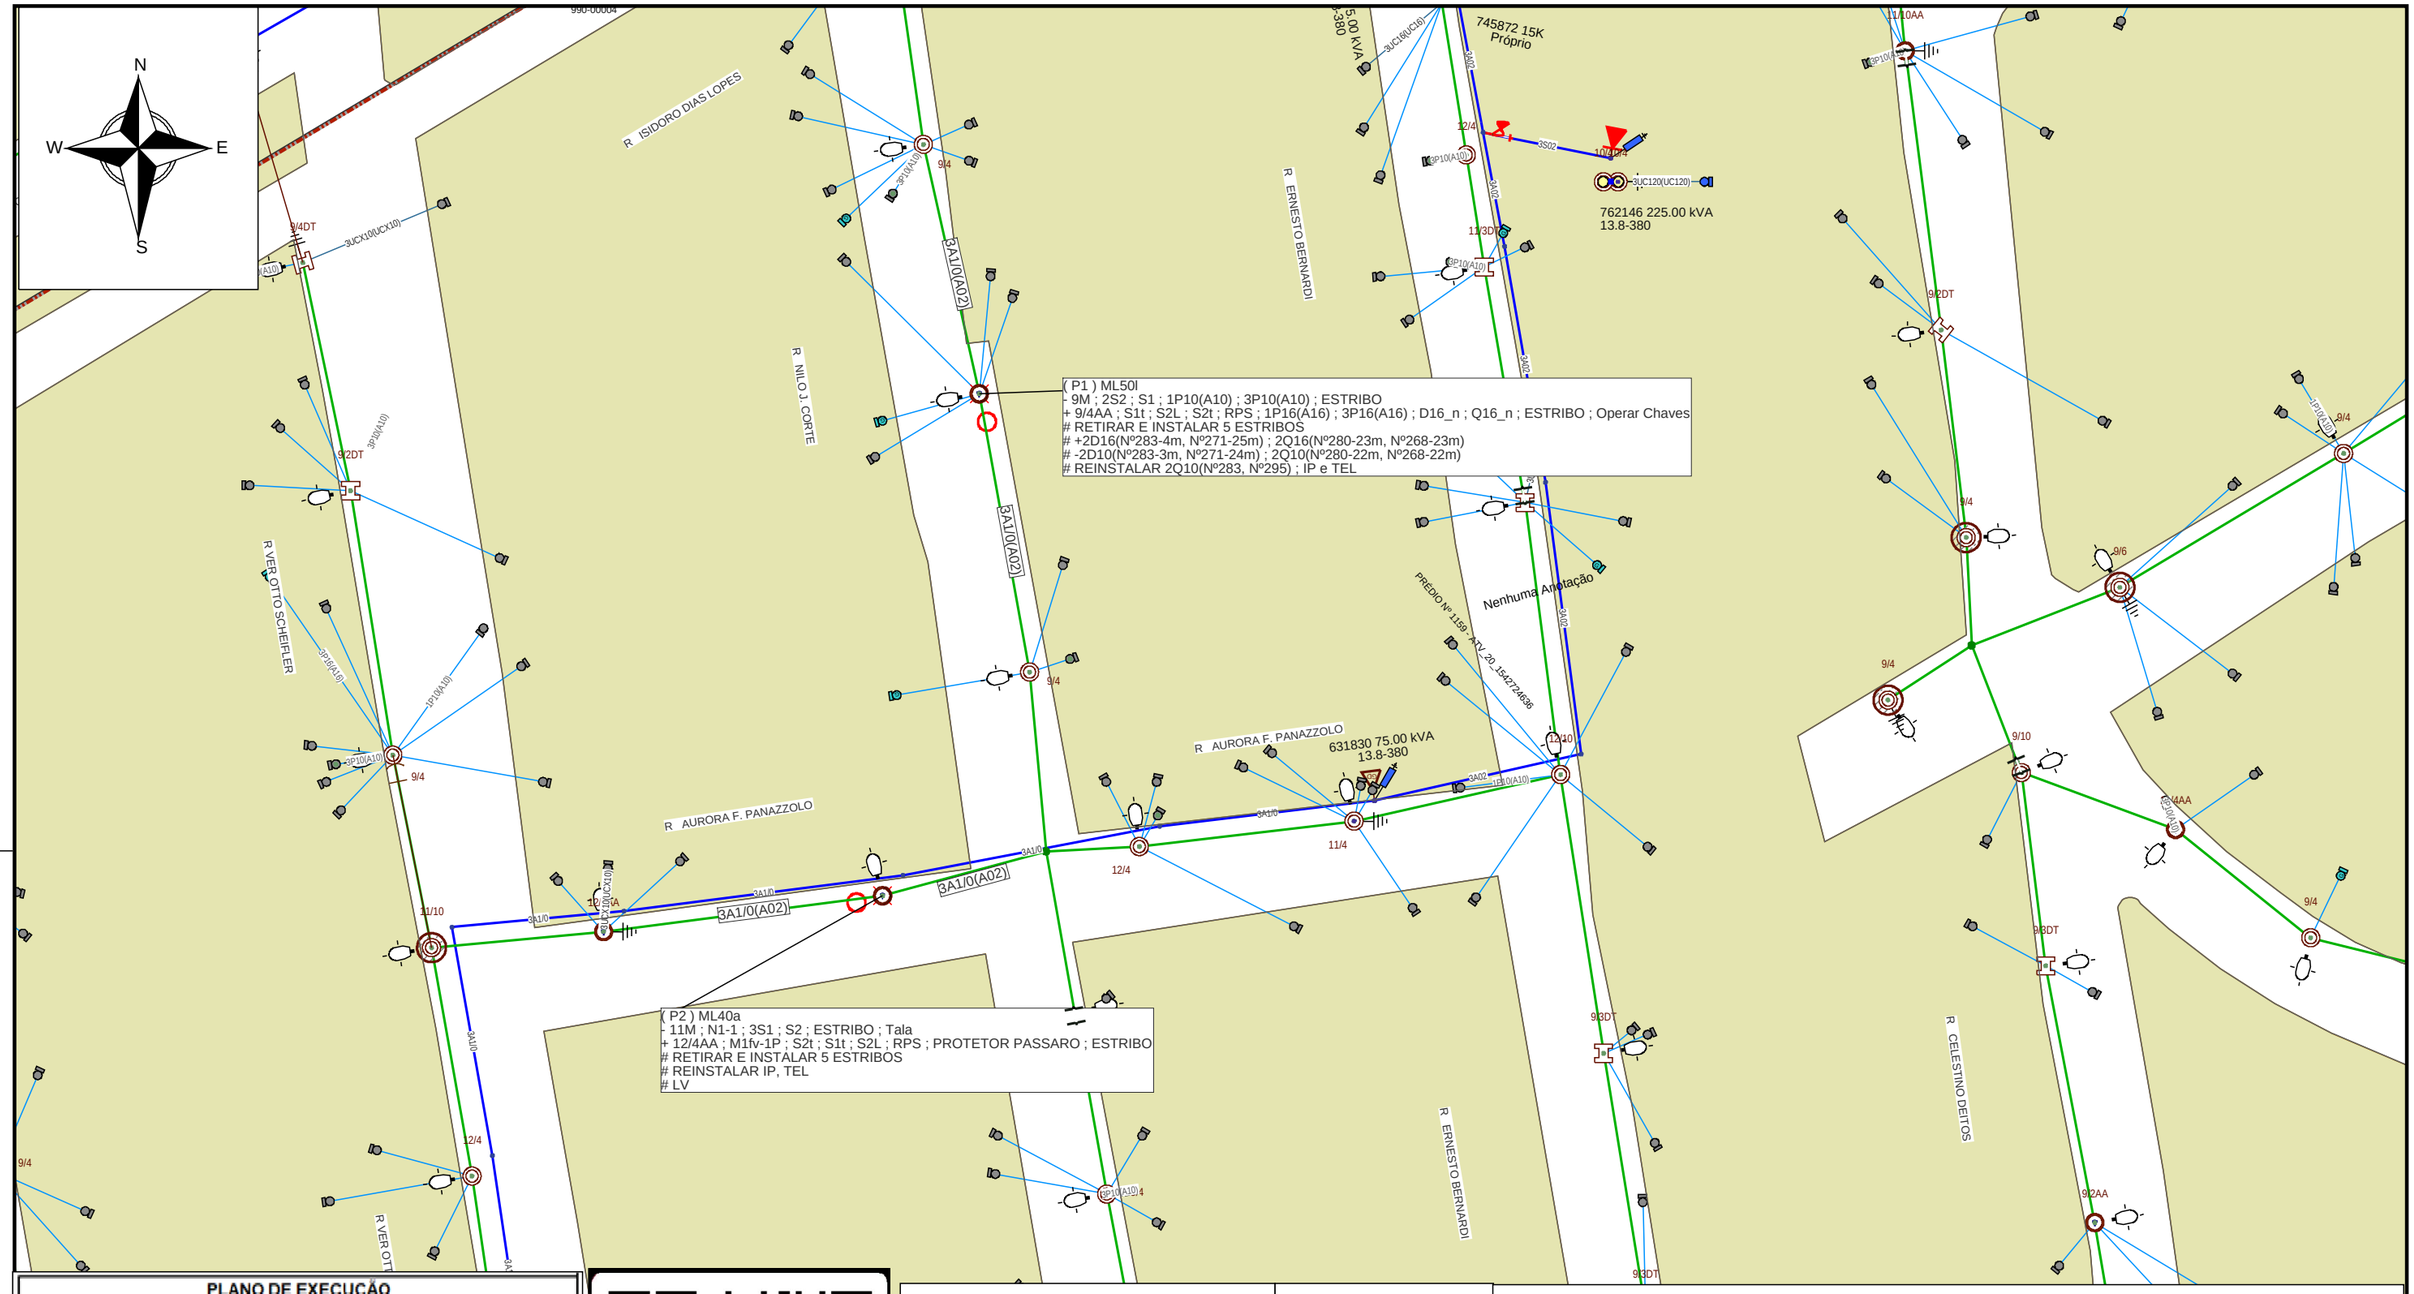


PLANO DE EXECUÇÃO

Abrir cavas e preparar a obra.
Substituir 2 postes conforme projeto.
Intervir no P2 em regime de LV desligando o TR 631830.
Manobras pagas no P1.

****EXECUTAR AS ATIVIDADES COM SEGURANÇA E CAPRICHO.****

Ação	Equipamento	Número	Clientes	Duração	CHI
Abrir	Transformador	631830	115	4	460
Linha Viva?		Sim	CHI TOTAL		460

FeedBack Para Fábrica de Projetos

Planeje
Use
Teste
Sinalize
Aterre

Frederico Holsbach

FREDERICO JOÃO HOLSBACH
Gerência Obras e Manutenção
Técnico de Processos O&M
CFT-BR : 02506034030

CPFL ENERGIA

Gerência de Obras e Manutenção

Município: Caxias do Sul

Cliente: RGE SUL DISTRIBUIDORA DE ENERGIA S.A

Obra: Substituição de Poste - OS 101183260

Endereço: R NILO JOSÉ CORTE, B DESVIO RIZZO

Responsável Técnico:
Eng. Ederson Paulo Vogel
CREA: RS135794 ART: 10911826

Escala: 1:850	Data: 20/04/2026	Nota: 000007514669
Classe de isolação: 15kV	AL: CXH44	Folha 1
Projetista: Frederico	Projeto: 000008021208	Levantador: Reinholdo Brulinger